


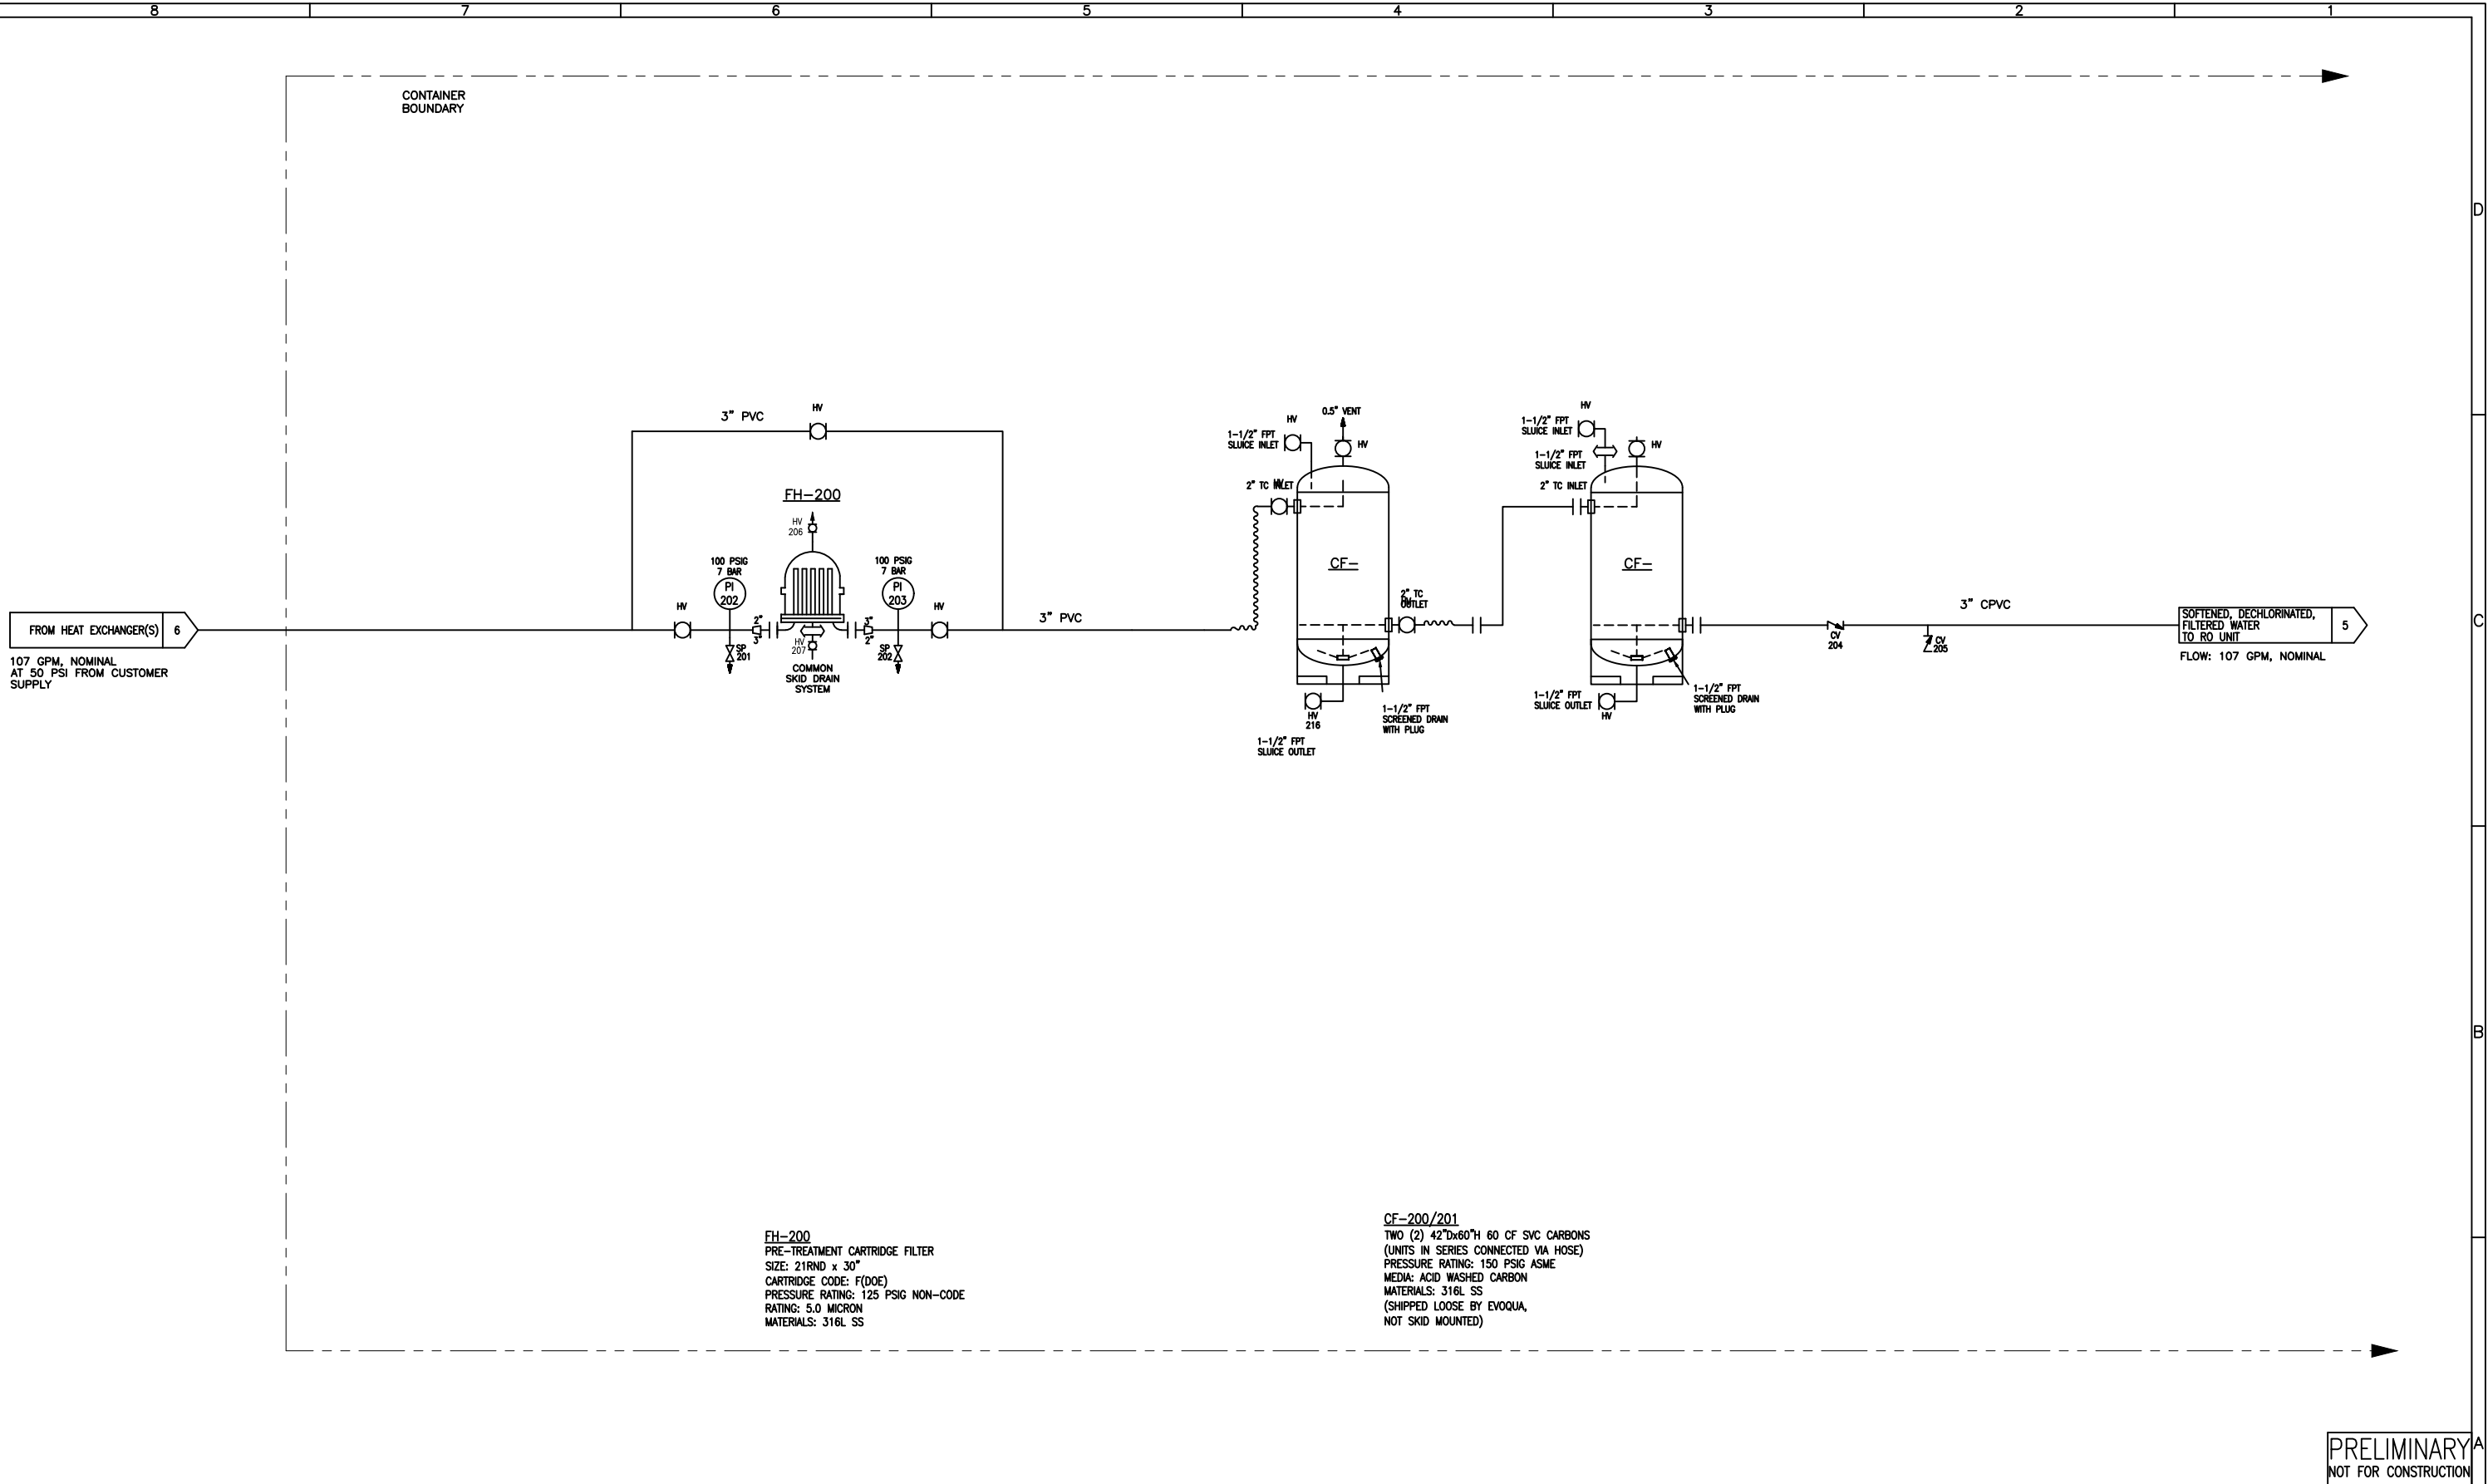


FH-200
PRE-TREATMENT CARTRIDGE FILTER
SIZE: 21RND x 30"
CARTRIDGE CODE: F(DOE)
PRESSURE RATING: 125 PSIG NON-CODE
RATING: 5.0 MICRON
MATERIALS: 316L SS


CF-200/201
TWO (2) 42"Dx60"H 60 CF SVC CARBONS
(UNITS IN SERIES CONNECTED VIA HOSE)
PRESSURE RATING: 150 PSIG ASME
MEDIA: ACID WASHED CARBON
MATERIALS: 316L SS
(SHIPPED LOOSE BY EVOQUA,
NOT SKID MOUNTED)

PRELIMINARY^A
NOT FOR CONSTRUCTION

STD: BORDER-0106-24X36D1	INTL REF:	BAR = 1" AT PLOT SCALE	REV	DESCRIPTION	DATE	DWN	CHKD	APVD	ECN	COMPANY CONFIDENTIAL THIS DOCUMENT AND ALL INFORMATION CONTAINED HEREIN ARE THE PROPERTY OF EVOQUA AND/OR ITS AFFILIATES. THE DESIGN CONCEPTS AND INFORMATION CONTAINED HEREIN ARE PROPRIETARY TO EVOQUA AND ARE SUBMITTED IN CONFIDENCE. THEY ARE NOT TRANSFERABLE AND MUST BE USED ONLY FOR THE PURPOSE FOR WHICH THE DOCUMENT IS EXPRESSLY LOANED. THEY MUST NOT BE DISCLOSED, REPRODUCED, LOANED OR USED IN ANY OTHER MANNER WITHOUT THE EXPRESS WRITTEN CONSENT OF EVOQUA. IN NO EVENT SHALL THEY BE USED IN ANY MANNER DETRIMENTAL TO THE INTEREST OF EVOQUA. ALL PATENT RIGHTS ARE RESERVED. UPON THE DEMAND OF EVOQUA, THIS DOCUMENT, ALONG WITH ALL COPIES AND EXTRACTS, AND ALL RELATED NOTES AND ANALYSES, MUST BE RETURNED TO EVOQUA OR DESTROYED, AS INSTRUCTED BY EVOQUA. ACCEPTANCE OF THE DELIVERY OF THIS DOCUMENT CONSTITUTES AGREEMENT TO THESE TERMS.	DESIGNER	DATE	TITLE PROCESS AND INSTRUMENTATION DIAGRAM													
											CHECKER	DATE	WATER TECHNOLOGIES COLORADO SPRINGS, CO 719-570-9600													
											ENGINEER	DATE														
											MANAGER	DATE														
											FILE:											SCALE: NONE				
											- SEE SHEET ONE											PROJECT	CODE	DRAWING	SHEET 3 OF 8	REV A

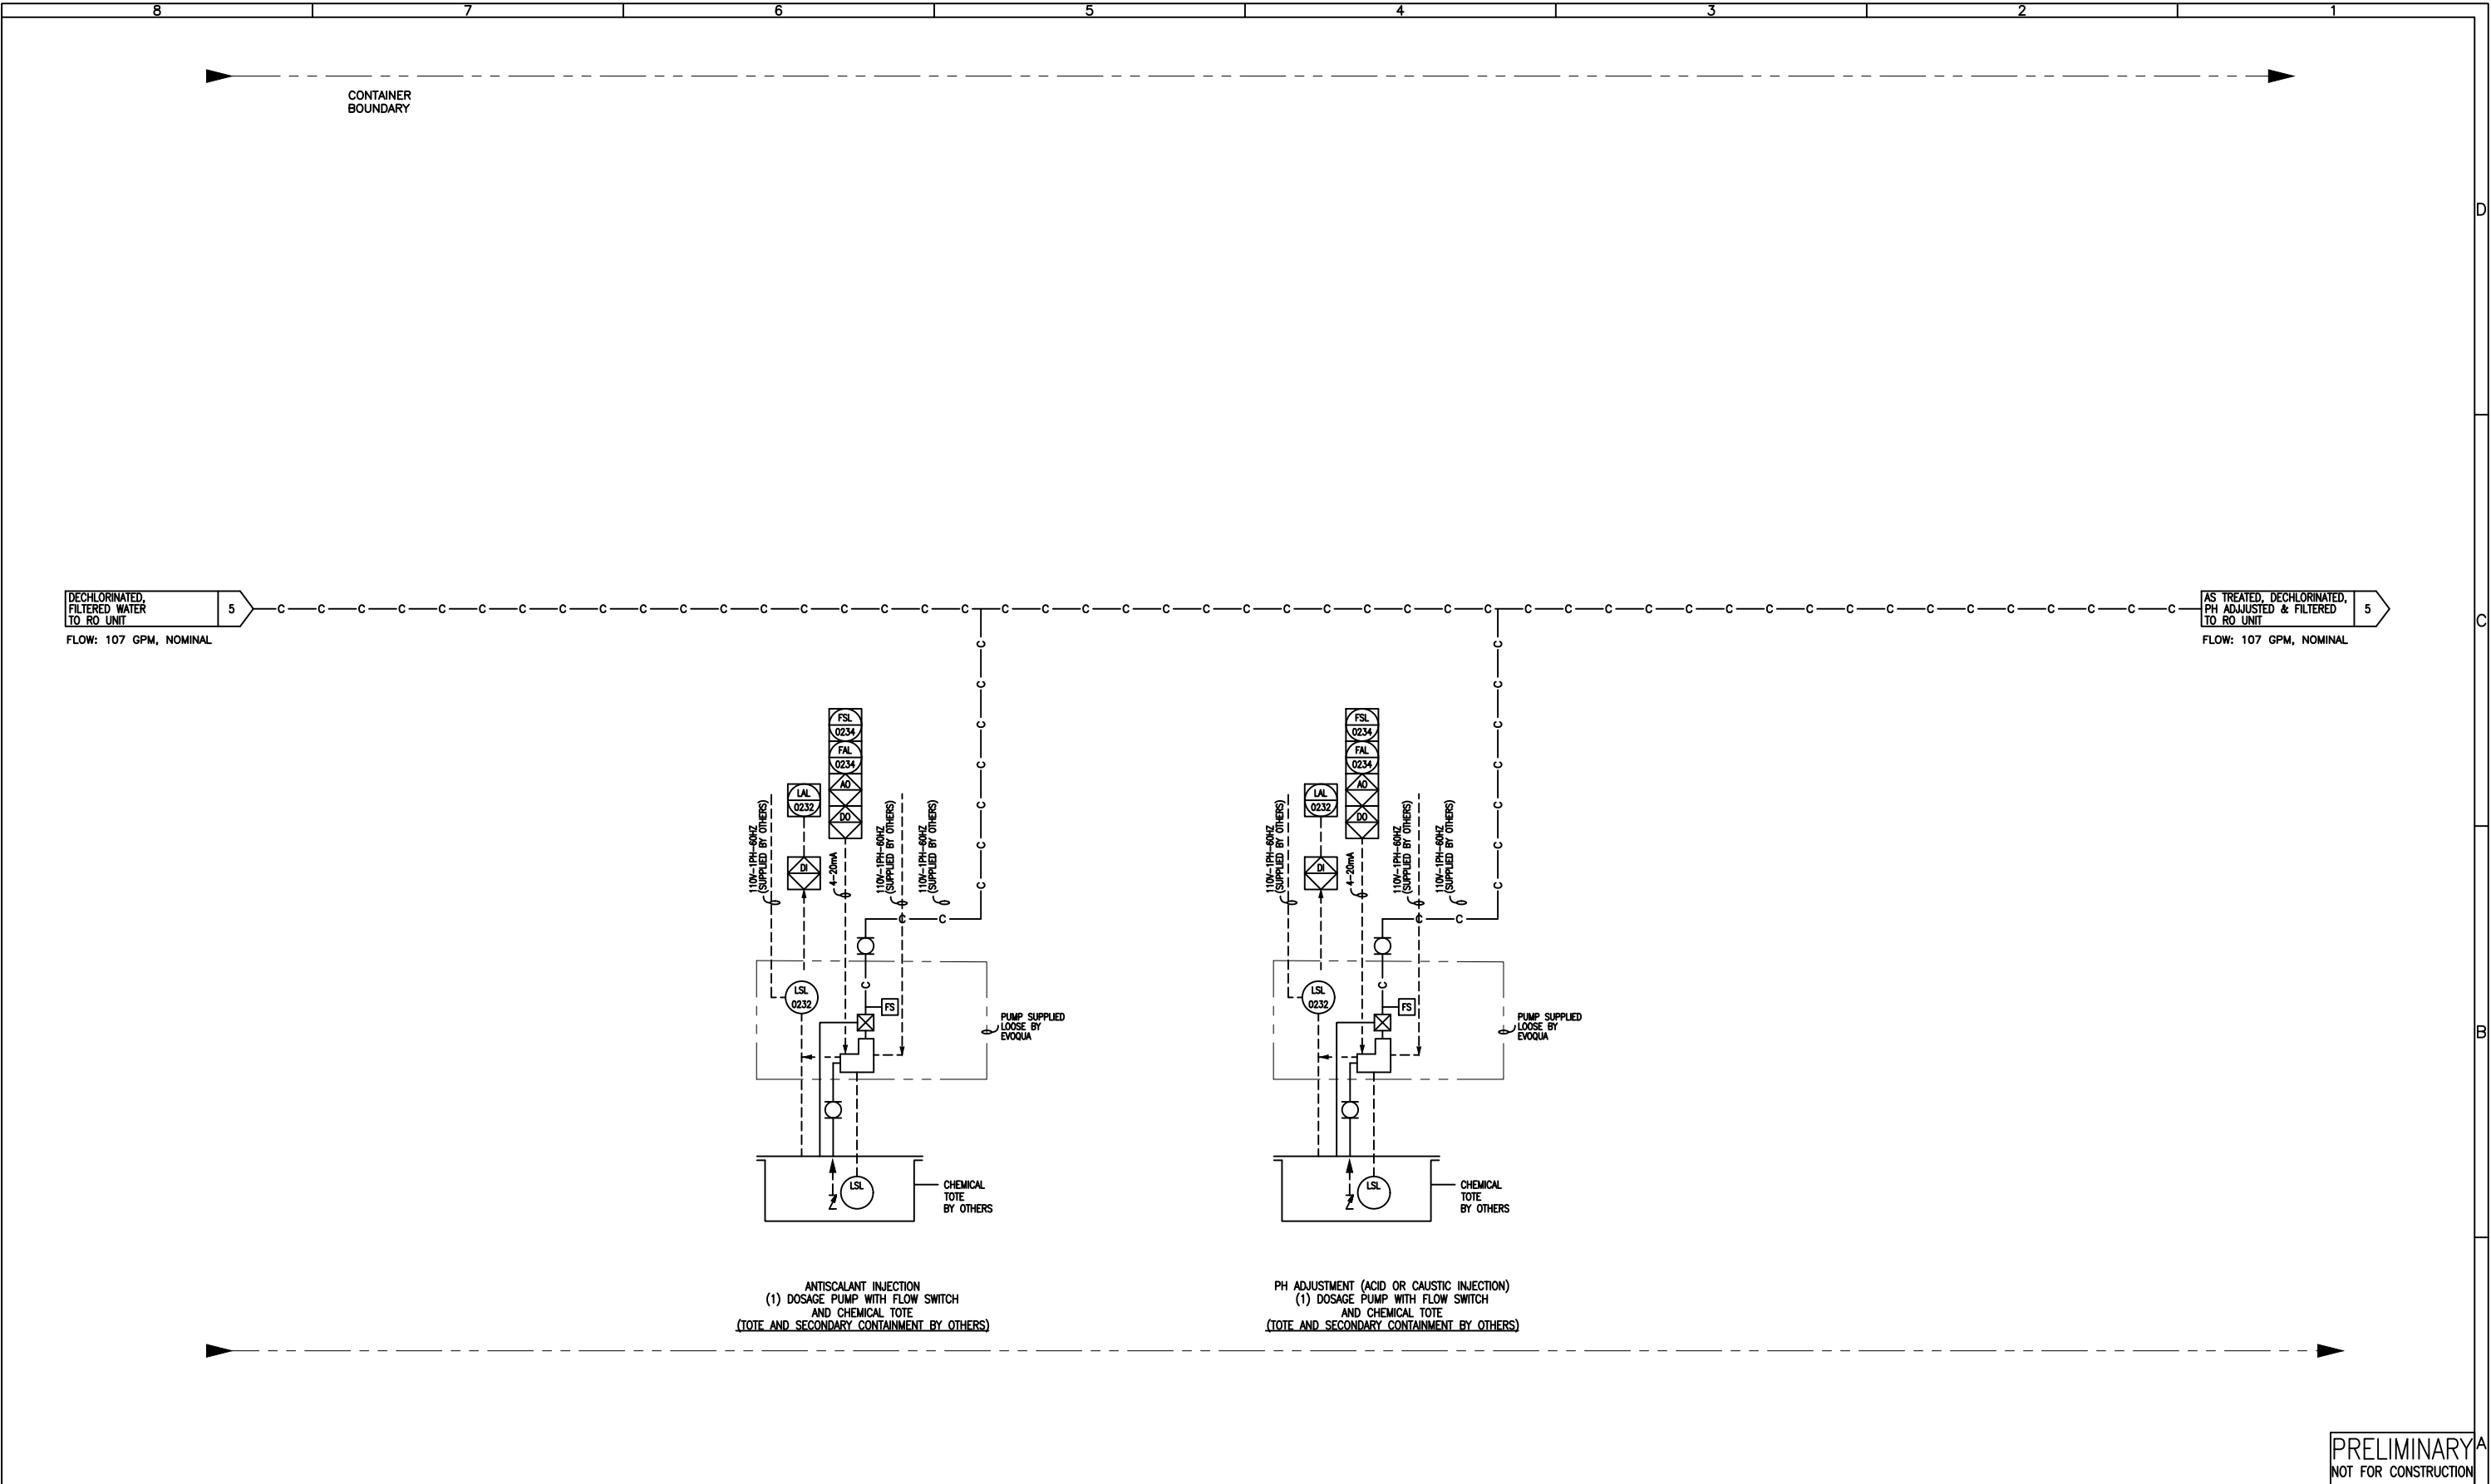

--	--	

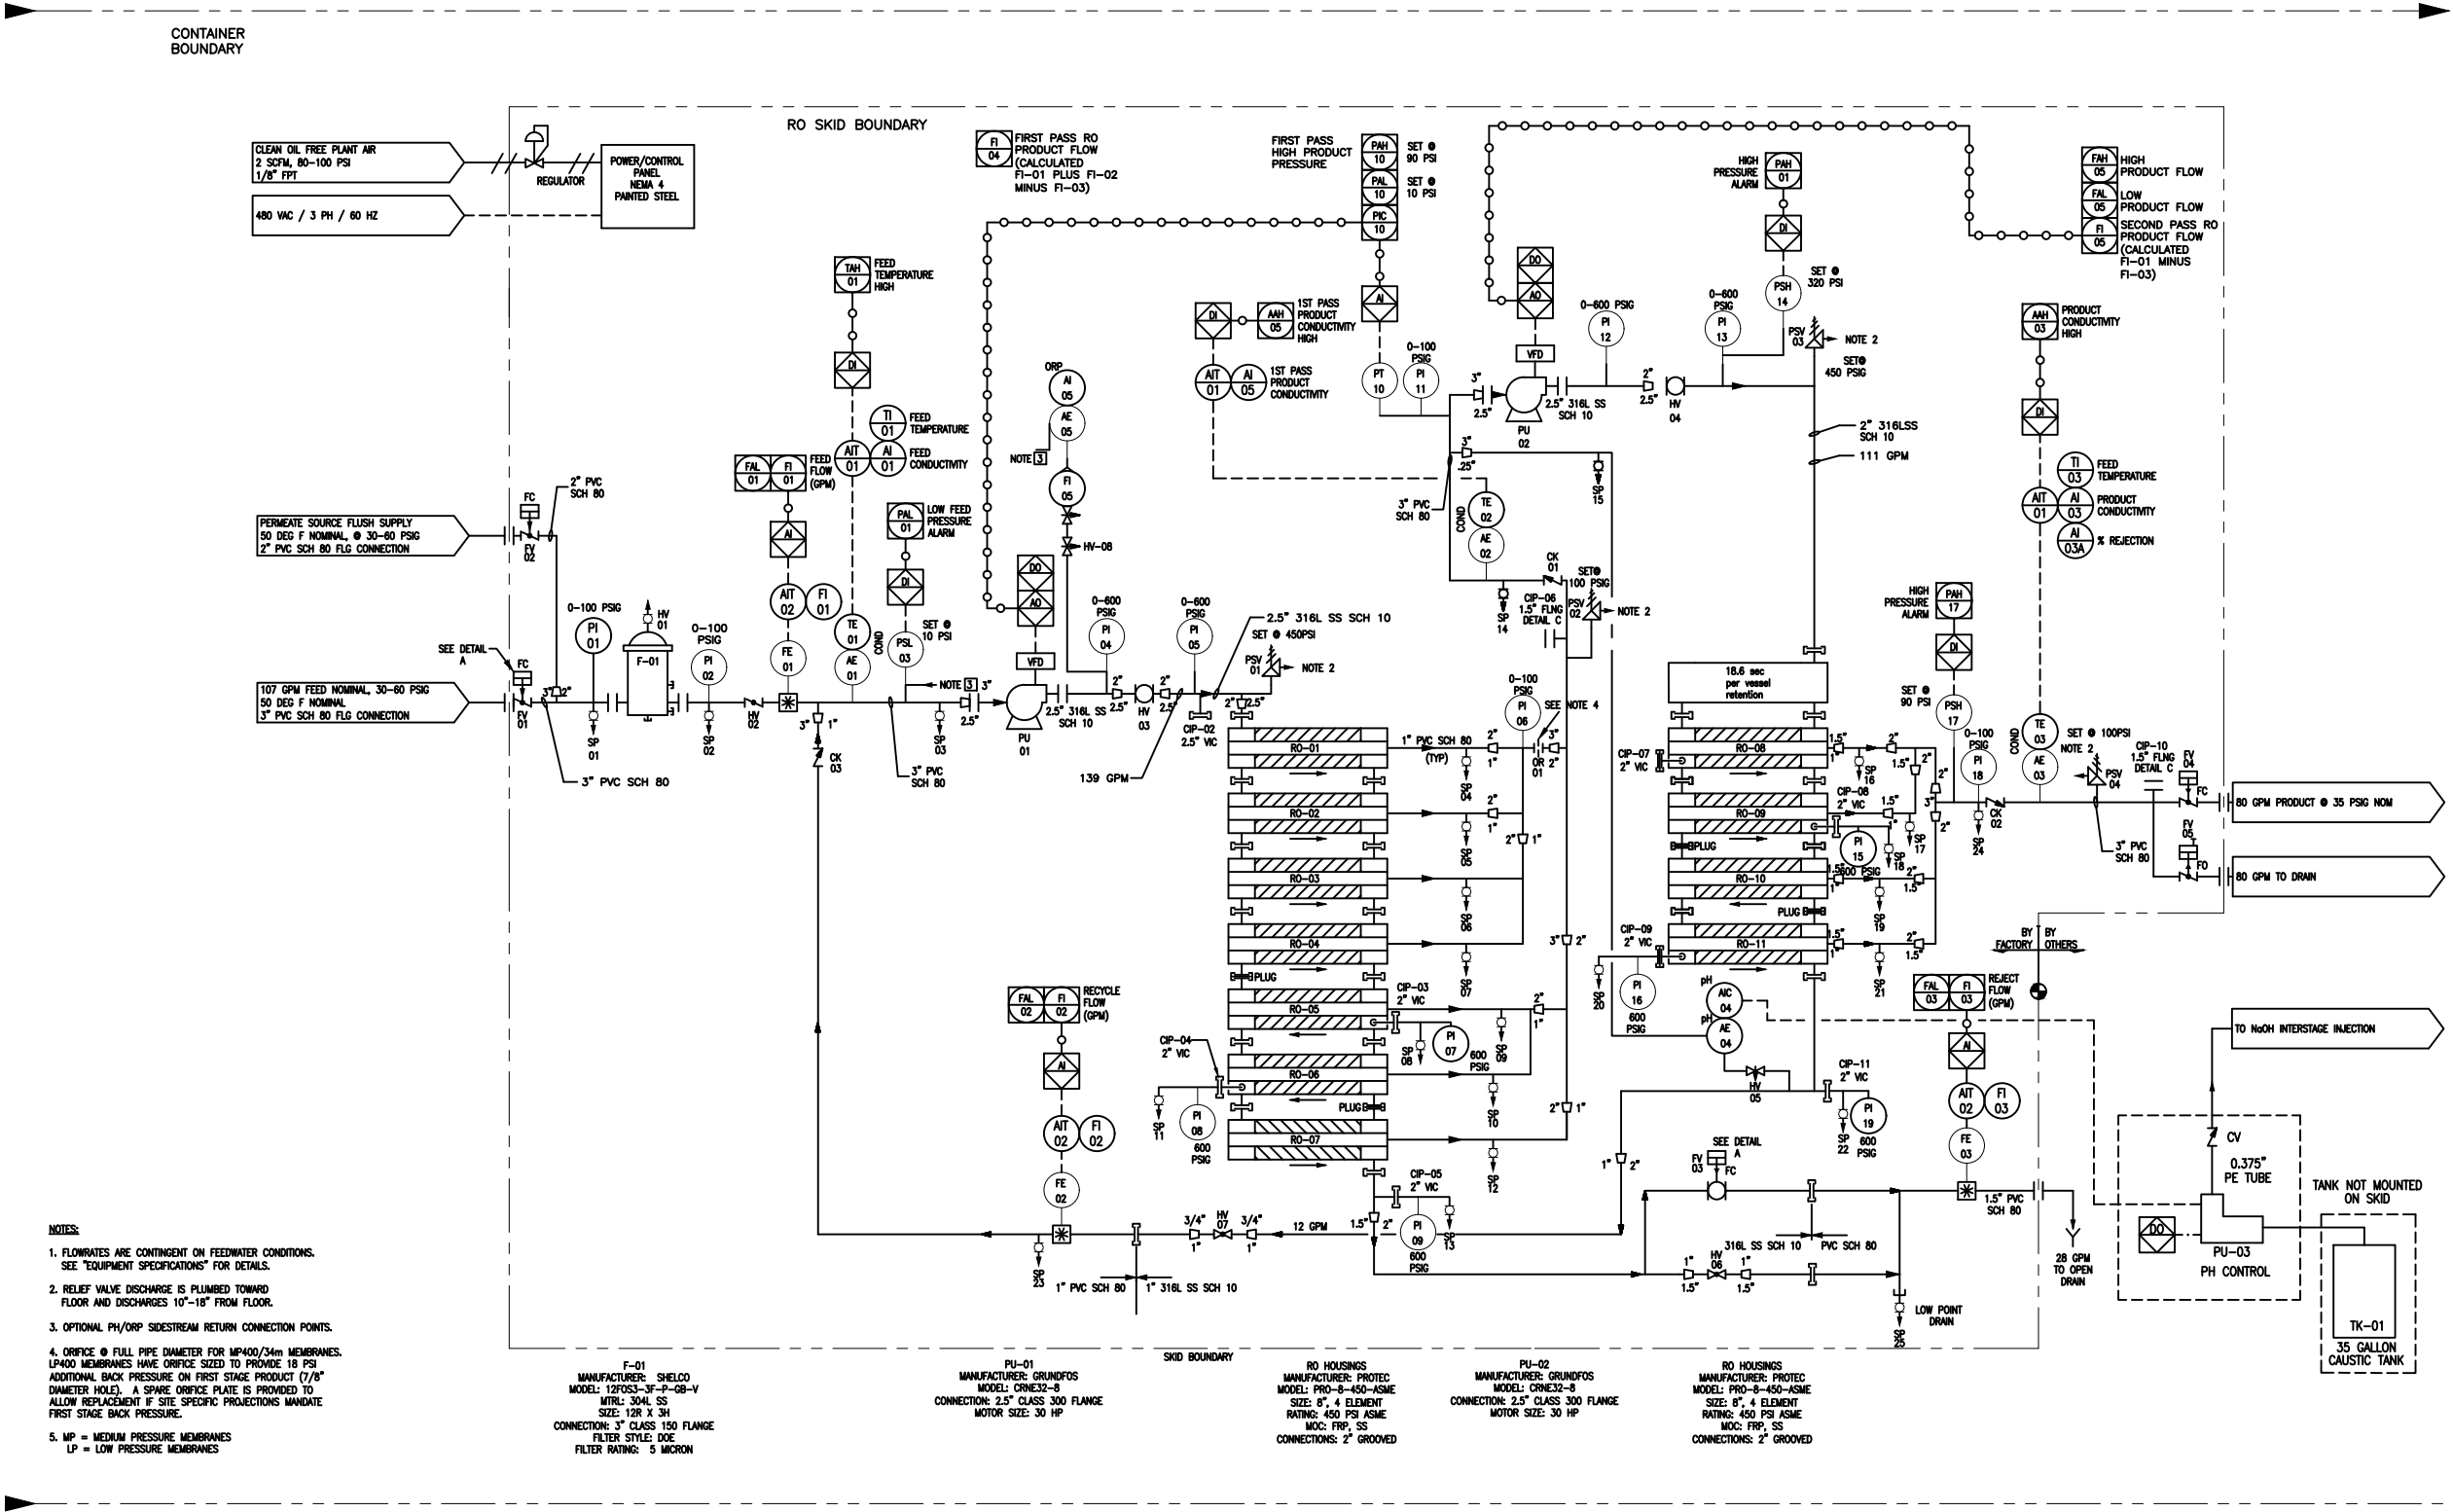

- NOTES:
1. FLOWRATES ARE CONTINGENT ON FEEDWATER CONDITIONS. SEE "EQUIPMENT SPECIFICATIONS" FOR DETAILS.
 2. RELIEF VALVE DISCHARGE IS PLUMBED TOWARD FLOOR AND DISCHARGES 10'-18" FROM FLOOR.
 3. OPTIONAL PH/ORP SIDESTREAM RETURN CONNECTION POINTS.
 4. ORIFICE @ FULL PIPE DIAMETER FOR MP400/34in MEMBRANES. LP400 MEMBRANES HAVE ORIFICE SIZED TO PROVIDE 18 PSI ADDITIONAL BACK PRESSURE ON FIRST STAGE PRODUCT (7/8" DIAMETER HOLE). A SPARE ORIFICE PLATE IS PROVIDED TO ALLOW REPLACEMENT IF SITE SPECIFIC PROJECTIONS MANDATE FIRST STAGE BACK PRESSURE.
 5. MP = MEDIUM PRESSURE MEMBRANES
LP = LOW PRESSURE MEMBRANES


F-01
MANUFACTURER: SHELCO
MODEL: 12FOS3-3F-P-08-V
MTRL: 304L SS
SIZE: 12N X 3H
CONNECTION: 3" CLASS 150 FLANGE
FILTER STYLE: DOE
FILTER RATING: 5 MICRON

PU-01
MANUFACTURER: GRUNDFOS
MODEL: CRNE32-8
CONNECTION: 2.5" CLASS 300 FLANGE
MOTOR SIZE: 30 HP

RO HOUSINGS
MANUFACTURER: PROTEC
MODEL: PRO-8-450-ASME
SIZE: 8", 4 ELEMENT
RATING: 450 PSI ASME
MOC: FRP, SS
CONNECTIONS: 2" GROOVED


PU-02
MANUFACTURER: GRUNDFOS
MODEL: CRNE32-8
CONNECTION: 2.5" CLASS 300 FLANGE
MOTOR SIZE: 30 HP

RO HOUSINGS
MANUFACTURER: PROTEC
MODEL: PRO-8-450-ASME
SIZE: 8", 4 ELEMENT
RATING: 450 PSI ASME
MOC: FRP, SS
CONNECTIONS: 2" GROOVED

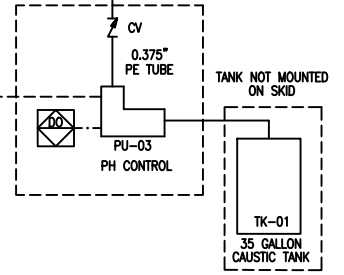

PRELIMINARY
NOT FOR CONSTRUCTION

--	--	

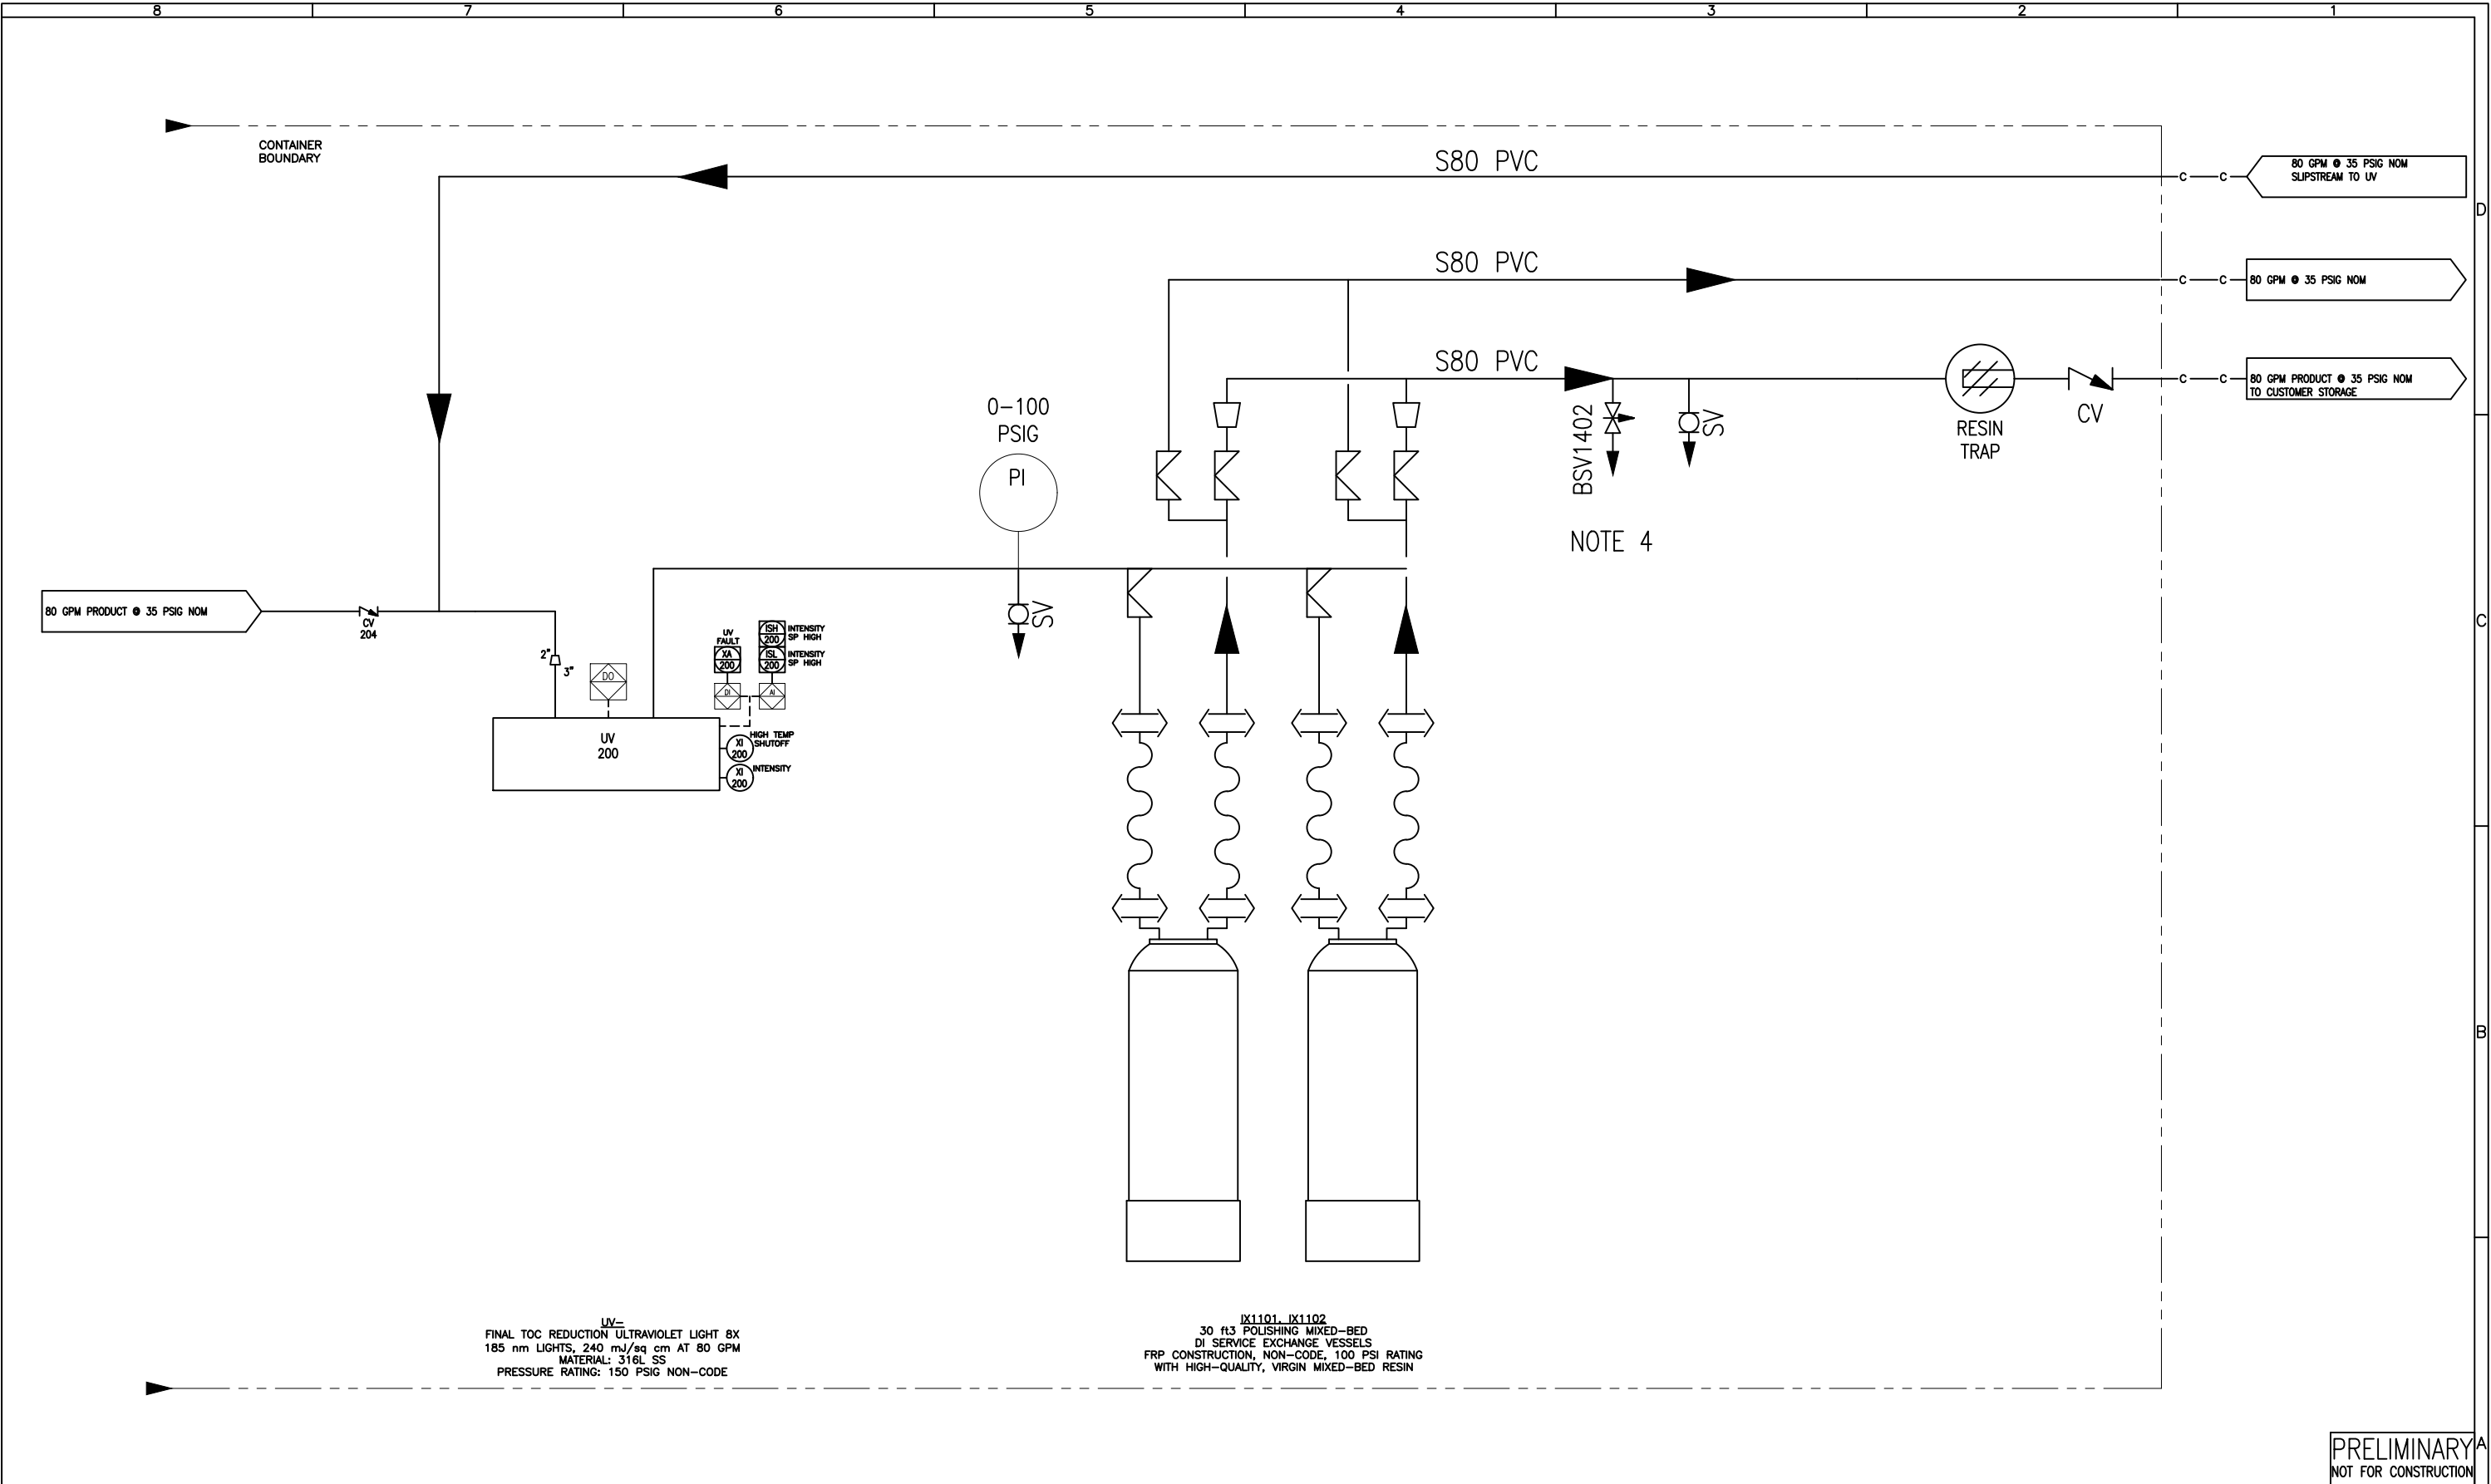

UV=
FINAL TOC REDUCTION ULTRAVIOLET LIGHT 8X
185 nm LIGHTS, 240 mJ/sq cm AT 80 GPM
MATERIAL: 316L SS
PRESSURE RATING: 150 PSIG NON-CODE

IX1101, IX1102
30 ft3 POLISHING MIXED-BED
DI SERVICE EXCHANGE VESSELS
FRP CONSTRUCTION, NON-CODE, 100 PSI RATING
WITH HIGH-QUALITY, VIRGIN MIXED-BED RESIN

PRELIMINARY
NOT FOR CONSTRUCTION

--	--	