

evoQUA
WATER TECHNOLOGIES

ELECTRIC HYDROGEN
BEAUMONT, TX
PROJECT NUMBER: 2034/001845

	Project No.: 22MH194		
	P.O. No.:	8027	Tag No.:
1	Approved Without Comments		
2	Approved With Comments; Revise and Resubmit		
3	Revise and Resubmit		
4	For Information Only		
5	Certified as Final Data		

Ron Perego		9/4/24
Project Manager		Date
Bart Rajtar		9/3/24
Project Engineer		Date
Mark Burton		8/21/24
EH2 Representative		Date

SHEET	PART NUMBER	FILENAME/DRAWING	DRAWING DESCRIPTION
1	W3T602509	V112057481-01	COVER SHEET
2	W3T602509	V112057481-02	ELECTRICAL SCHEMATIC NOTES
3	W3T602509	V112057481-03	POWER DISTRIBUTION - 480VAC
4	W3T602509	V112057481-04	POWER DISTRIBUTION - 120VAC - LOAD CENTER
5	W3T602509	V112057481-05	RELAY-USER TERMINALS
6	W3T602509	V112057481-06	ELECTRICAL ENCLOSURE NOTES & EXTERIOR DETAIL
7	W3T602509	V112057481-07	ELECTRICAL ENCLOSURE CUTOUT
8	W3T602509	V112057481-08	ELECTRICAL ENCLOSURE SUB PANEL LAYOUT
9	W3T602509	V112057481-09	ELECTRICAL TERMINAL LAYOUT
10	W3T602509	V112057481-10	ELECTRICAL NAME PLATE SCHEDULE

						COMPANY CONFIDENTIAL INFORMATION THIS DOCUMENT AND ALL INFORMATION CONTAINED HEREIN, INCLUDING THE DESIGN CONCEPTS AND THOSE ARISING THEREFROM, ARE THE PROPERTY OF EVOQUA AND/OR ITS AFFILIATES AND ARE SUBMITTED IN CONFIDENCE. THEY MAY BE USED ONLY FOR THE EXPRESS PURPOSE FOR WHICH THEY ARE PROVIDED AND MUST NOT BE DISCLOSED, REPRODUCED, OR COPIED IN ANY FORM, INCLUDING IN ELECTRONIC FORMAT, LOANED OR USED IN ANY OTHER MANNER WITHOUT THE EXPRESS WRITTEN CONSENT OF EVOQUA. ALL PATENT RIGHTS ARE RESERVED. THIS DOCUMENT AND DERIVATIVE WORKS THEREOF ARE PROTECTED UNDER APPLICABLE COPYRIGHT LAWS. UPON DEMAND OF EVOQUA, THIS DOCUMENT, ALONG WITH ALL COPIES AND EXTRACTS, AND ALL RELATED NOTES AND ANALYSES MUST BE RETURNED TO EVOQUA OR DESTROYED, AS INSTRUCTED BY EVOQUA. ACCEPTANCE OF THE DELIVERY OF THIS DOCUMENT CONSTITUTES AGREEMENT TO THESE TERMS.	DWN BY:	DATE	TITLE			
							C.HANER	2023-11-17	ELECTRICAL SCHEMATIC DIAGRAM (CETLUS) CONTAINER POWER DISTRIBUTION PANEL PDP-0107			
							CKD BY:	DATE	CLIENT			
							K.KALUNG	2023-11-17	ELECTRIC HYDROGEN BEAUMONT, TX			
							APPD BY:	DATE				
							K.KALUNG	2023-11-17				
							MGD BY:	SCALE	EVOQUA WATER TECHNOLOGIES COLORADO SPRINGS CO USA +1 719-570-9600			
							P.RYAN	NTS				
							PART NUMBER	PROJ/PROD NUMBER	CODE	FILE/DRAWING NUMBER	SHEET	REV
						W3T602509	2034/001845	EC-DOS03	V112057481-01	1 OF 10	2	

2	RE-ISSUED FOR CONSTRUCTION, ADD HEAT TRACED REVISED INCOMING POWER TO MAIN CIRCUIT BREAKER	2034-08-13	C.HANER	K.KALUNG	K.KALUNG	ECM128202
1	REVISE SCHEMATIC NOTE #3	2024-05-14	C.HANER	K.KALUNG	K.KALUNG	ECM127665
0	ISSUED FOR CONSTRUCTION	2023-12-27	C.HANER	K.KALUNG	K.KALUNG	N/A
REV	DESCRIPTION	DATE	DWN	CKD	APPD	ECN

ELECTRICAL SCHEMATIC NOTES

NOTES: UNLESS OTHERWISE SPECIFIED


1. ALL INTERNAL PANEL WIRING TO BE #14 AWG EXCEPT CLASS 2 CONTROL CIRCUITS AND PLC I/O TO BE #18 AWG.
2.  DENOTES REMOTE PANELS OR COMPONENT(S).
3. ALL FIELD WIRING TO BE COPPER CONDUCTORS SIZED AT MIN 60°C.
4. - - - - - DENOTES SKID WIRING BY FACTORY.
5. ----- DENOTES FIELD WIRING TO EXTERNAL COMPONENTS (BY OTHERS).
6. WIRE COLORS:

BLK	120/230V AND ABOVE POWER
RED	120/230V CONTROL
WHT	NEUTRAL
BLU	DC POSITIVE
BLU/WHT	DC UNGROUNDED COMMON
WHT/BLU	DC GROUNDED COMMON
ORG	EXTERNALLY POWERED OR UNGROUNDED CONDUCTORS REMAINING ENERGIZED WHEN MAIN SUPPLY CIRCUIT DISCONNECT IS IN OFF POSITION
WHT/ORG	DISCONNECT AC CIRCUIT CONDUCTOR REMAINING ENERGIZED WHEN MAIN SUPPLY CIRCUIT DISCONNECT IS IN OFF POSITION
GRN/YEL	GROUNDING
7. ALL SKID WIRING TO BE #14 AWG THHN MINIMUM, EXCEPT FOR MULTI-CONDUCTOR CABLES WITH OVERALL JACKET.
8. SHIELDED SIGNAL CABLE FOR CLASS 1 CONTROL CIRCUITS TO BE 600V BELDEN 1120A OR EQUIVALENT.
9. SHIELDED SIGNAL CABLE FOR CLASS 2 CONTROL CIRCUITS TO BE 300V BELDEN 8760 OR EQUIVALENT.
10. - - c - - c - - DENOTES CONTAINER WIRING BY FACTORY.



	Project No.: 22MH194		
	P.O. No.:	8027	Tag No.:
1	Approved Without Comments		
2	Approved With Comments; Revise and Resubmit		
3	Revise and Resubmit		
4	For Information Only		
5	Certified as Final Data		

<u>Ron Perego</u>	<u>9/4/24</u>
Project Manager	Date
<u>Bart Rajtar</u>	<u>9/3/24</u>
Project Engineer	Date
<u>Mark Burton</u>	<u>8/21/24</u>
EH2 Representative	Date


[illegible]

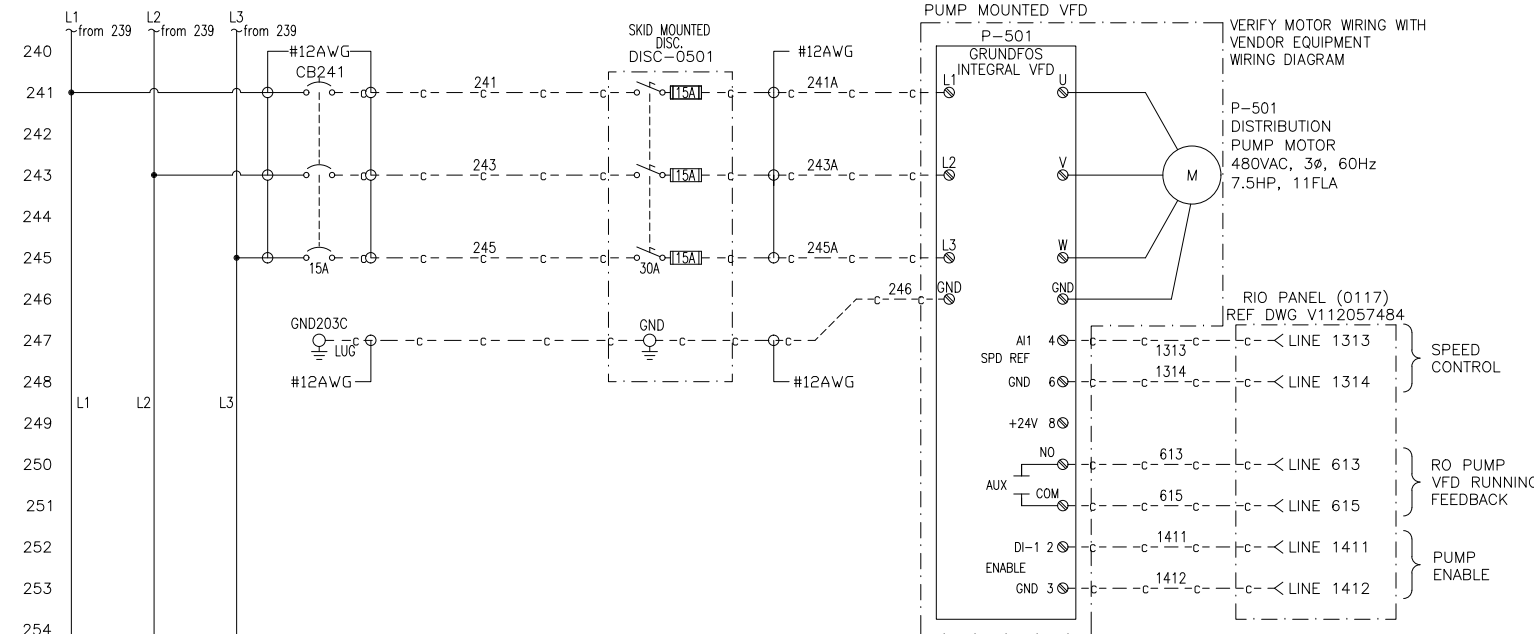[illegible]


1. THIS PANEL TO BE MOUNTED ON FRONT EXTERIOR OF CONTAINER.
2. THIS ENCLOSURE IS TO BE NEMA TYPE 4X STAINLESS STEEL.
3. MANUFACTURING TO LAYOUT BACKPANEL AS SHOWN.
4. MANUFACTURING TO VERIFY ALL DIMENSIONS AND CUTOUT SIZES BEFORE CUTTING OR DRILLING PANEL.
5. WIREWAY TO BE 4" DEEP.
6. DIN RAIL TO BE MOUNTED ON 1" STANDOFFS.
7. CONDUIT TO BE GRC.
8. DRAIN TO BE LOCATED AND INSTALLED BY SKID ELECTRIC.
9. TRANSFORMER MOUNTED ON THE INSIDE OF THE CONTAINER, SKID ELECTRICAL TO LOCATE AND MOUNT AT TIME OF ASSEMBLY.

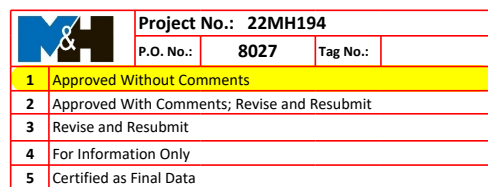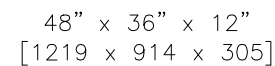[illegible]




NOTES: SEE SHEET ONE

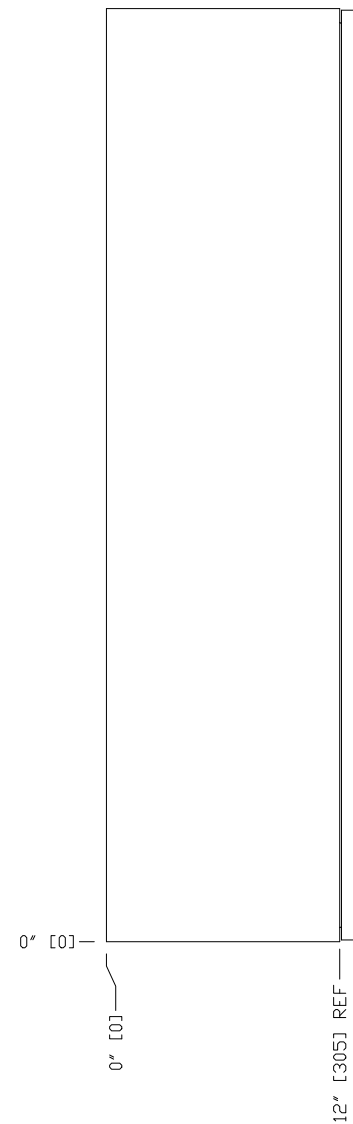

LEFT SIDE DETAIL

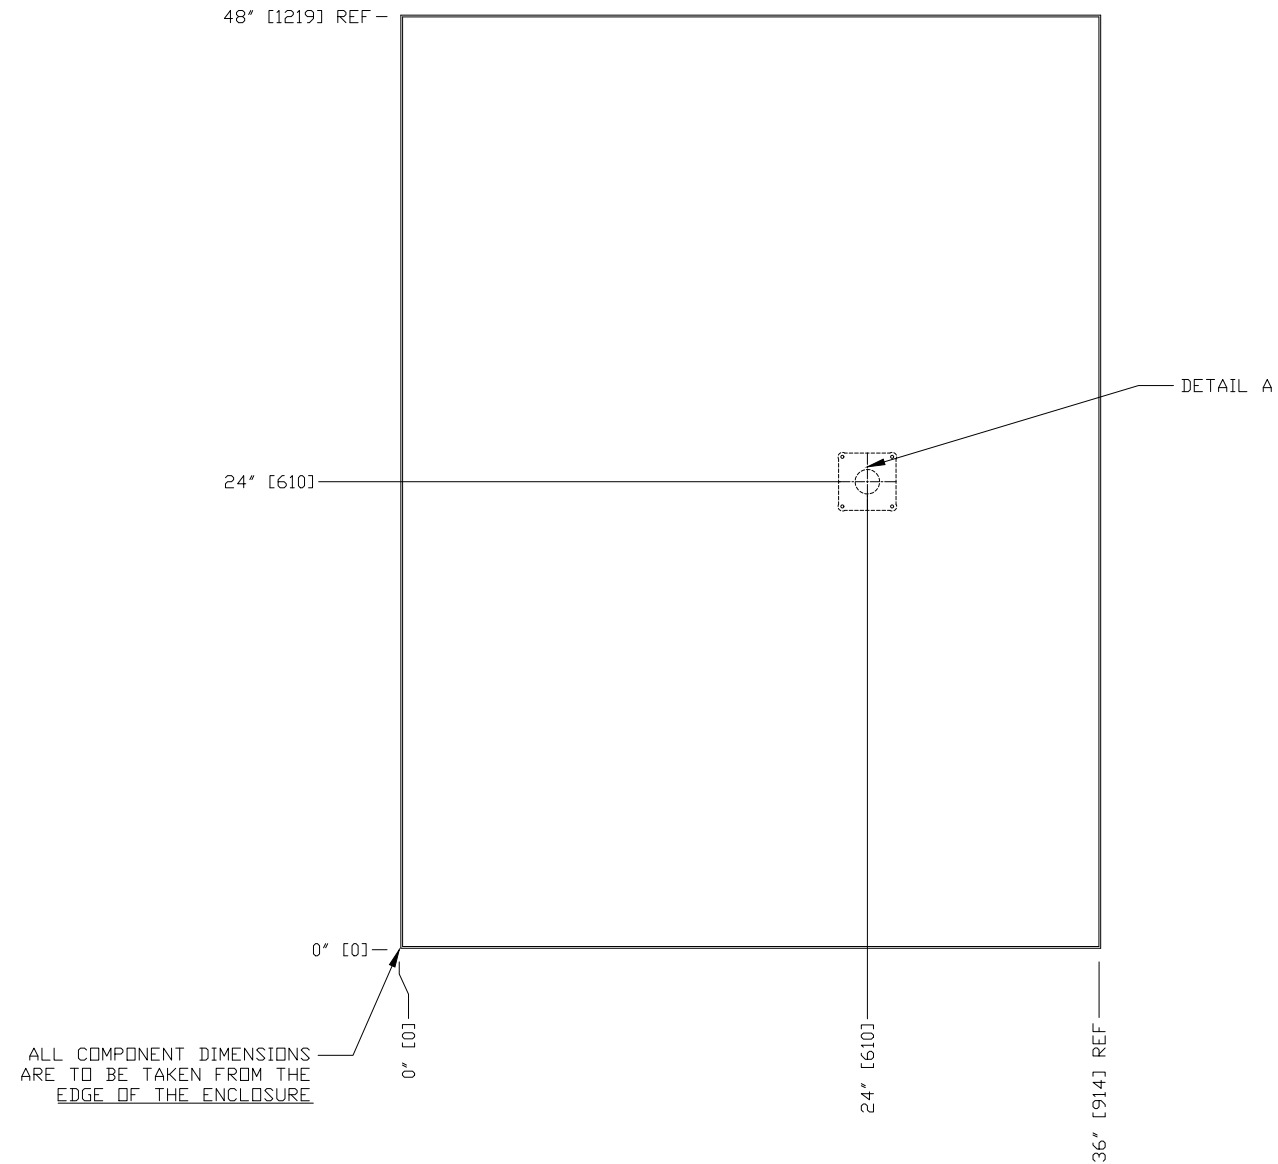

PANEL DETAIL

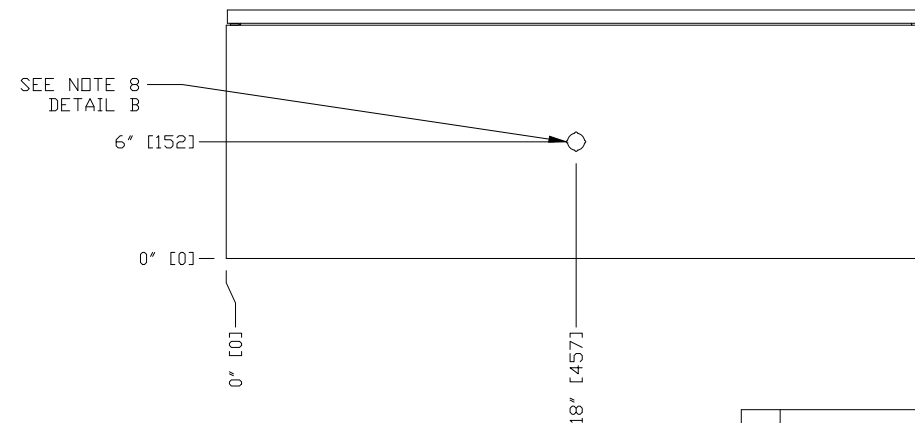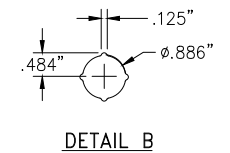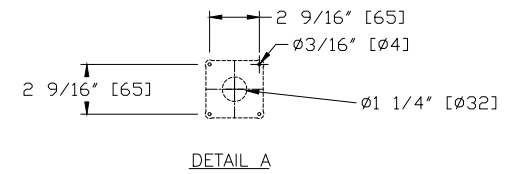

BOTTOM DETAIL

	Project No.: 22MH194		
	P.O. No.:	8027	Tag No.:
1	Approved Without Comments		
2	Approved With Comments; Revise and Resubmit		
3	Revise and Resubmit		
4	For Information Only		
5	Certified as Final Data		

<u>Ron Perego</u>	<u>9/4/24</u>
Project Manager	Date
<u>Bart Raytar</u>	<u>9/3/24</u>
Project Engineer	Date
<u>Mark Burton</u>	<u>8/21/24</u>
EH2 Representative	Date

--	--	

STD: Electrical v4.3	BAR = 1" AT PLOT SCALE
----------------------	--



	Project No.: 22MH194		
	P.O. No.:	8027	Tag No.:
1	Approved Without Comments		
2	Approved With Comments; Revise and Resubmit		
3	Revise and Resubmit		
4	For Information Only		
5	Certified as Final Data		

2	RE-issued FOR CONSTRUCTION, ADJ HEAT TRACED REVISED INCOMING POWER TO MAIN CIRCUIT BREAKER	2024-08-13	C.HANER	K.KALUNG	K.KALUNG	ECM128202	CMPANY CONFIDENTIAL INFORMATION THIS DOCUMENT AND ALL INFORMATION CONTAINED HEREIN, INCLUDING THE DESIGN CONCEPTS AND THOSE ARISING THEREFROM, ARE THE PROPERTY OF EVOQUA AND/OR ITS AFFILIATES AND ARE SUBMITTED IN CONFIDENCE. THEY MAY BE USED ONLY FOR THE EXPRESS PURPOSE FOR WHICH THEY ARE PROVIDED AND MUST NOT BE DISCLOSED, REPRODUCED, OR COPIED IN ANY FORM, INCLUDING IN ELECTRONIC FORM OR BY ANY MEANS, WITHOUT THE EXPRESS WRITTEN CONSENT OF EVOQUA. ALL INTENT AND CONTENT OF THIS DOCUMENT AND DERIVATIVE WORKS THEREOF ARE PROTECTED UNDER APPLICABLE COPYRIGHT LAWS. UPON RECEIPT OF EVOQUA, THIS DOCUMENT, ALONG WITH ALL COPIES AND EXTRACTS, AND ALL RELATED NOTES AND ANALYSES MUST BE RETURNED TO EVOQUA OR DESTROYED, AS INSTRUCTED BY EVOQUA. ACCEPTANCE OF THE DELIVERY OF THIS DOCUMENT CONSTITUTES AGREEMENT TO THESE TERMS.	DWN BY: C.HANER	DATE: 2023-11-17	TITLE: ENCLOSURE/BACKPANEL LAYOUT (CETLUS) CONTAINER POWER DISTRIBUTION PANEL PDP-0107	 EVOQUA WATER TECHNOLOGIES COLORADO SPRINGS CO USA +1-719-570-9690	PROJ/PROO NUMBER: 0304/001845 CODE: EC-DS083 FILE/DRAWING NUMBER: V112057481-08	SHEET 8 OF 10	REV 2
1	REVISE SCHEMATIC NOTE #3	2024-05-14	C.HANER	K.KALUNG	K.KALUNG	ECM127865		CKD BY: K.KALUNG DATE: 2023-11-17 APP'D BY: K.KALUNG DATE: 2023-11-17	CLIENT: ELECTRIC HYDROGEN BEAUMONT, TX					
0	ISSUED FOR CONSTRUCTION	2023-12-27	C.HANER	K.KALUNG	K.KALUNG	N/A		MDG BY: P.RYAN SCALE: NTS						
REV	DESCRIPTION	DATE	DWN	CKD	APPD	ECN	PART NUMBER: W3T602509	PROJ/PROO NUMBER: 0304/001845	CODE: EC-DS083	FILE/DRAWING NUMBER: V112057481-08	SHEET 8 OF 10	REV 2		

INTENTIONALLY LEFT BLANK

INTENTIONALLY LEFT BLANK

	Project No.: 22MH194		
	P.O. No.:	8027	Tag No.:
1 Approved Without Comments			
2 Approved With Comments; Revise and Resubmit			
3 Revise and Resubmit			
4 For Information Only			
5 Certified as Final Data			

<u>Ron Perego</u>	<u>9/4/24</u>
Project Manager	Date
<u>Bart Rajtar</u>	<u>9/3/24</u>
Project Engineer	Date
<u>Mark Burton</u>	<u>8/21/24</u>
EH2 Representative	Date

[illegible]

