

evoQUA
WATER TECHNOLOGIES

ELECTRIC HYDROGEN
BEAUMONT, TX
PROJECT NUMBER: 2034/001845

	Project No.: 22MH194		
	P.O. No.:	8027	Tag No.:
1	Approved Without Comments		
2	Approved With Comments; Revise and Resubmit		
3	Revise and Resubmit		
4	For Information Only		
5	Certified as Final Data		

Ron Perego6/17/24

Project ManagerDate

Bart Rajtar6/17/24

Project EngineerDate

EH2 Representative

Date

SHEET	PART NUMBER	FILENAME/DRAWING	DRAWING DESCRIPTION
1	W3T602508	V112057482-01	COVER SHEET
2	W3T602508	V112057482-02	ELECTRICAL SCHEMATIC NOTES
3	W3T602508	V112057482-03	POWER DISTRIBUTION
4	W3T602508	V112057482-04	ELECTRICAL ENCLOSURE NOTES & EXTERIOR DETAIL
5	W3T602508	V112057482-05	ELECTRICAL ENCLOSURE CUTOUT
6	W3T602508	V112057482-06	ELECTRICAL ENCLOSURE SUB PANEL LAYOUT
7	W3T602508	V112057482-07	ELECTRICAL TERMINAL LAYOUT
8	W3T602508	V112057482-08	ELECTRICAL NAME PLATE SCHEDULE

							COMPANY CONFIDENTIAL INFORMATION THIS DOCUMENT AND ALL INFORMATION CONTAINED HEREIN, INCLUDING THE DESIGN CONCEPTS AND THOSE ARISING THEREFROM, ARE THE PROPERTY OF EVOQUA AND/OR ITS AFFILIATES AND ARE SUBMITTED IN CONFIDENCE. THEY MAY BE USED ONLY FOR THE EXPRESS PURPOSE FOR WHICH THEY ARE PROVIDED AND MUST NOT BE DISCLOSED, REPRODUCED, OR COPIED IN ANY FORM, INCLUDING IN ELECTRONIC FORMAT, LOANED OR USED IN ANY OTHER MANNER WITHOUT THE EXPRESS WRITTEN CONSENT OF EVOQUA. ALL PATENT RIGHTS ARE RESERVED. THIS DOCUMENT AND DERIVATIVE WORKS THEREOF ARE PROTECTED UNDER APPLICABLE COPYRIGHT LAWS. UPON DEMAND OF EVOQUA, THIS DOCUMENT, ALONG WITH ALL COPIES AND EXTRACTS, AND ALL RELATED NOTES AND ANALYSES MUST BE RETURNED TO EVOQUA OR DESTROYED, AS INSTRUCTED BY EVOQUA. ACCEPTANCE OF THE DELIVERY OF THIS DOCUMENT CONSTITUTES AGREEMENT TO THESE TERMS.				DWN BY:	DATE	TITLE						
							M.KALIRA	2023-12-07	ENCLOSURE/BACKPANEL LAYOUT SODIUM BISULFITE DOSING PANEL JUNCTION BOX SKID 0200										
							CKD BY:	DATE											
							S.THANGA	2023-12-07	CLIENT										
							APPD BY:	DATE											
							K.KISITU	2023-12-07	ELECTRIC HYDROGEN BEAUMONT, TX										
1	REVISE SCHEMATIC NOTE #3	2024-05-14	C.HANER	K.KALUNG	K.KALUNG	ECM127665										EVOQUA WATER TECHNOLOGIES 1000 SPRINGS CO USA +1 719-570-9600			
0	ISSUED FOR CONSTRUCTION	2023-12-28	M.KALIRA	S.THANGA	K.KISITU	N/A													
REV	DESCRIPTION	DATE	DWN	CKD	APPD	ECN								PART NUMBER	PROJ/PROD NUMBER	CODE	FILE/DRAWING NUMBER	SHEET	REV
														W3T602508	2034/001845	EC-DOS03	V112057482-01	1 OF 8	1

0207/0208

8

7

6

5

4

3

2

1

ELECTRICAL SCHEMATIC NOTES

NOTES: UNLESS OTHERWISE SPECIFIED

1. ALL INTERNAL PANEL WIRING TO BE #14 AWG EXCEPT CLASS 2 CONTROL CIRCUITS AND PLC I/O TO BE #18 AWG.

2. DENOTES REMOTE PANELS OR COMPONENT(S).

3. ALL FIELD WIRING TO BE COPPER CONDUCTORS SIZED AT MIN 60°C.

4. --s--s-- DENOTES SKID WIRING BY FACTORY.

5. ----- DENOTES FIELD WIRING TO EXTERNAL COMPONENTS (BY OTHERS).

6. WIRE COLORS:

BLK120/230V AND ABOVE POWER

RED120/230V CONTROL

WHTNEUTRAL

BLUDC POSITIVE

BLU/WHTDC UNGROUNDED COMMON

WHT/BLUDC GROUNDED COMMON

ORGEXTERNALLY POWERED OR UNGROUNDED CONDUCTORS REMAINING ENERGIZED WHEN MAIN SUPPLY CIRCUIT DISCONNECT IS IN OFF POSITION

WHT/ORG GROUNDED AC CIRCUIT CONDUCTOR REMAINING ENERGIZED WHEN MAIN SUPPLY CIRCUIT DISCONNECT IS IN OFF POSITION

GRN/YELGROUNDING

7. ALL SKID WIRING TO BE #14 AWG THHN MINIMUM, EXCEPT FOR MULTI-CONDUCTOR CABLES WITH OVERALL JACKET.

8. SHIELDED SIGNAL CABLE FOR CLASS 1 CONTROL CIRCUITS TO BE 600V BELDEN 1120A OR EQUIVALENT.

9. SHIELDED SIGNAL CABLE FOR CLASS 2 CONTROL CIRCUITS TO BE 300V BELDEN 8760 OR EQUIVALENT.

10. -c--c--DENOTES CONTAINER WIRING BY FACTORY.

STD Electrical v4.3

BAR = 1" AT PLOT SCALE

0207/0208

							COMPANY CONFIDENTIAL INFORMATION THIS DOCUMENT AND ALL INFORMATION CONTAINED HEREIN, INCLUDING THE DESIGN CONCEPTS AND THOSE ARISING THEREFROM, ARE THE PROPERTY OF EVOQUA AND/OR ITS AFFILIATES AND ARE SUBMITTED IN CONFERENCE. THEY MAY BE USED ONLY FOR THE EXPRESS PURPOSE FOR WHICH THEY ARE PROVIDED AND MUST NOT BE DISCLOSED, REPRODUCED, OR COPIED IN ANY FORM, INCLUDING IN ELECTRONIC FORMAT, LOANED OR USED IN ANY OTHER MANNER WITHOUT THE EXPRESS WRITTEN CONSENT OF EVOQUA. ALL PATENT RIGHTS ARE RESERVED. THIS DOCUMENT AND DERIVATIVE WORKS THEREOF ARE PROTECTED UNDER APPLICABLE COPYRIGHT LAWS. UPON DEMAND OF EVOQUA, THIS DOCUMENT, ALONG WITH ALL COPIES AND EXTRACTS, AND ALL RELATED NOTES AND ANALYSES MUST BE RETURNED TO EVOQUA OR DESTROYED, AS INSTRUCTED BY EVOQUA. ACCEPTANCE OF THE DELIVERY OF THIS DOCUMENT CONSTITUTES AGREEMENT TO THESE TERMS.	DWN BY: M.KALIRA	DATE 2023-12-07	TITLE ENCLOSURE/BACKPANEL LAYOUT SODIUM BISULFITE DOSING PANEL JUNCTION BOX SKID 0200			
								CKD BY: S.THANGA	DATE 2023-12-07	CLIENT ELECTRIC HYDROGEN BEAUMONT, TX			
								APPD BY: K.KISITU	DATE 2023-12-07				
								MGD BY: P.RYAN	SCALE NTS				
1	REVISE SCHEMATIC NOTE #3	2024-05-14	C.HANER	K.KALUNG	K.KALUNG	ECM127665		PART NUMBER W3T602508	PROJ/PROD NUMBER 2034/001845	CODE EC-DOS03	FILE/DRAWING NUMBER V112057482-02	SHEET 2 OF 8	REV 1
0	ISSUED FOR CONSTRUCTION	2023-12-28	M.KALIRA	S.THANGA	K.KISITU	N/A							
REV	DESCRIPTION	DATE	DWN	CKD	APPD	ECN							

8 7 6 5 4 3 2 1

300

301

302

303

304

305

306

307

308

309

310

311

312

313

314

315

316

317

318

319

320

321

322

323

324

325

326

327

328

329

330

331

332

333

334

335

336

337

338

339

340

341

342

343

344

345

346

347

348

349

350

351

352

353

354

355

356

357

358

359

360

361

362

363

364

365

366

367

368

369

370

371

372

373

374

375

376





377

378

379

STD Electrical v4.3

BAR = 1" AT PLOT SCALE

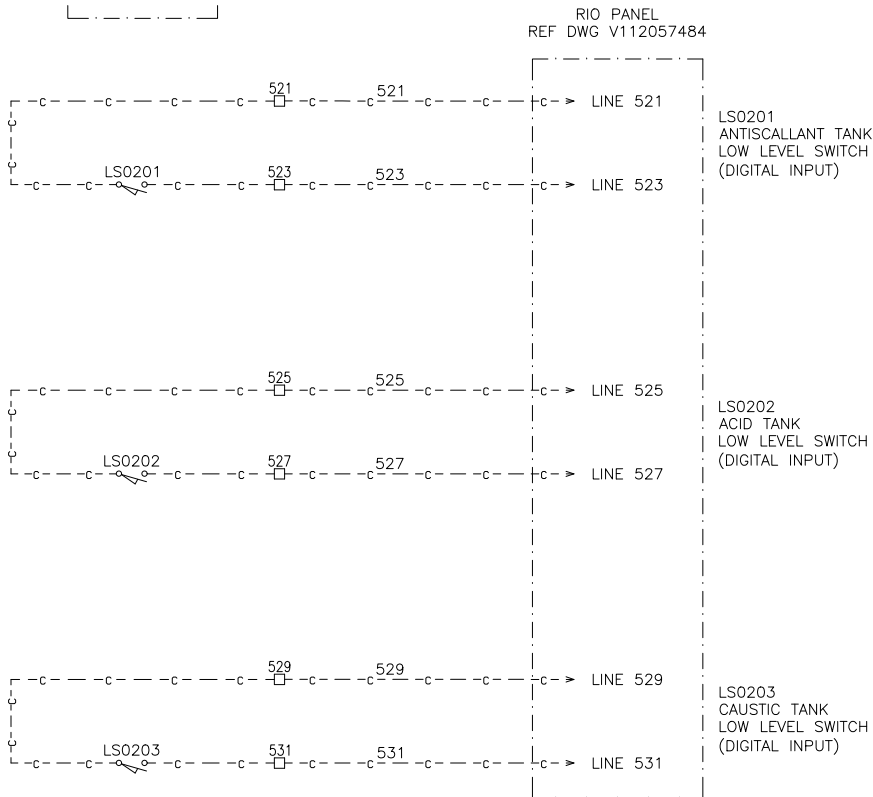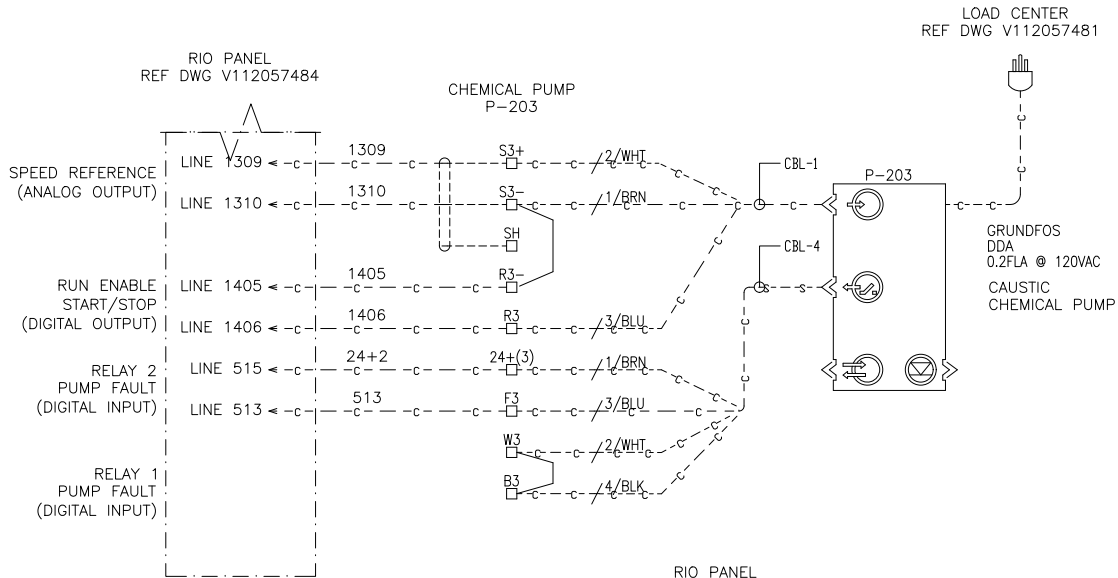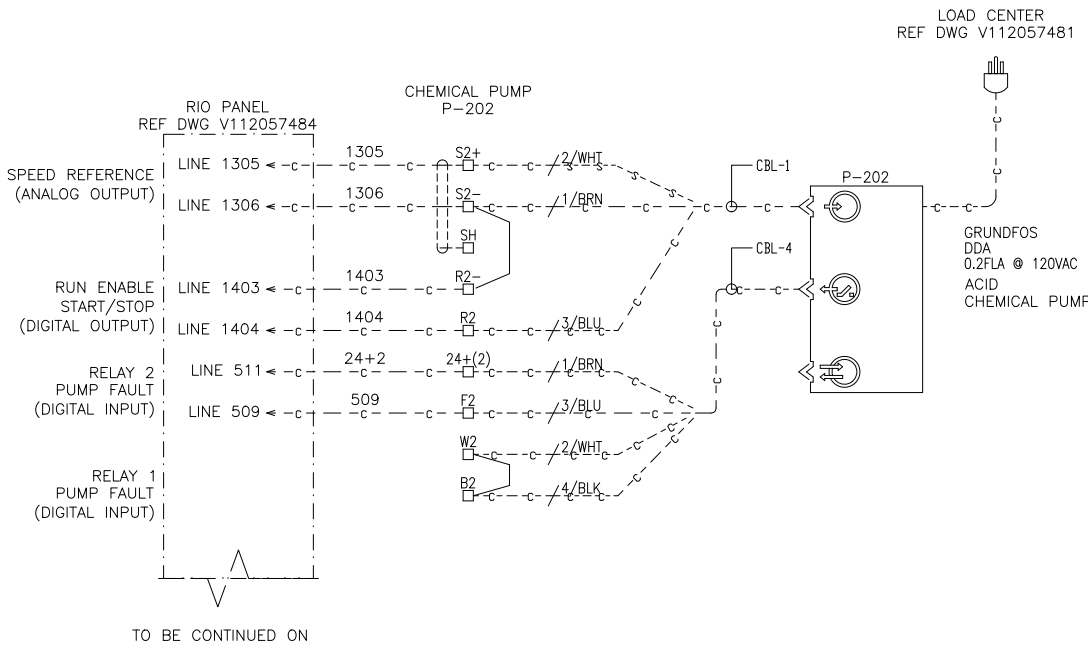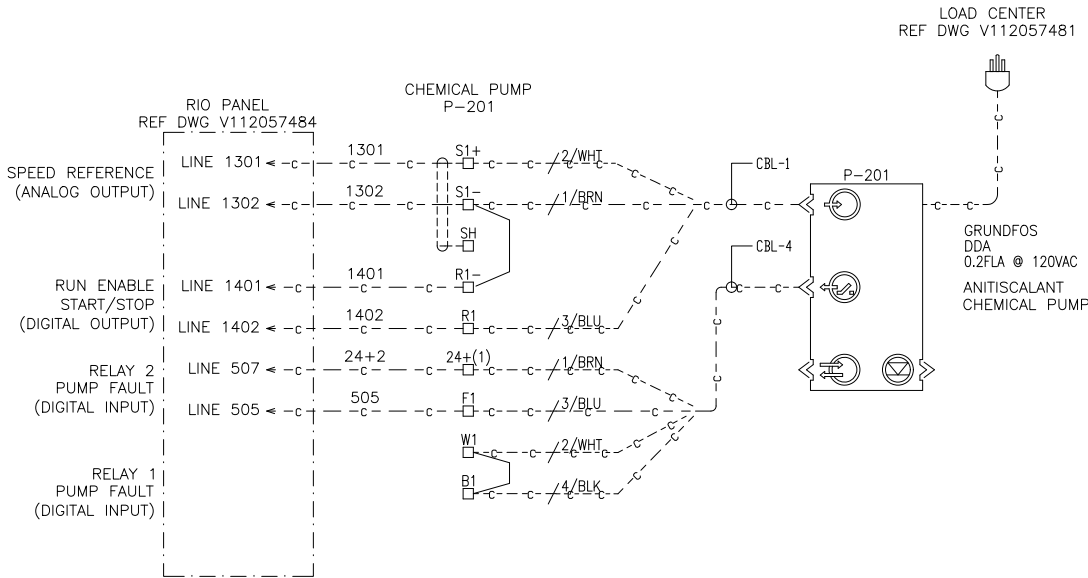

COMPANY CONFIDENTIAL INFORMATION THIS DOCUMENT AND ALL INFORMATION CONTAINED HEREIN, INCLUDING THE DESIGN CONCEPTS AND THOSE ARISING THEREFROM, ARE THE PROPERTY OF EVOQUA AND/OR ITS AFFILIATES AND ARE SUBMITTED IN CONFERENCE. THEY MAY BE USED ONLY FOR THE EXPRESS PURPOSE FOR WHICH THEY ARE PROVIDED AND MUST NOT BE DISCLOSED, REPRODUCED, OR COPIED IN ANY FORM, INCLUDING IN ELECTRONIC FORMAT, LOANED OR USED IN ANY OTHER MANNER WITHOUT THE EXPRESS WRITTEN CONSENT OF EVOQUA. ALL PATENT RIGHTS ARE RESERVED. THIS DOCUMENT AND DERIVATIVE WORKS THEREOF ARE PROTECTED UNDER APPLICABLE COPYRIGHT LAWS. UPON DEMAND OF EVOQUA, THIS DOCUMENT, ALONG WITH ALL COPIES AND EXTRACTS, AND ALL RELATED NOTES AND ANALYSES MUST BE RETURNED TO EVOQUA OR DESTROYED, AS INSTRUCTED BY EVOQUA. ACCEPTANCE OF THE DELIVERY OF THIS DOCUMENT CONSTITUTES AGREEMENT TO THESE TERMS.							DWN BY: M.KALIRA DATE: 2023-12-07 CKD BY: S.THANGA DATE: 2023-12-07 APPD BY: K.KISITU DATE: 2023-12-07 MGD BY: P.RYAN SCALE: NTS	TITLE: ENCLOSURE/BACKPANEL LAYOUT SODIUM BISULFITE DOSING PANEL JUNCTION BOX SKID 0200 CLIENT: ELECTRIC HYDROGEN BEAUMONT, TX
1	REVISE SCHEMATIC NOTE #3	2024-05-14	C.HANER	K.KALUNG	K.KALUNG	ECM127665	 EVOQUA WATER TECHNOLOGIES COLORADO SPRINGS CO USA +1 719-570-9600	PART NUMBER: 2034/001845 CODE: EC-DOS03 FILE/DRAWING NUMBER: V112057482-03 SHEET: 3 OF 8 REV: 1
0	ISSUED FOR CONSTRUCTION	2023-12-28	M.KALIRA	S.THANGA	K.KISITU	N/A		
REV	DESCRIPTION	DATE	DWN	CKD	APPD	ECN		

NOTES : UNLESS OTHERWISE SPECIFIED

1.

THIS PANEL TO BE MOUNTED ON THE EXTERIOR OF SODIUM BISULFITE DOSING PANEL, SKID 0200
2.


THIS ENCLOSURE IS TO BE TYPE NEMA 4X FRP.
3.

MANUFACTURING TO LAYOUT BACKPANEL AS SHOWN.
4.


MANUFACTURING TO VERIFY ALL DIMENSIONS AND CUTOUT SIZES BEFORE CUTTING OR DRILLING PANEL.
5.

WIREWAY TO BE 3” DEEP.
6.


DIN RAIL TO BE MOUNTED ON 1” STANDOFFS.

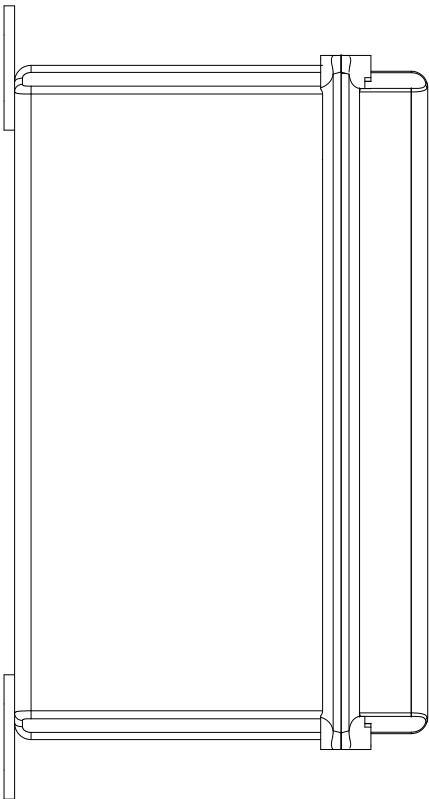

LEFT SIDE DETAIL

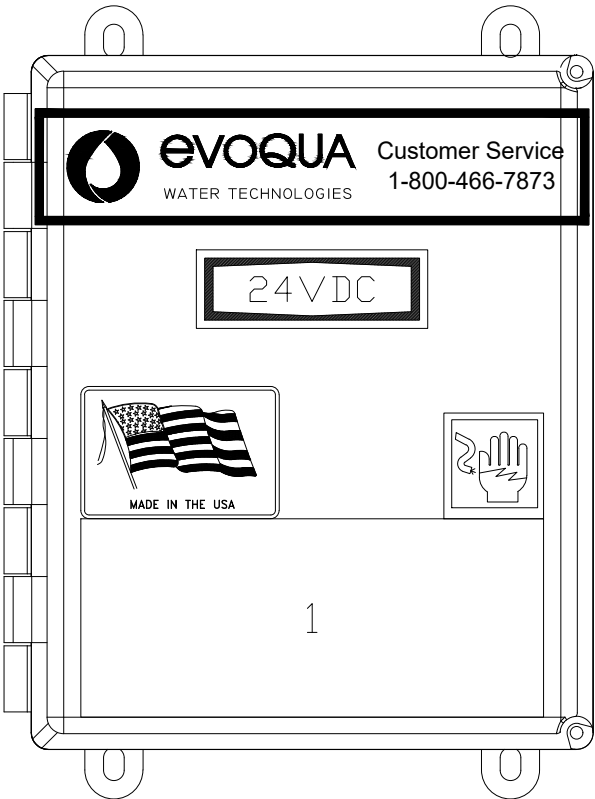


PANEL DETAIL
10” x 8” x 6”
[254MM x 203MM x 152MM]

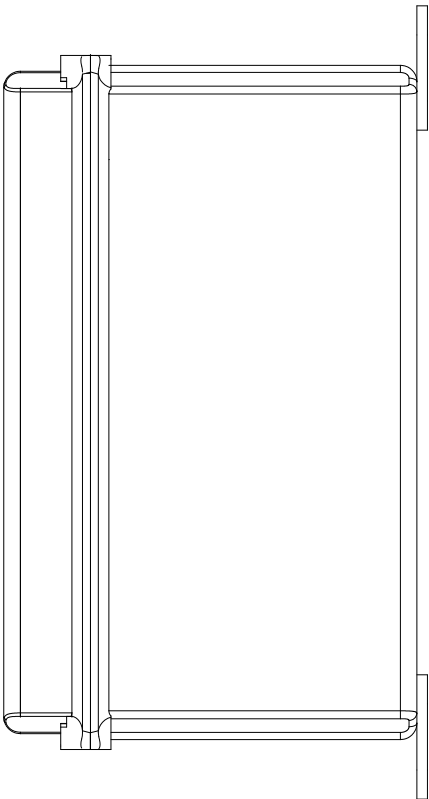


RIGHT SIDE DETAIL

							COMPANY CONFIDENTIAL INFORMATION THIS DOCUMENT AND ALL INFORMATION CONTAINED HEREIN, INCLUDING THE DESIGN CONCEPTS AND THOSE ARISING THEREFROM, ARE THE PROPERTY OF EVOQUA AND/OR ITS AFFILIATES AND ARE SUBMITTED IN CONFERENCE. THEY MAY BE USED ONLY FOR THE EXPRESS PURPOSE FOR WHICH THEY ARE PROVIDED AND MUST NOT BE DISCLOSED, REPRODUCED, OR COPIED IN ANY FORM, INCLUDING IN ELECTRONIC FORMAT, LOANED OR USED IN ANY OTHER MANNER WITHOUT THE EXPRESS WRITTEN CONSENT OF EVOQUA. ALL PATENT RIGHTS ARE RESERVED. THIS DOCUMENT AND DERIVATIVE WORKS THEREOF ARE PROTECTED UNDER APPLICABLE COPYRIGHT LAWS. UPON DEMAND OF EVOQUA, THIS DOCUMENT, ALONG WITH ALL COPIES AND EXTRACTS, AND ALL RELATED NOTES AND ANALYSES MUST BE RETURNED TO EVOQUA OR DESTROYED, AS INSTRUCTED BY EVOQUA. ACCEPTANCE OF THE DELIVERY OF THIS DOCUMENT CONSTITUTES AGREEMENT TO THESE TERMS.	DWN BY: M.KALIRA	DATE: 2023-12-07	TITLE ENCLOSURE/BACKPANEL LAYOUT SODIUM BISULFITE DOSING PANEL JUNCTION BOX SKID 0200
								CKD BY: S.THANGA	DATE: 2023-12-07	CLIENT ELECTRIC HYDROGEN BEAUMONT, TX
								APPD BY: K.KISITU	DATE: 2023-12-07	
								MGD BY: P.RYAN	SCALE: NTS	
1	REVISE SCHEMATIC NOTE #3	2024-05-14	C.HANER	K.KALUNG	K.KALUNG	ECM127665				
0	ISSUED FOR CONSTRUCTION	2023-12-28	M.KALIRA	S.THANGA	K.KISITU	N/A				
REV	DESCRIPTION	DATE	DWN	CKD	APPD	ECN		PART NUMBER W3T602508	PROJ/PROD NUMBER 2034/001845	CODE EC-DOS03
									FILE/DRAWING NUMBER V112057482-04	SHEET 4 OF 8
										REV 1


NOTES: SEE SHEET ONE

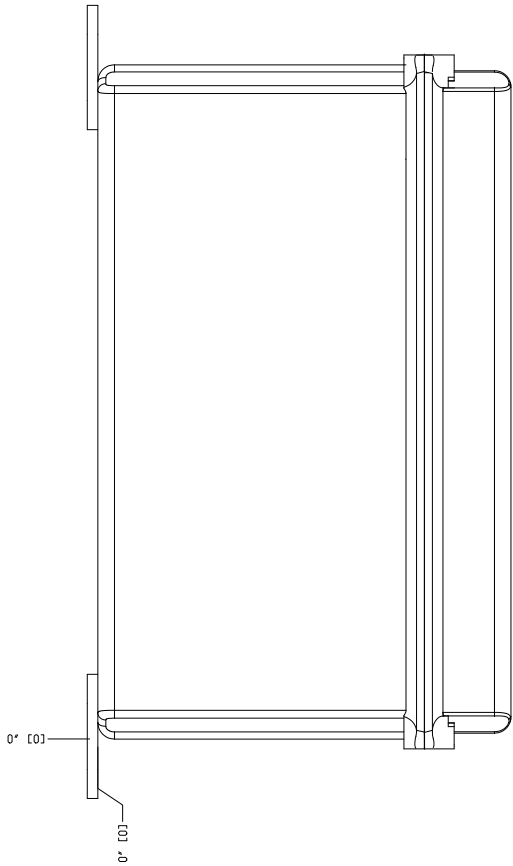

LEFT SIDE DETAIL

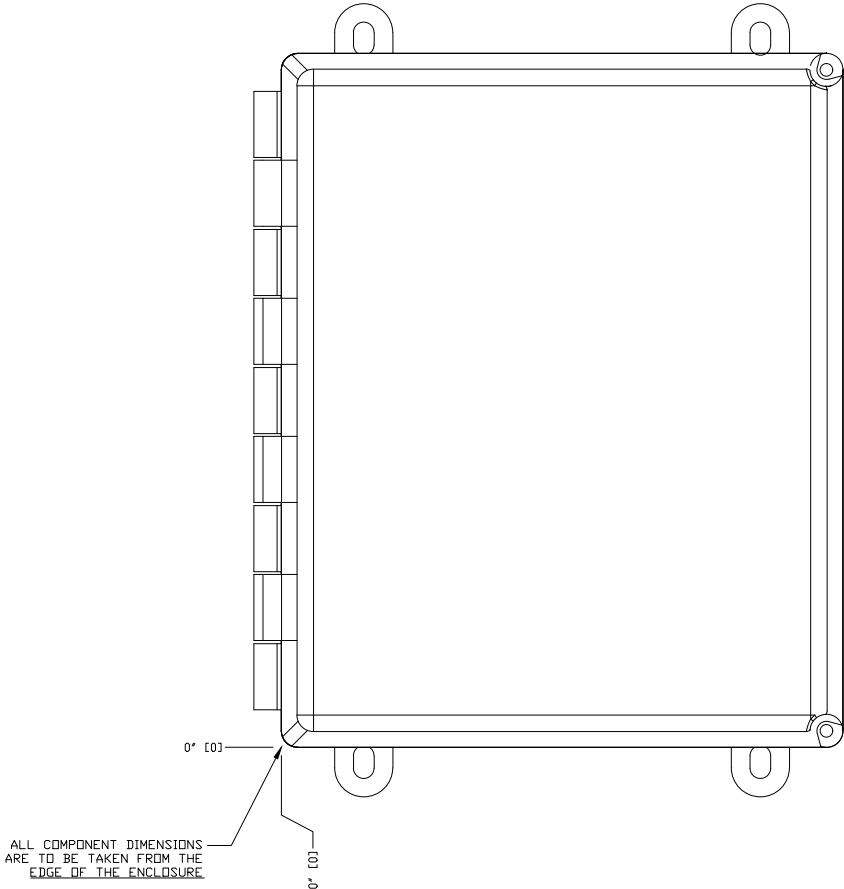


PANEL DETAIL

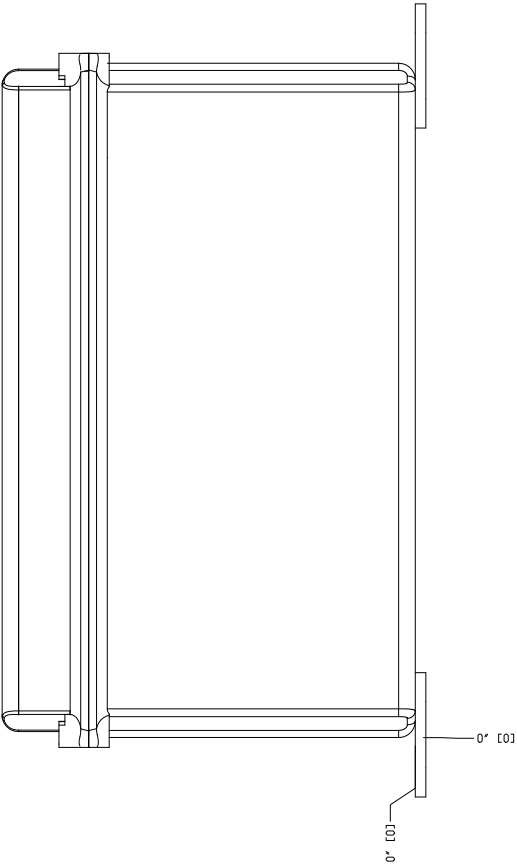

RIGHT SIDE DETAIL

MANUFACTURING TO VERIFY LOCATION AND ALL DIMENSIONS AND CUTOUT SIZES BEFORE CUTTING OR DRILLING PANEL.

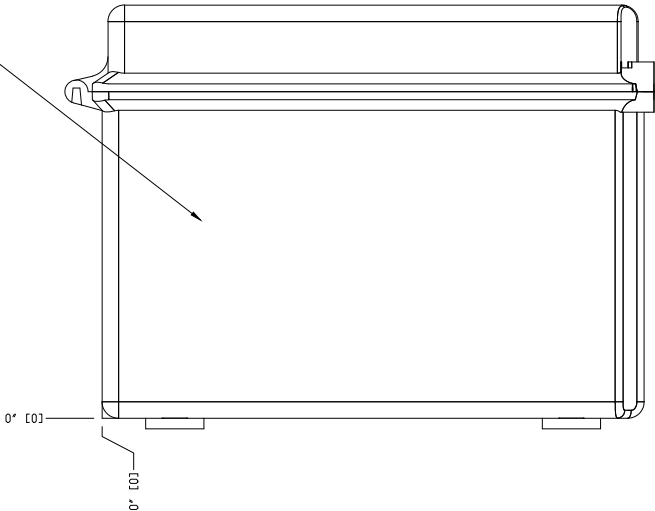


BOTTOM DETAIL

STD Electrical v4.3

BAR = 1" AT PLOT SCALE


							COMPANY CONFIDENTIAL INFORMATION THIS DOCUMENT AND ALL INFORMATION CONTAINED HEREIN, INCLUDING THE DESIGN CONCEPTS AND THOSE ARISING THEREFROM, ARE THE PROPERTY OF EVOQUA AND/OR ITS AFFILIATES AND ARE SUBMITTED IN CONFERENCE. THEY MAY BE USED ONLY FOR THE EXPRESS PURPOSE FOR WHICH THEY ARE PROVIDED AND MUST NOT BE DISCLOSED, REPRODUCED, OR COPIED IN ANY FORM, INCLUDING IN ELECTRONIC FORMAT, LOANED OR USED IN ANY OTHER MANNER WITHOUT THE EXPRESS WRITTEN CONSENT OF EVOQUA. ALL PATENT RIGHTS ARE RESERVED. THIS DOCUMENT AND DERIVATIVE WORKS THEREOF ARE PROTECTED UNDER APPLICABLE COPYRIGHT LAWS. UPON DEMAND OF EVOQUA, THIS DOCUMENT, ALONG WITH ALL COPIES AND EXTRACTS, AND ALL RELATED NOTES AND ANALYSES MUST BE RETURNED TO EVOQUA OR DESTROYED, AS INSTRUCTED BY EVOQUA. ACCEPTANCE OF THE DELIVERY OF THIS DOCUMENT CONSTITUTES AGREEMENT TO THESE TERMS.			DWN BY: M.KALIRA	DATE: 2023-12-07	TITLE: ENCLOSURE/BACKPANEL LAYOUT SODIUM BISULFITE DOSING PANEL JUNCTION BOX SKID 0200
							CKD BY: S.THANGA	DATE: 2023-12-07	CLIENT: ELECTRIC HYDROGEN BEAUMONT, TX			
							APPD BY: K.KISITU	DATE: 2023-12-07				
							MGD BY: P.RYAN	SCALE: NTS	 EVOQUA WATER TECHNOLOGIES COLORADO SPRINGS CO USA +1 719-570-9600			
1	REVISE SCHEMATIC NOTE #3	2024-05-14	C.HANER	K.KALUNG	K.KALUNG	ECM127665						
0	ISSUED FOR CONSTRUCTION	2023-12-28	M.KALIRA	S.THANGA	K.KISITU	N/A						
REV	DESCRIPTION	DATE	DWN	CKD	APPD	ECN	PART NUMBER W3T602508	PROJ/PROD NUMBER 2034/001845	CODE EC-DOS03	FILE/DRAWING NUMBER V112057482-05	SHEET 5 OF 8	REV 1

0207/0208

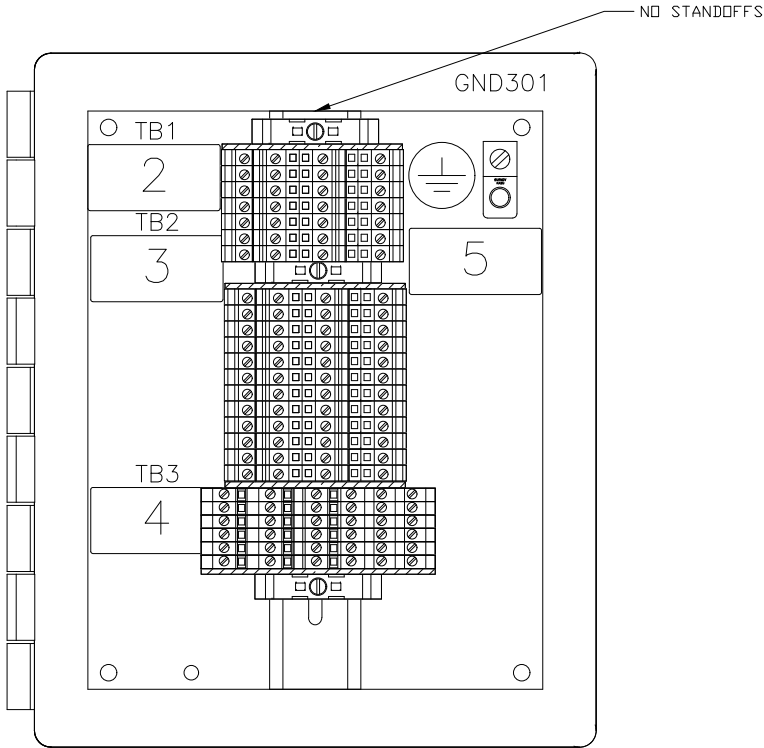

10" x 8" x 6"

BACKPANEL LAYOUT

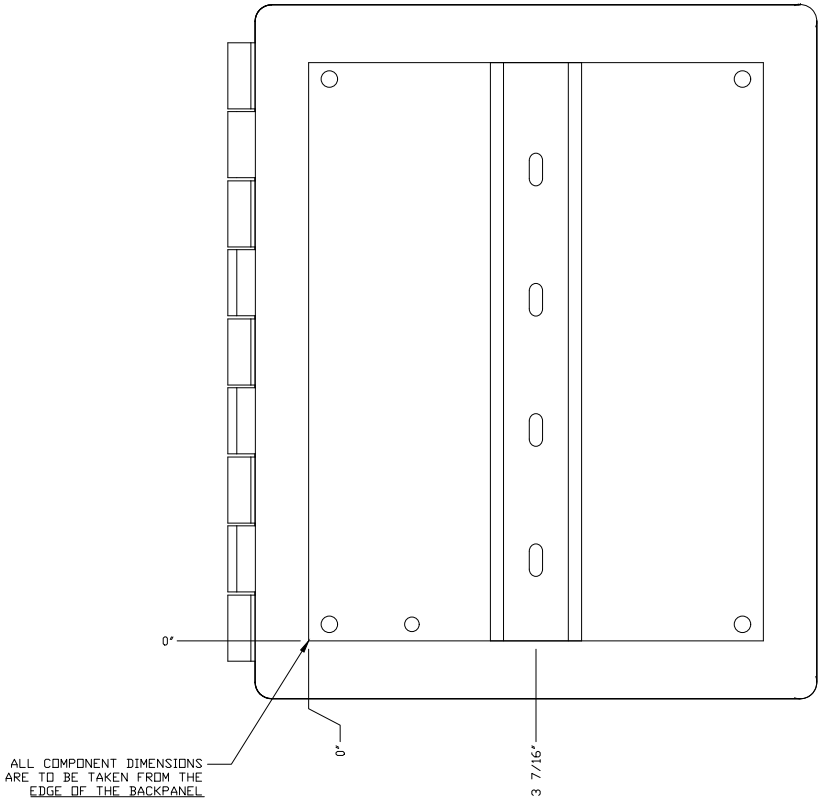

BACKPANEL DETAIL

							COMPANY CONFIDENTIAL INFORMATION THIS DOCUMENT AND ALL INFORMATION CONTAINED HEREIN, INCLUDING THE DESIGN CONCEPTS AND THOSE ARISING THEREFROM, ARE THE PROPERTY OF EVOQUA AND/OR ITS AFFILIATES AND ARE SUBMITTED IN CONFERENCE. THEY MAY BE USED ONLY FOR THE EXPRESS PURPOSE FOR WHICH THEY ARE PROVIDED AND MUST NOT BE DISCLOSED, REPRODUCED, OR COPIED IN ANY FORM, INCLUDING IN ELECTRONIC FORMAT, LOANED OR USED IN ANY OTHER MANNER WITHOUT THE EXPRESS WRITTEN CONSENT OF EVOQUA. ALL PATENT RIGHTS ARE RESERVED. THIS DOCUMENT AND DERIVATIVE WORKS THEREOF ARE PROTECTED UNDER APPLICABLE COPYRIGHT LAWS. UPON DEMAND OF EVOQUA, THIS DOCUMENT, ALONG WITH ALL COPIES AND EXTRACTS, AND ALL RELATED NOTES AND ANALYSES MUST BE RETURNED TO EVOQUA OR DESTROYED, AS INSTRUCTED BY EVOQUA. ACCEPTANCE OF THE DELIVERY OF THIS DOCUMENT CONSTITUTES AGREEMENT TO THESE TERMS.			DWN BY: M.KALIRA	DATE: 2023-12-07	TITLE: ENCLOSURE/BACKPANEL LAYOUT SODIUM BISULFITE DOSING PANEL JUNCTION BOX SKID 0200		
							CKD BY: S.THANGA	DATE: 2023-12-07	CLIENT:	ELECTRIC HYDROGEN BEAUMONT, TX				
							APPD BY: K.KISITU	DATE: 2023-12-07	 evoqua WATER TECHNOLOGIES					
1	REVISE SCHEMATIC NOTE #3	2024-05-14	C.HANER	K.KALUNG	K.KALUNG	ECM127665	MGD BY: P.RYAN	SCALE: NTS						
0	ISSUED FOR CONSTRUCTION	2023-12-28	M.KALIRA	S.THANGA	K.KISITU	N/A								
REV	DESCRIPTION	DATE	DWN	CKD	APPD	ECN	PART NUMBER W3T602508	PROJ/PROD NUMBER 2034/001845	CODE EC-DOS03	FILE/DRAWING NUMBER V112057482-06	SHEET 6 OF 8	REV 1		

[illegible]

