



ELECTRIC HYDROGEN
BEAUMONT, TX
PROJECT NUMBER: 2034/001845

EVOQUA MUST IDENTIFY HOW TO GET SHIPPED LOOSE LIT-501 WIRING INTO THE CONEX CONTAINER. HIGHLY ENCOURAGE A NEW JUNCTION BE ADDED OVER THE TOP OF THE POWER DISTRIBUTION PANEL (PDP) FOR LIT-501 AND CUSTOMER CONTROLS INTERFACE CONNECTIONS (4PR #16 & TWO ETHERNET CABLES).

	Project No.: 22MH194		
	P.O. No.:	8027	Tag No.:
1	Approved Without Comments		
2	Approved With Comments; Revise and Resubmit		
3	Revise and Resubmit		
4	For Information Only		
5	Certified as Final Data		

Ron Perego

Project Manager

6/17/24

Date

Bart Rajtar

Project Engineer

6/17/24

Date

EH2 Representative

Date

SHEET	PART NUMBER	FILENAME/DRAWING	DRAWING DESCRIPTION
1	W3T602507	V112057483-01	COVER SHEET
2	W3T602507	V112057483-02	ELECTRICAL SCHEMATIC NOTES
3	W3T602507	V112057483-03	POWER DISTRIBUTION - 480VAC
4	W3T602507	V112057483-04	POWER DISTRIBUTION - 480VAC
5	W3T602507	V112057483-05	POWER DISTRIBUTION - 120VAC
6	W3T602507	V112057483-06	POWER DISTRIBUTION - 120VAC
7	W3T602507	V112057483-07	POWER DISTRIBUTION - 120VAC
8	W3T602507	V112057483-08	PLC COMMUNICATION
9	W3T602507	V112057483-09	PLC I/O - DISCRETE INPUT
10	W3T602507	V112057483-10	PLC I/O - ANALOG INPUT
11	W3T602507	V112057483-11	PLC I/O - ANALOG INPUT
12	W3T602507	V112057483-12	PLC I/O - ANALOG INPUT/DIGITAL INPUT
13	W3T602507	V112057483-13	PLC I/O - FPD/DIGITAL OUTPUT
14	W3T602507	V112057483-14	PLC I/O - ANALOG INPUT/DIGITAL OUTPUT
15	W3T602507	V112057483-15	CONTROL RELAY CONNECTION
16	W3T602507	V112057483-16	INTENTIONALLY LEFT BLANK
17	W3T602507	V112057483-17	ELECTRICAL ENCLOSURE LAYOUT
18	W3T602507	V112057483-18	ELECTRICAL ENCLOSURE CUTOUT
19	W3T602507	V112057483-19	ELECTRICAL SUBPANEL LAYOUT
20	W3T602507	V112057483-20	ELECTRICAL TERMINAL LAYOUT
21	W3T602507	V112057483-21	ELECTRICAL NAME PLATE SCHEDULE

						COMPANY CONFIDENTIAL INFORMATION THIS DOCUMENT AND ALL INFORMATION CONTAINED HEREIN, INCLUDING THE DESIGN CONCEPTS AND THOSE ARISING THEREFROM, ARE THE PROPERTY OF EVOQUA AND/OR ITS AFFILIATES AND ARE SUBMITTED IN CONFIDENCE. THEY MAY BE USED ONLY FOR THE EXPRESS PURPOSE FOR WHICH THEY ARE PROVIDED AND MUST NOT BE DISCLOSED, REPRODUCED, OR COPIED IN ANY FORM, INCLUDING IN ELECTRONIC FORMAT, LOANED OR USED IN ANY OTHER MANNER WITHOUT THE EXPRESS WRITTEN CONSENT OF EVOQUA. ALL PATENT RIGHTS ARE RESERVED. THIS DOCUMENT AND DERIVATIVE WORKS THEREOF ARE PROTECTED UNDER APPLICABLE COPYRIGHT LAWS. UPON DEMAND OF EVOQUA, THIS DOCUMENT, ALONG WITH ALL COPIES AND EXTRACTS, AND ALL RELATED NOTES AND ANALYSES MUST BE RETURNED TO EVOQUA OR DESTROYED, AS INSTRUCTED BY EVOQUA, ACCEPTANCE OF THE DELIVERY OF THIS DOCUMENT CONSTITUTES AGREEMENT TO THESE TERMS.				DWN BY:	DATE	TITLE			
						M.KALIRA	2023-11-28	ELECTRICAL SCHEMATICS & ENCLOSURE DIAGRAMS (cETLus) CONTAINERIZED 2-PASS RO WITH PRETREATMENT RO PANEL - SKID 0300							
						CKD BY:	DATE								
						S.THANGA	2023-11-28	CLIENT	ELECTRIC HYDROGEN BEAUMONT, TX						
						APPD BY:	DATE								
						K.KISITU	2023-11-28								
						MGD BY:	SCALE								
						P.RYAN	NTS								
								EVOQUA WATER TECHNOLOGIES 1000 SPRINGS CO USA +1 719-570-9600							
						PART NUMBER	PROJ/PROD NUMBER	CODE	FILE/DRAWING NUMBER	SHEET	REV				
						W3T602507	2034/001845	EC-DOS03	V112057483-01	1 OF 21	1				

8

7

6

5

4

3

2

1

ELECTRICAL SCHEMATIC NOTES

NOTES: UNLESS OTHERWISE SPECIFIED

1. ALL INTERNAL PANEL WIRING TO BE #14 AWG EXCEPT CLASS 2 CONTROL CIRCUITS AND PLC I/O TO BE #18 AWG.

2. DENOTES REMOTE PANELS OR COMPONENT(S).

3. ALL FIELD WIRING TO BE COPPER CONDUCTORS SIZED AT MIN 60°C.

4. --s--s-- DENOTES SKID WIRING BY FACTORY.

5. ----- DENOTES FIELD WIRING TO EXTERNAL COMPONENTS (BY OTHERS).

6. WIRE COLORS:

BLK120/230V AND ABOVE POWER

RED120/230V CONTROL

WHTNEUTRAL

BLUDC POSITIVE

BLU/WHTDC UNGROUNDED COMMON

WHT/BLUDC GROUNDED COMMON

ORGEXTERNALLY POWERED OR UNGROUNDED CONDUCTORS REMAINING ENERGIZED WHEN MAIN SUPPLY CIRCUIT DISCONNECT IS IN OFF POSITION

WHT/ORG GROUNDED AC CIRCUIT CONDUCTOR REMAINING ENERGIZED WHEN MAIN SUPPLY CIRCUIT DISCONNECT IS IN OFF POSITION

GRN/YELGROUNDING

7. ALL SKID WIRING TO BE #14 AWG THHN MINIMUM, EXCEPT FOR MULTI-CONDUCTOR CABLES WITH OVERALL JACKET.

8. SHIELDED SIGNAL CABLE FOR CLASS 1 CONTROL CIRCUITS TO BE 600V BELDEN 1120A OR EQUIVALENT.

9. SHIELDED SIGNAL CABLE FOR CLASS 2 CONTROL CIRCUITS TO BE 300V BELDEN 8760 OR EQUIVALENT.




10. -c--c--DENOTES CONTAINER WIRING BY FACTORY.

STD Electrical v4.3


BAR = 1" AT PLOT SCALE


0307/0308

							COMPANY CONFIDENTIAL INFORMATION THIS DOCUMENT AND ALL INFORMATION CONTAINED HEREIN, INCLUDING THE DESIGN CONCEPTS AND THOSE ARISING THEREFROM, ARE THE PROPERTY OF EVOQUA AND/OR ITS AFFILIATES AND ARE SUBMITTED IN CONFERENCE. THEY MAY BE USED ONLY FOR THE EXPRESS PURPOSE FOR WHICH THEY ARE PROVIDED AND MUST NOT BE DISCLOSED, REPRODUCED, OR COPIED IN ANY FORM, INCLUDING IN ELECTRONIC FORMAT, LOANED OR USED IN ANY OTHER MANNER WITHOUT THE EXPRESS WRITTEN CONSENT OF EVOQUA. ALL PATENT RIGHTS ARE RESERVED. THIS DOCUMENT AND DERIVATIVE WORKS THEREOF ARE PROTECTED UNDER APPLICABLE COPYRIGHT LAWS. UPON DEMAND OF EVOQUA, THIS DOCUMENT, ALONG WITH ALL COPIES AND EXTRACTS, AND ALL RELATED NOTES AND ANALYSES MUST BE RETURNED TO EVOQUA OR DESTROYED, AS INSTRUCTED BY EVOQUA. ACCEPTANCE OF THE DELIVERY OF THIS DOCUMENT CONSTITUTES AGREEMENT TO THESE TERMS.	DWN BY: M.KALIRA	DATE 2023-11-28	TITLE ELECTRICAL SCHEMATICS & ENCLOSURE DIAGRAMS (cETLus) CONTAINERIZED 2-PASS RO WITH PRETREATMENT RO PANEL - SKID 0300			
								CKD BY: S.THANGA	DATE 2023-11-28	CLIENT ELECTRIC HYDROGEN BEAUMONT, TX			
								APPD BY: K.KISITU	DATE 2023-11-28				
								MGD BY: P.RYAN	SCALE NTS				
1	REVISE SCHEMATIC NOTE #3 & ETHERNET SWITCH CHANGE	2024-05-14	C.HANER	K.KALUNG	K.KALUNG	ECM127665		PART NUMBER W3T602507	PROJ/PROD NUMBER 2034/001845	CODE EC-DOS03	FILE/DRAWING NUMBER V112057483-02	SHEET 2 OF 21	REV 1
0	ISSUED FOR CONSTRUCTION	2023-12-28	M.KALIRA	S.THANGA	K.KISITU	N/A							
REV	DESCRIPTION	DATE	DWN	CKD	APPD	ECN							

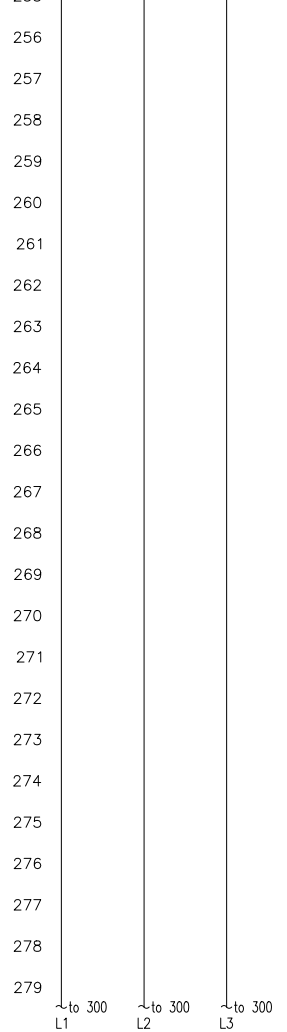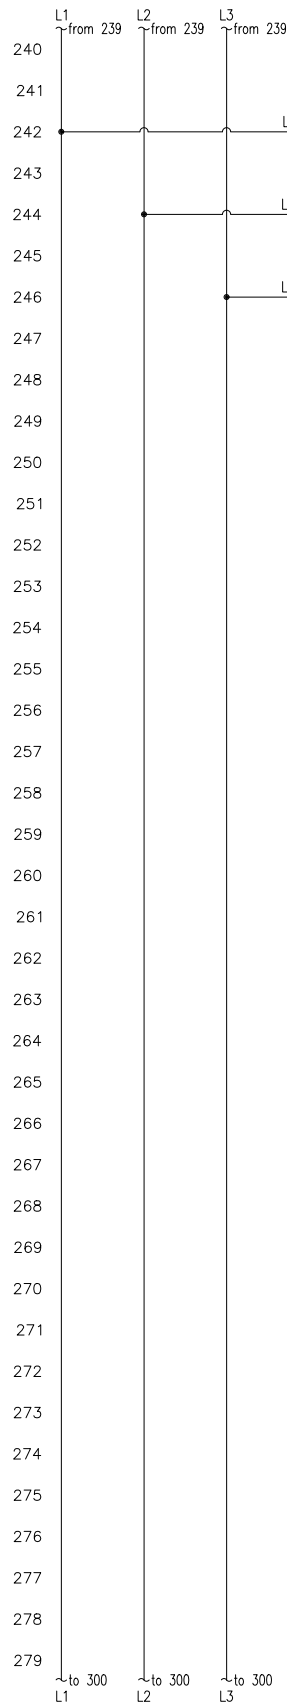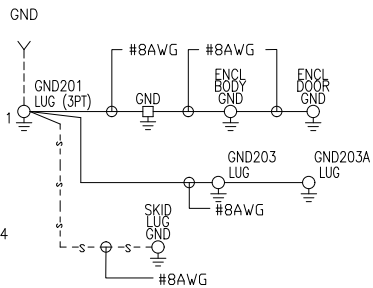


STD: Electrical v4.3		BAR = 1" AT PLOT SCALE
----------------------	---	------------------------

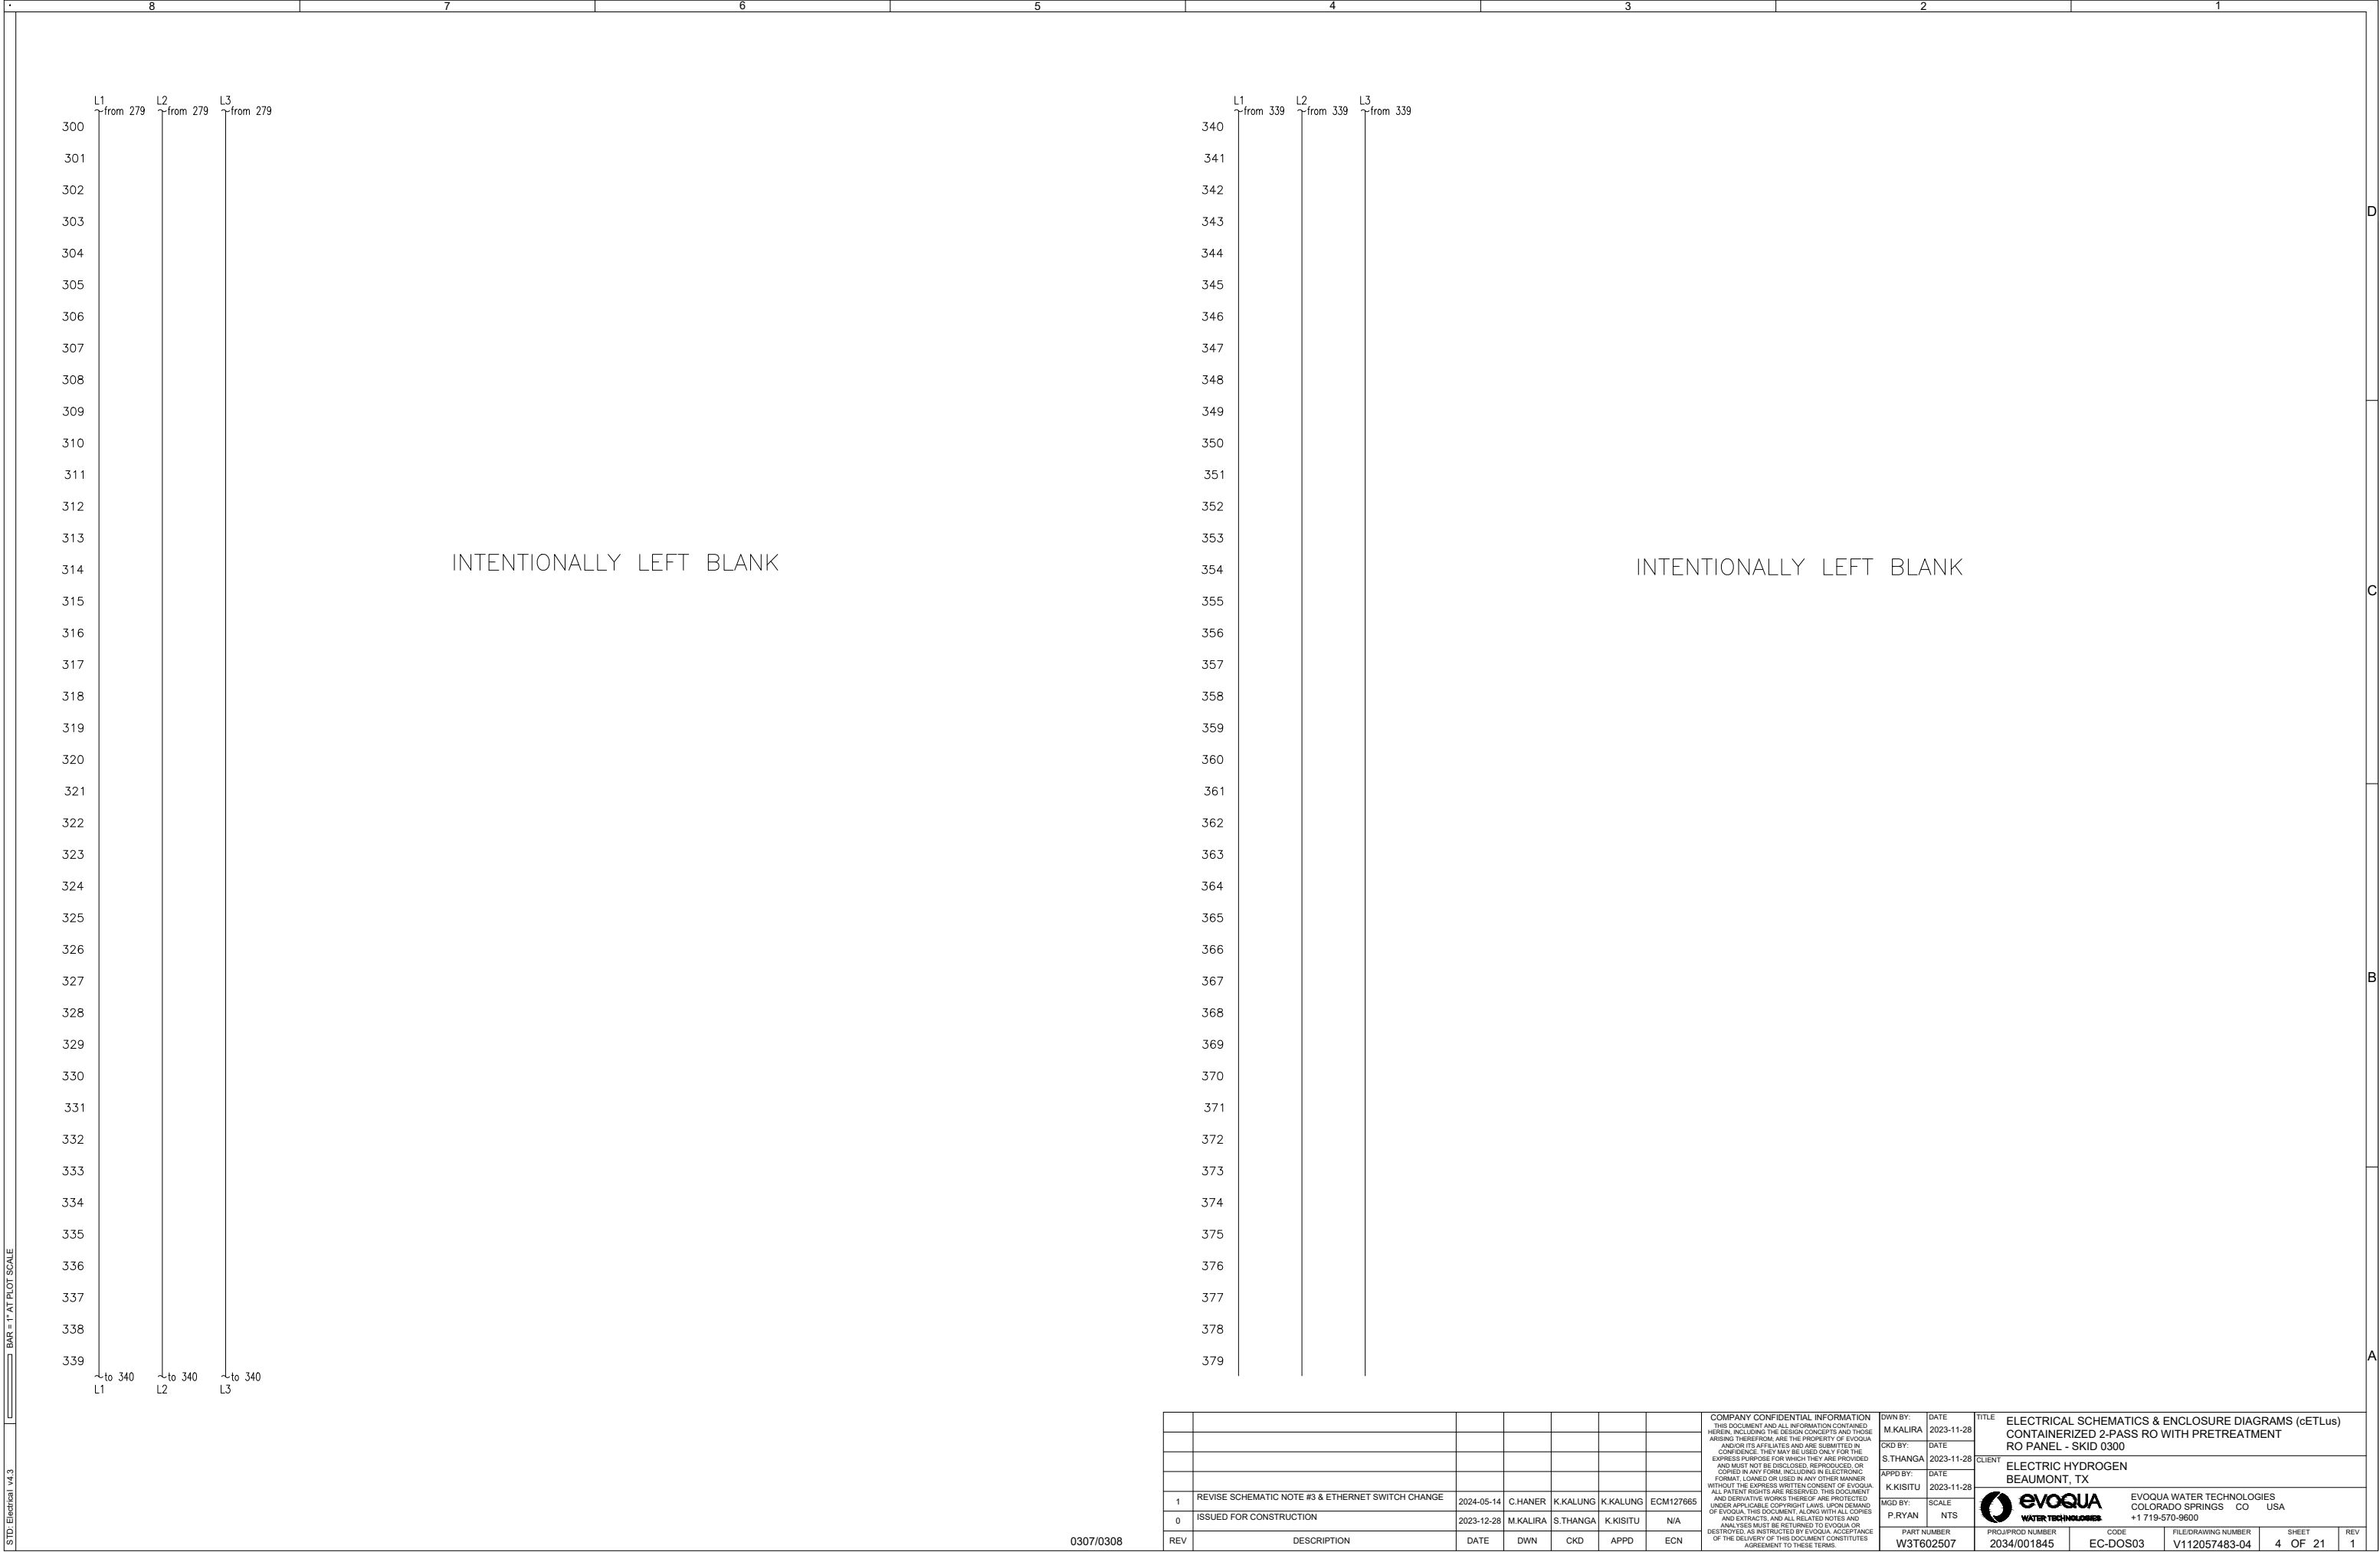

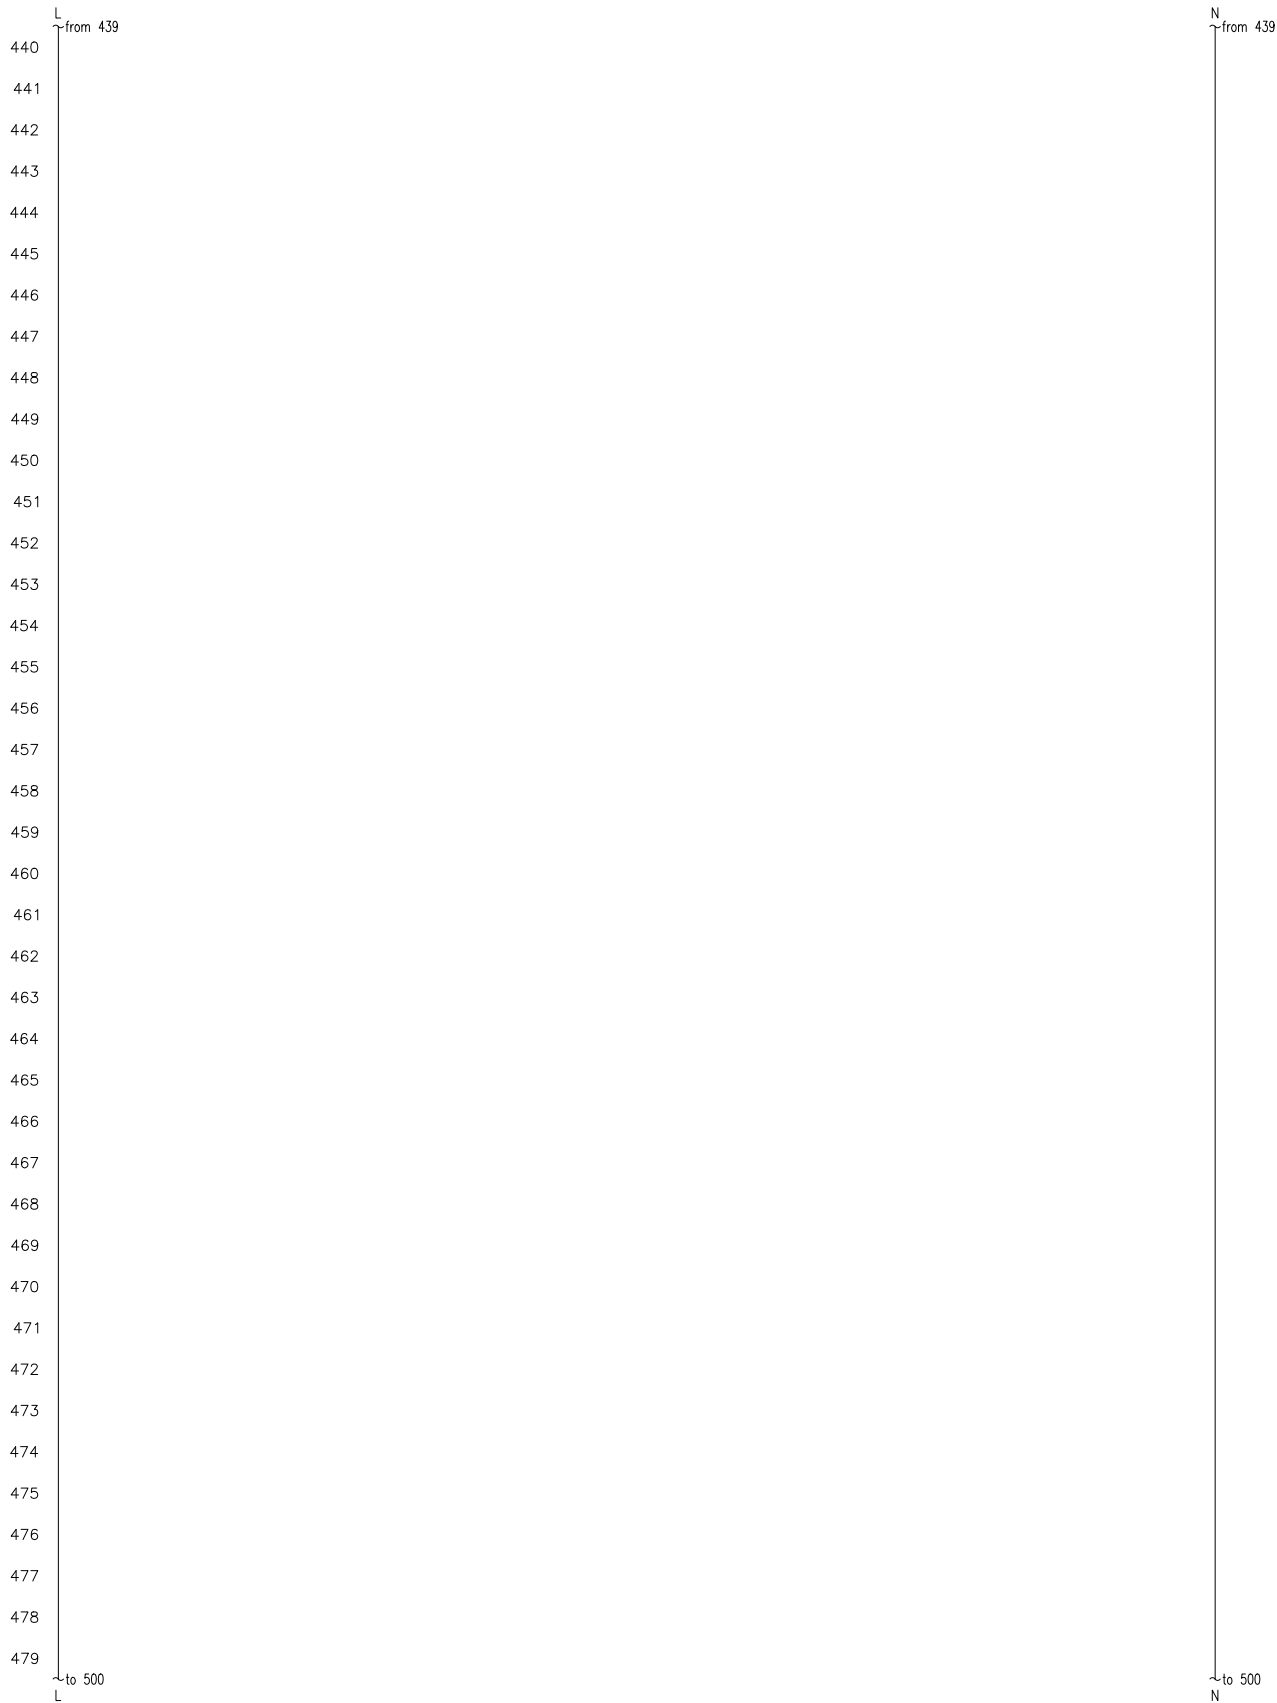


STD: Electrical v4.3

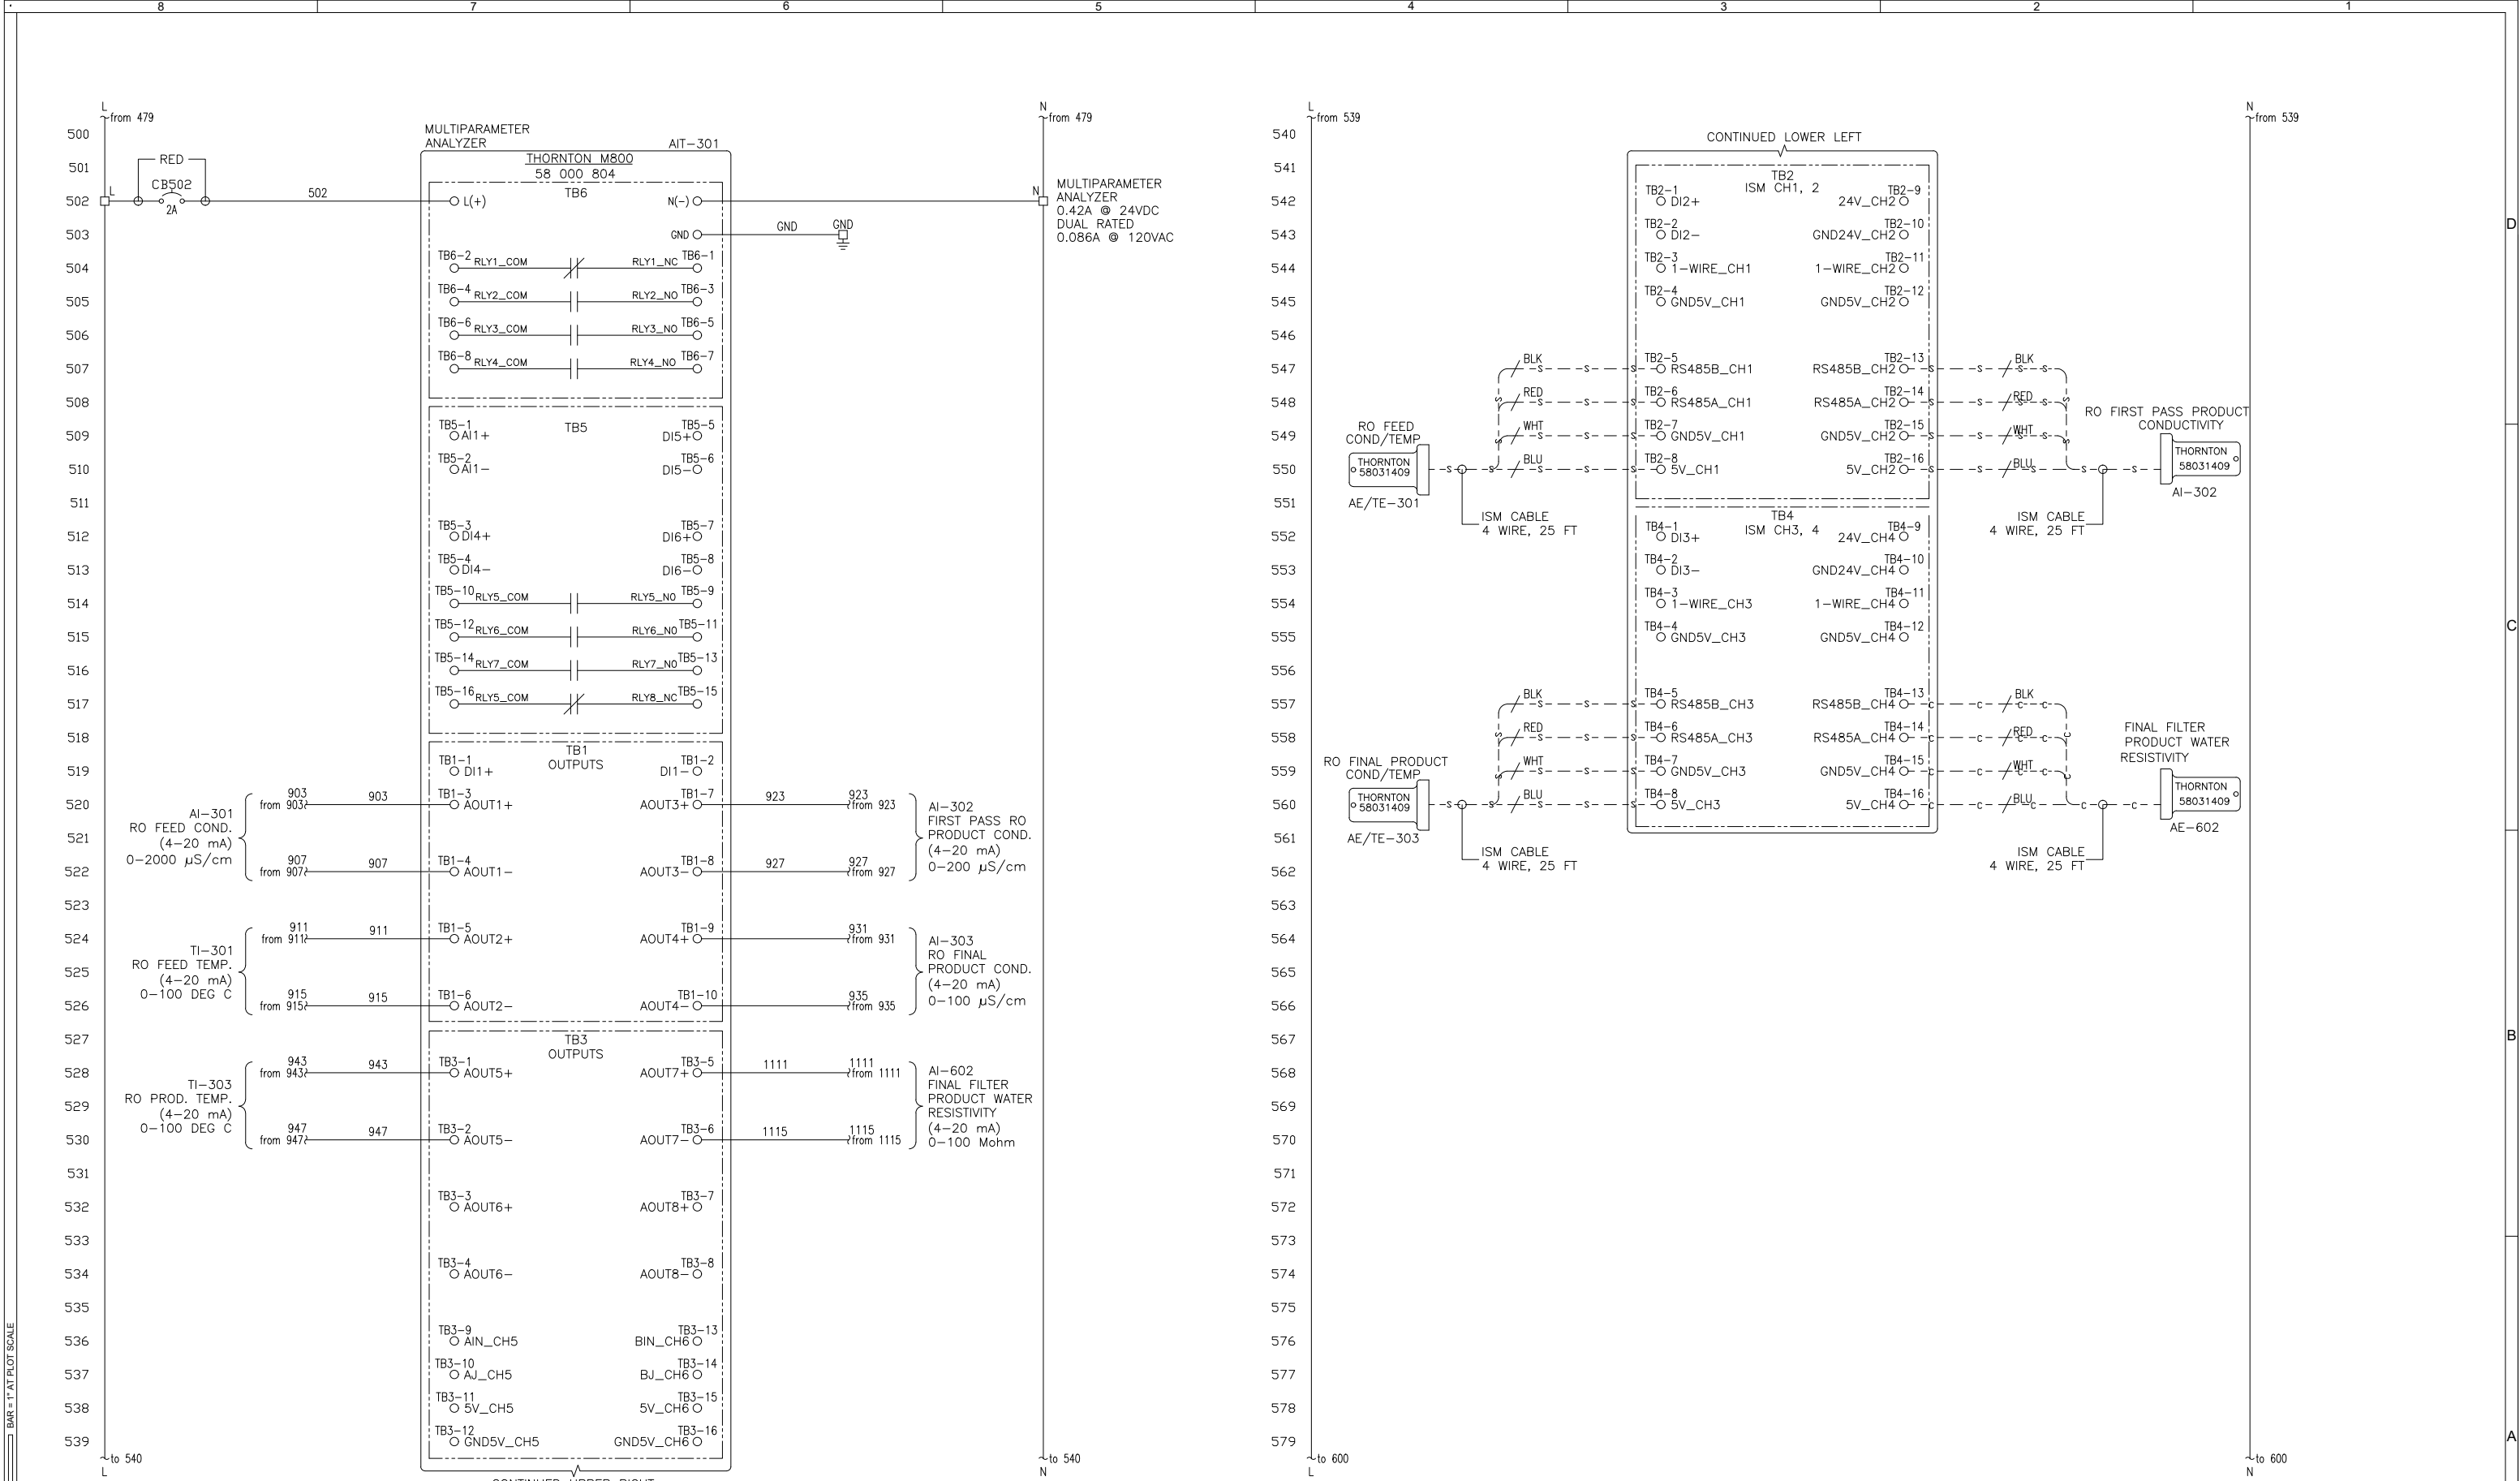

STD Electrical v4.3
BAR = 1" AT PLOT SCALE

0307/0308


							COMPANY CONFIDENTIAL INFORMATION THIS DOCUMENT AND ALL INFORMATION CONTAINED HEREIN, INCLUDING THE DESIGN CONCEPTS AND THOSE ARISING THEREFROM, ARE THE PROPERTY OF EVOQUA AND/OR ITS AFFILIATES AND ARE SUBMITTED IN CONFERENCE. THEY MAY BE USED ONLY FOR THE EXPRESS PURPOSE FOR WHICH THEY ARE PROVIDED AND MUST NOT BE DISCLOSED, REPRODUCED, OR COPIED IN ANY FORM, INCLUDING IN ELECTRONIC FORMAT, LOANED OR USED IN ANY OTHER MANNER WITHOUT THE EXPRESS WRITTEN CONSENT OF EVOQUA. ALL PATENT RIGHTS ARE RESERVED. THIS DOCUMENT AND DERIVATIVE WORKS THEREOF ARE PROTECTED UNDER APPLICABLE COPYRIGHT LAWS. UPON DEMAND OF EVOQUA, THIS DOCUMENT, ALONG WITH ALL COPIES AND EXTRACTS, AND ALL RELATED NOTES AND ANALYSES MUST BE RETURNED TO EVOQUA OR DESTROYED, AS INSTRUCTED BY EVOQUA. ACCEPTANCE OF THE DELIVERY OF THIS DOCUMENT CONSTITUTES AGREEMENT TO THESE TERMS.	DWN BY: M.KALIRA CKD BY: S.THANGA APPD BY: K.KISITU MGD BY: P.RYAN	DATE: 2023-11-28 DATE: 2023-11-28 DATE: 2023-11-28 SCALE: NTS	TITLE: ELECTRICAL SCHEMATICS & ENCLOSURE DIAGRAMS (cETLus) CONTAINERIZED 2-PASS RO WITH PRETREATMENT RO PANEL - SKID 0300 CLIENT: ELECTRIC HYDROGEN BEAUMONT, TX	 EVOQUA WATER TECHNOLOGIES COLORADO SPRINGS CO USA +1 719-570-9600	PROJ/PROD NUMBER: 2034/001845 CODE: EC-DOS03 FILE/DRAWING NUMBER: V112057483-06 SHEET: 6 OF 21 REV: 1
1	REVISE SCHEMATIC NOTE #3 & ETHERNET SWITCH CHANGE	2024-05-14	C.HANER	K.KALUNG	K.KALUNG	ECM127665						
0	ISSUED FOR CONSTRUCTION	2023-12-28	M.KALIRA	S.THANGA	K.KISITU	N/A						
REV	DESCRIPTION	DATE	DWN	CKD	APPD	ECN						

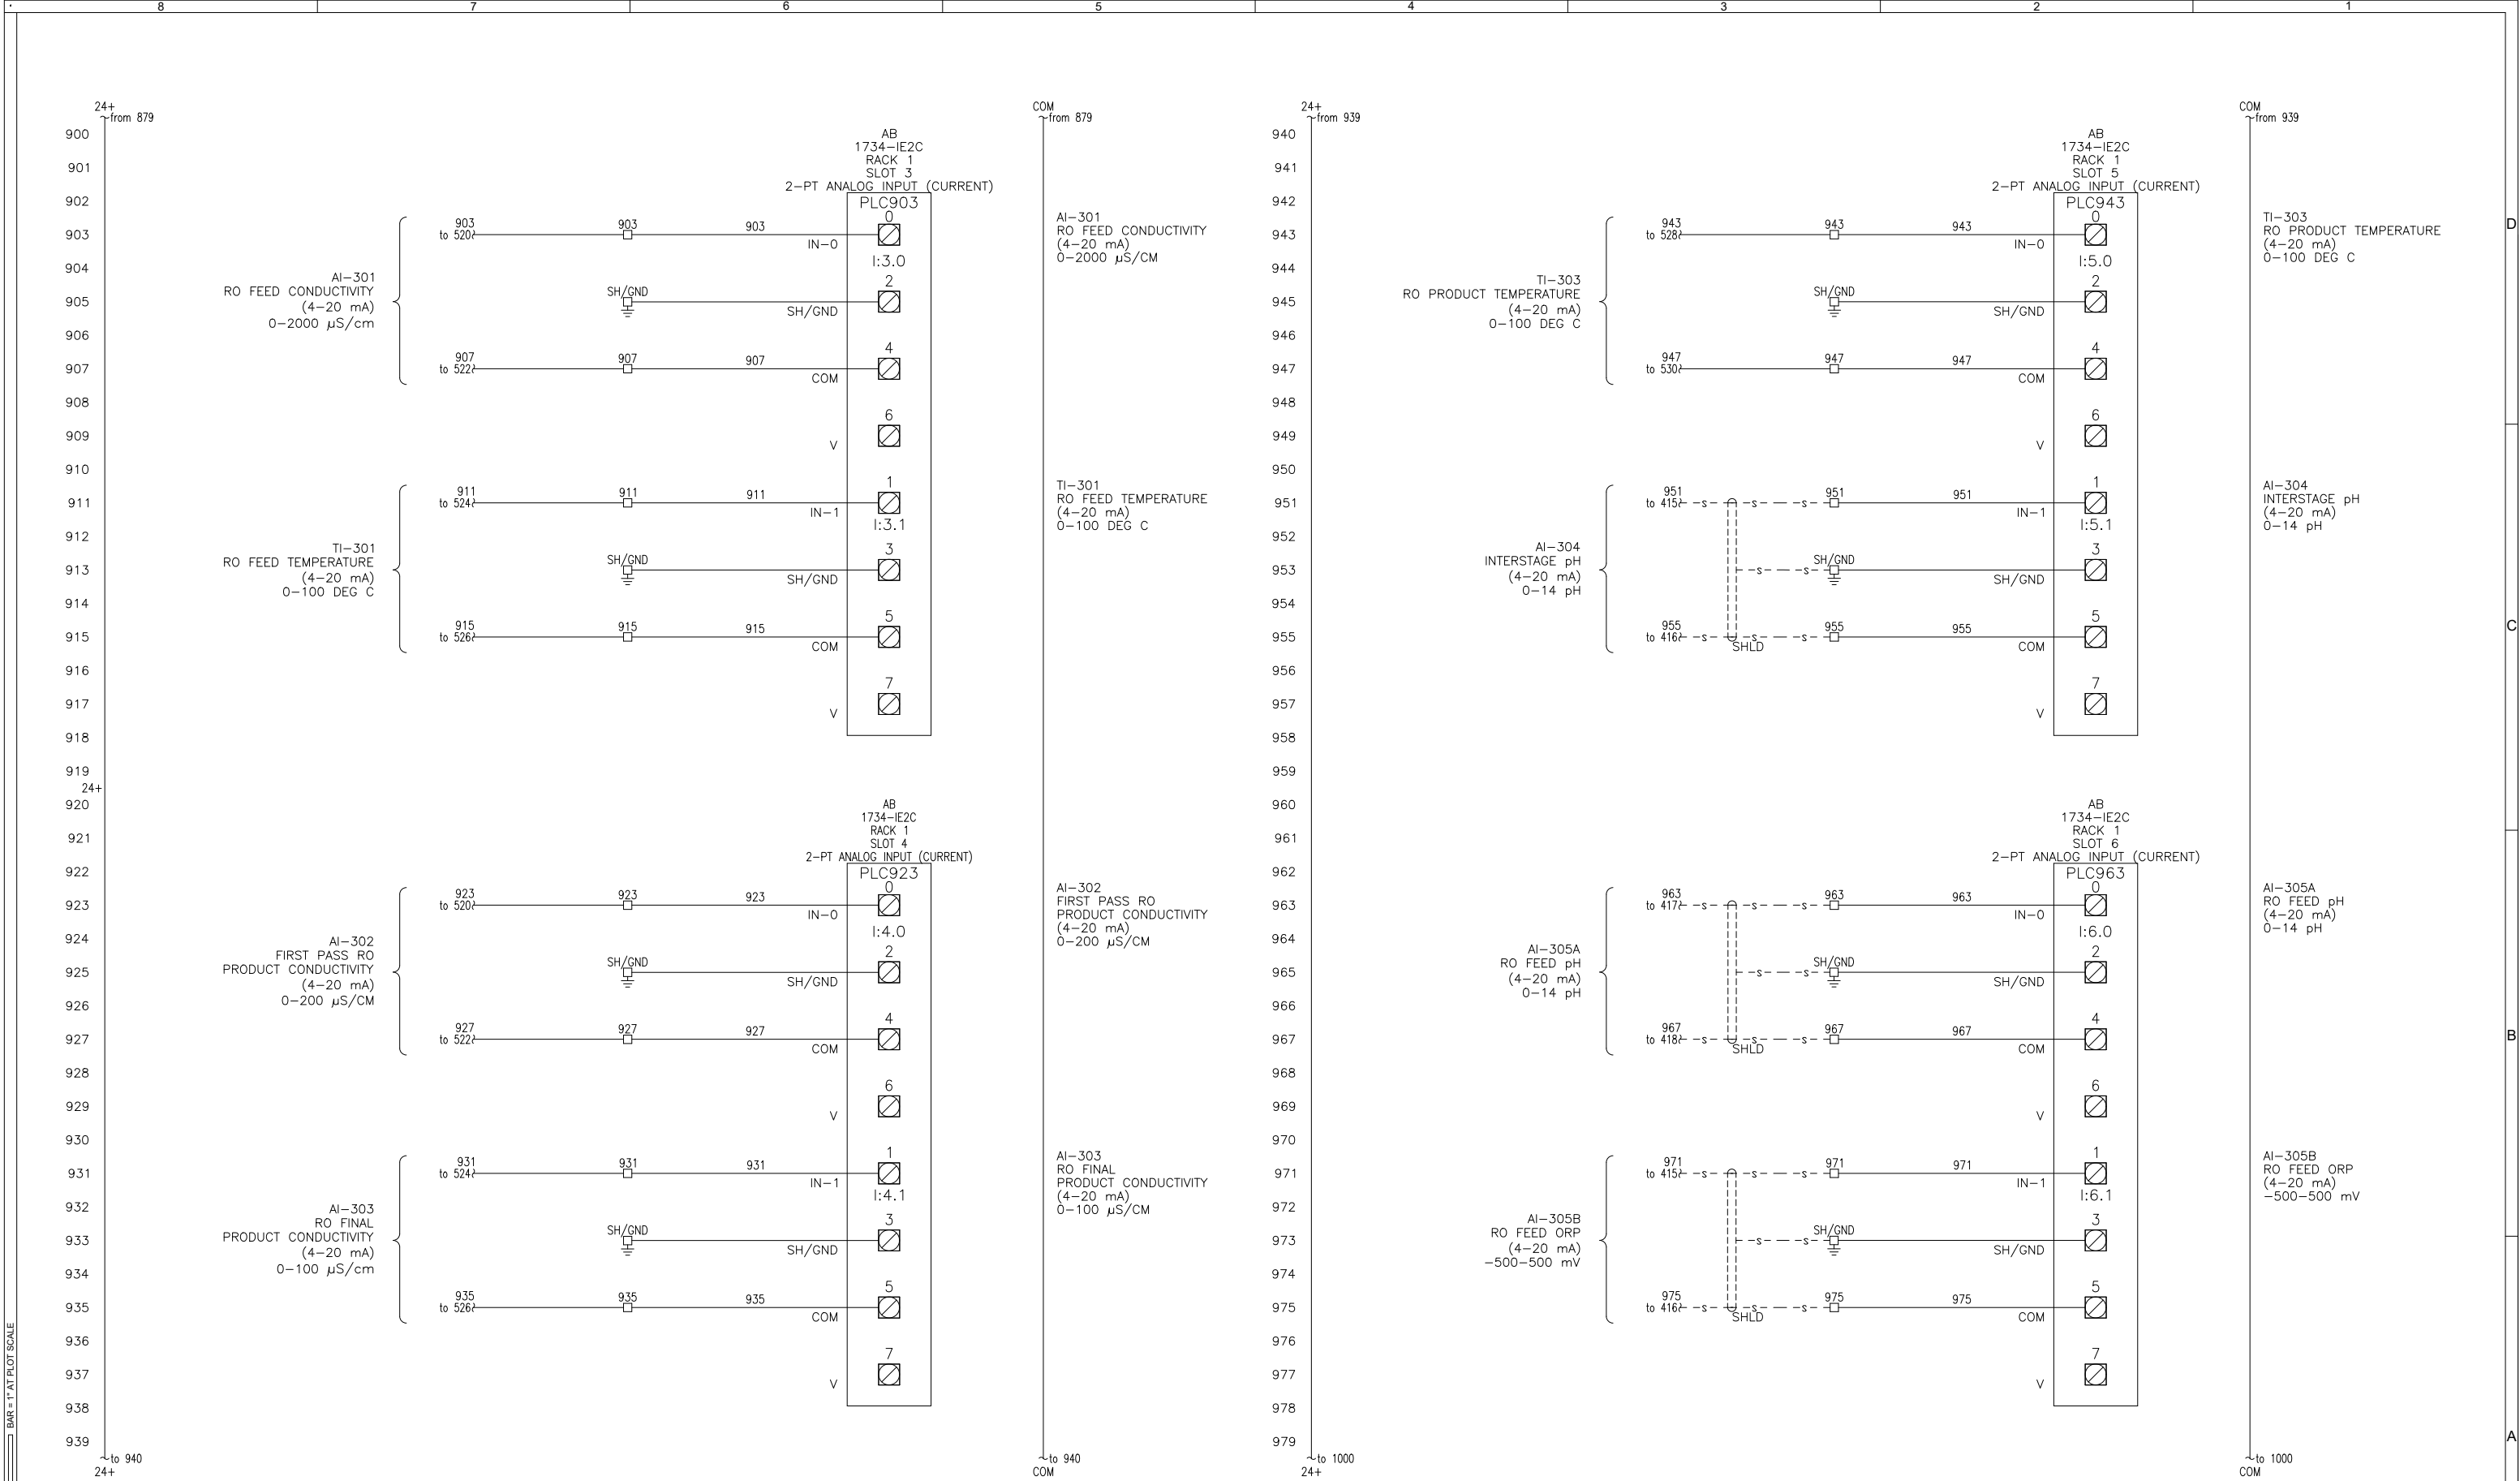

STD Electrical v4.3
BAR = 1" AT PLOT SCALE

COMPANY CONFIDENTIAL INFORMATION THIS DOCUMENT AND ALL INFORMATION CONTAINED HEREIN, INCLUDING THE DESIGN CONCEPTS AND THOSE ARISING THEREFROM, ARE THE PROPERTY OF EVOQUA AND/OR ITS AFFILIATES AND ARE SUBMITTED IN CONFIDENCE. THEY MAY BE USED ONLY FOR THE EXPRESS PURPOSE FOR WHICH THEY ARE PROVIDED AND MUST NOT BE DISCLOSED, REPRODUCED, OR COPIED IN ANY FORM, INCLUDING IN ELECTRONIC FORMAT, LOANED OR USED IN ANY OTHER MANNER WITHOUT THE EXPRESS WRITTEN CONSENT OF EVOQUA. ALL PATENT RIGHTS ARE RESERVED. THIS DOCUMENT AND DERIVATIVE WORKS THEREOF ARE PROTECTED UNDER APPLICABLE COPYRIGHT LAWS. UPON DEMAND OF EVOQUA, THIS DOCUMENT, ALONG WITH ALL COPIES AND EXTRACTS, AND ALL RELATED NOTES AND ANALYSES MUST BE RETURNED TO EVOQUA OR DESTROYED, AS INSTRUCTED BY EVOQUA. ACCEPTANCE OF THE DELIVERY OF THIS DOCUMENT CONSTITUTES AGREEMENT TO THESE TERMS.							DWN BY:	DATE:	TITLE:			
							M.KALIRA	2023-11-28	ELECTRICAL SCHEMATICS & ENCLOSURE DIAGRAMS (cETLus) CONTAINERIZED 2-PASS RO WITH PRETREATMENT RO PANEL - SKID 0300			
							CKD BY:	DATE:	CLIENT:			
							S.THANGA	2023-11-28	ELECTRIC HYDROGEN BEAUMONT, TX			
							APPD BY:	DATE:				
							K.KISITU	2023-11-28				
							MGD BY:	SCALE:	EVOQUA WATER TECHNOLOGIES 10000 ROAD 10000 DALLAS, TX 75243 USA +1 719-570-9600			
							P.RYAN	NTS				
1	REVISE SCHEMATIC NOTE #3 & ETHERNET SWITCH CHANGE	2024-05-14	C.HANER	K.KALUNG	K.KALUNG	ECM127665						
0	ISSUED FOR CONSTRUCTION	2023-12-28	M.KALIRA	S.THANGA	K.KISITU	N/A						
REV	DESCRIPTION	DATE	DWN	CKD	APPD	ECN	PART NUMBER	PROJ/PROD NUMBER	CODE	FILE/DRAWING NUMBER	SHEET	REV
							W3T602507	2034/001845	EC-DOS03	V112057483-10	10 OF 21	1

0307/0308

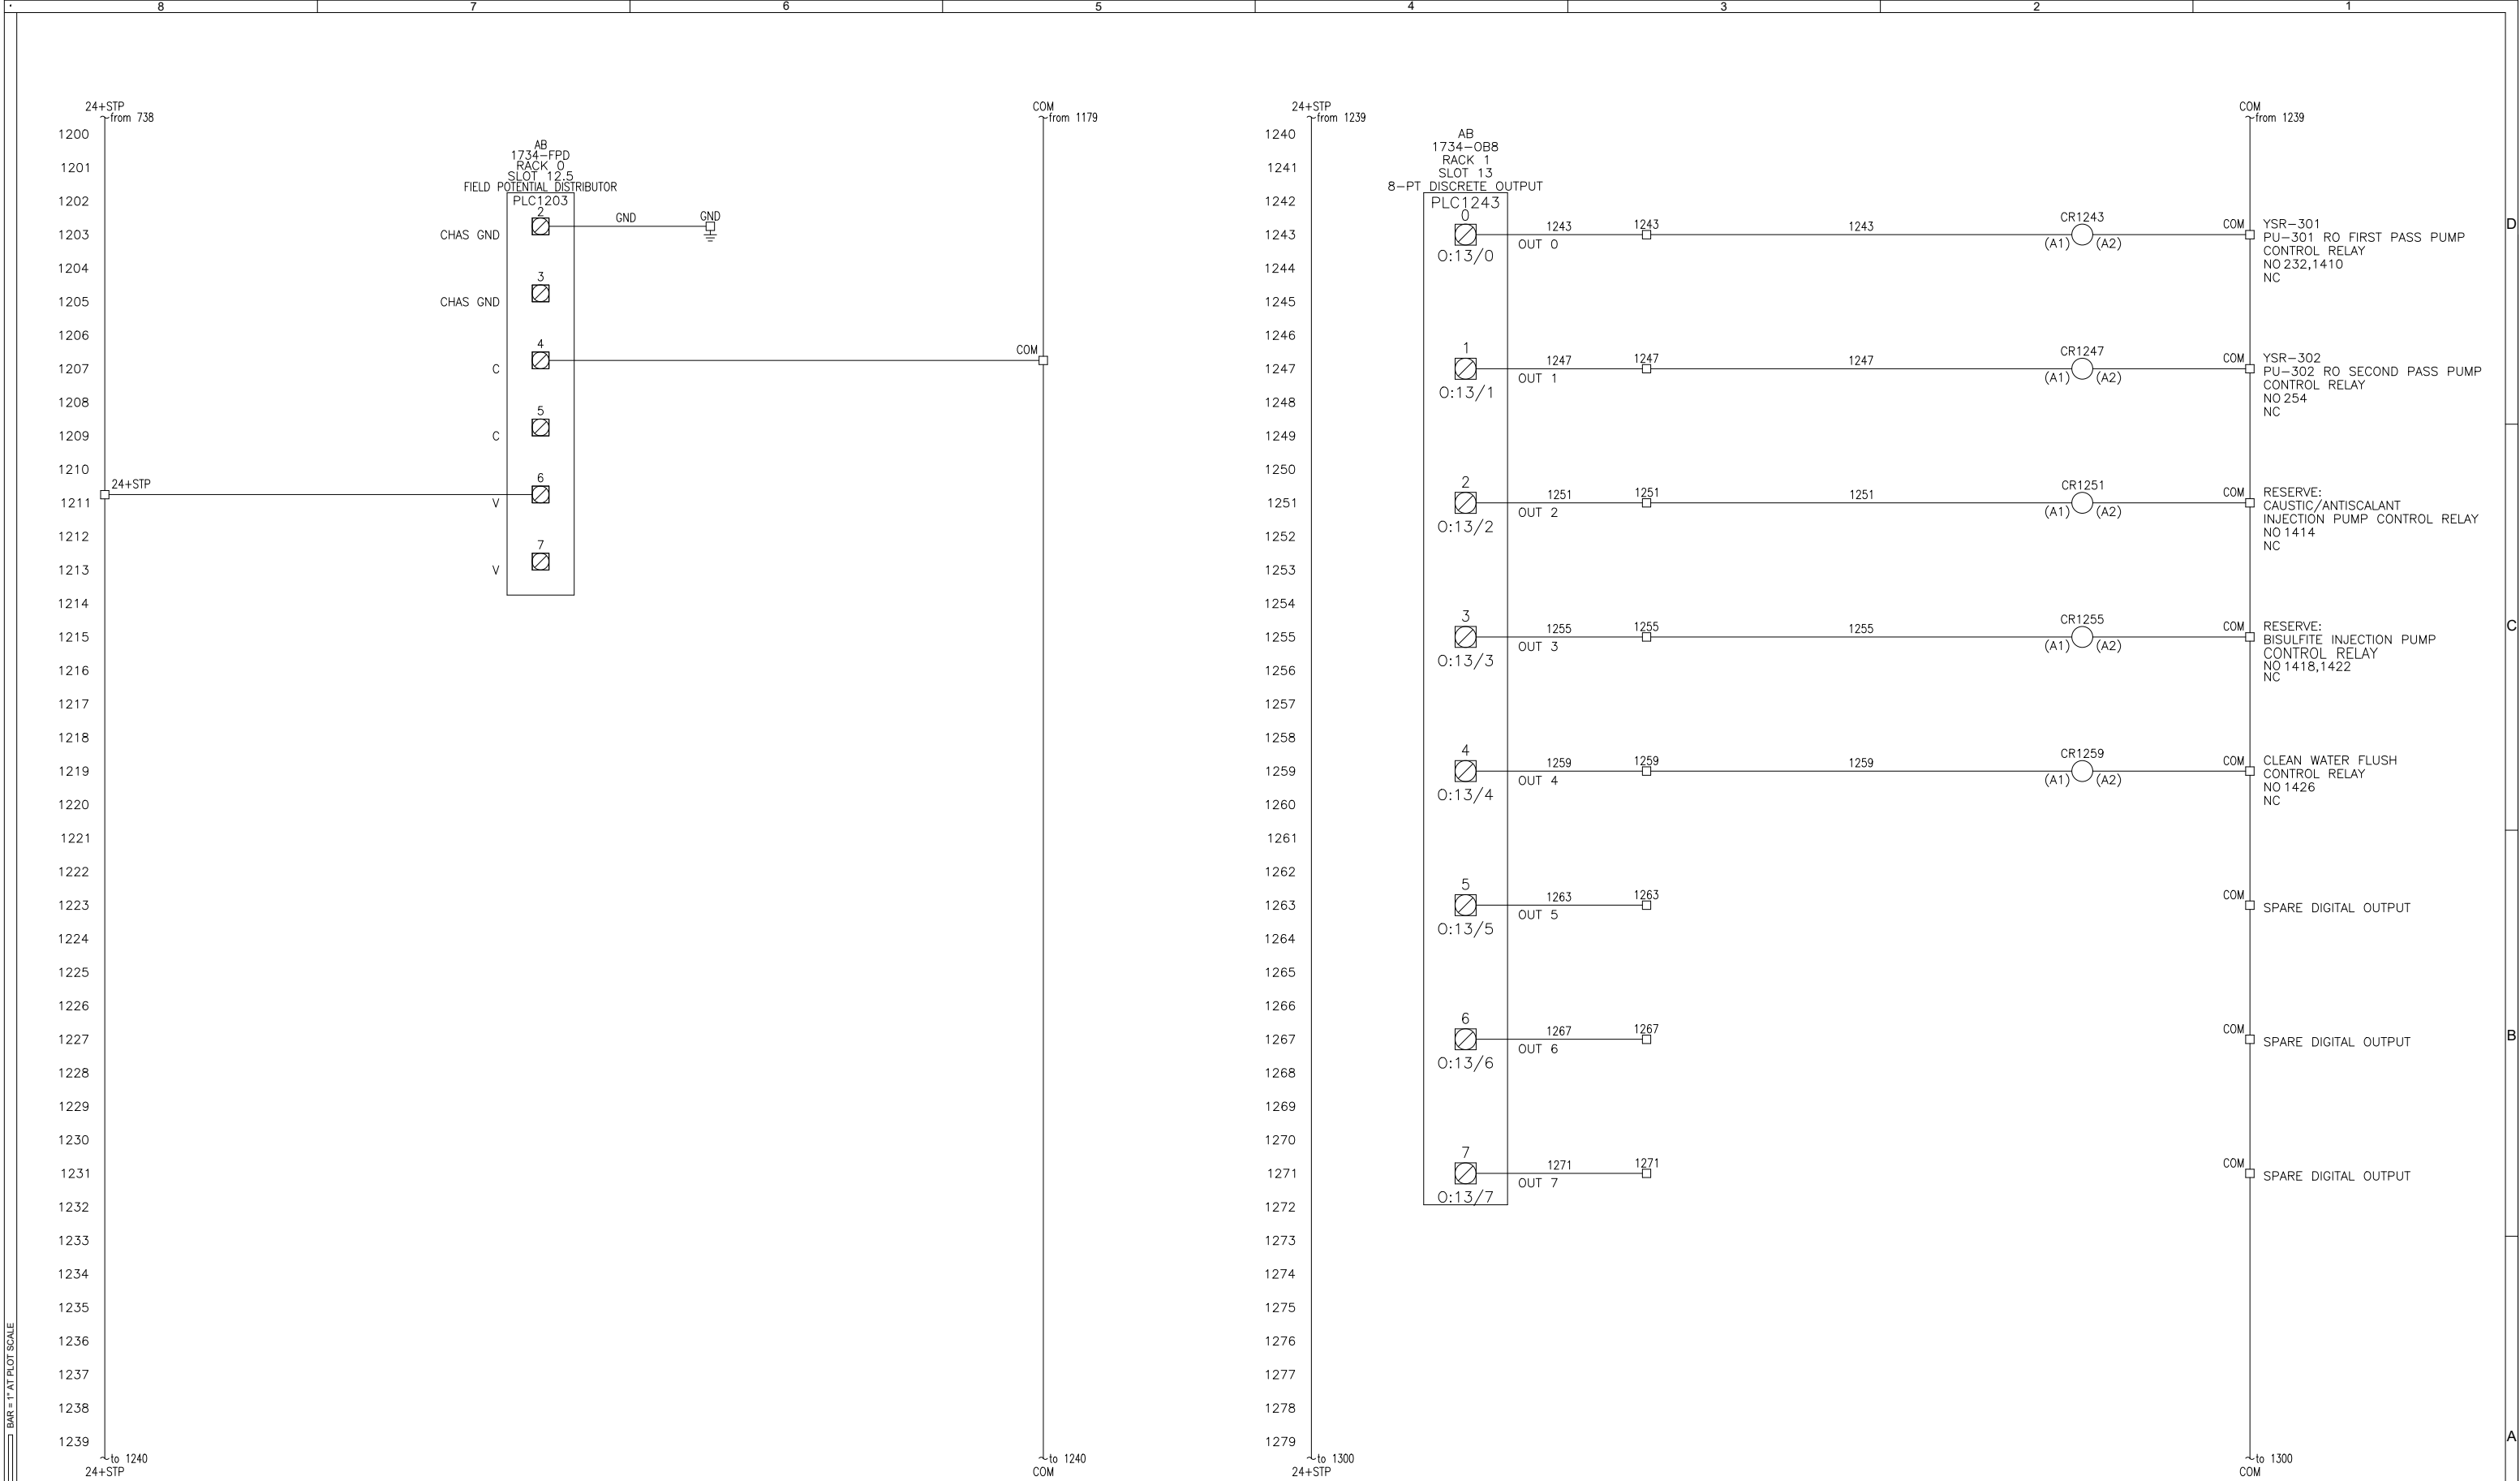


STD Electrical v4.3
BAR = 1" AT PLOT SCALE

							COMPANY CONFIDENTIAL INFORMATION THIS DOCUMENT AND ALL INFORMATION CONTAINED HEREIN, INCLUDING THE DESIGN CONCEPTS AND THOSE ARISING THEREFROM, ARE THE PROPERTY OF EVOQUA AND/OR ITS AFFILIATES AND ARE SUBMITTED IN CONFERENCE. THEY MAY BE USED ONLY FOR THE EXPRESS PURPOSE FOR WHICH THEY ARE PROVIDED AND MUST NOT BE DISCLOSED, REPRODUCED, OR COPIED IN ANY FORM, INCLUDING IN ELECTRONIC FORMAT, LOANED OR USED IN ANY OTHER MANNER WITHOUT THE EXPRESS WRITTEN CONSENT OF EVOQUA. ALL PATENT RIGHTS ARE RESERVED. THIS DOCUMENT AND DERIVATIVE WORKS THEREOF ARE PROTECTED UNDER APPLICABLE COPYRIGHT LAWS. UPON DEMAND OF EVOQUA, THIS DOCUMENT, ALONG WITH ALL COPIES AND EXTRACTS, AND ALL RELATED NOTES AND ANALYSES MUST BE RETURNED TO EVOQUA OR DESTROYED, AS INSTRUCTED BY EVOQUA. ACCEPTANCE OF THE DELIVERY OF THIS DOCUMENT CONSTITUTES AGREEMENT TO THESE TERMS.	DWN BY: M.KALIRA CKD BY: S.THANGA APPD BY: K.KISITU MGD BY: P.RYAN	DATE: 2023-11-28 DATE: 2023-11-28 DATE: 2023-11-28 SCALE: NTS	TITLE: ELECTRICAL SCHEMATICS & ENCLOSURE DIAGRAMS (cETLus) CONTAINERIZED 2-PASS RO WITH PRETREATMENT RO PANEL - SKID 0300 CLIENT: ELECTRIC HYDROGEN BEAUMONT, TX	 evoqua WATER TECHNOLOGIES	EVOQUA WATER TECHNOLOGIES COLORADO SPRINGS CO USA +1 719-570-9600	PART NUMBER: W3T602507 PROJ/PROD NUMBER: 2034/001845 CODE: EC-DOS03 FILE/DRAWING NUMBER: V112057483-13 SHEET: 13 OF 21 REV: 1
1	REVISE SCHEMATIC NOTE #3 & ETHERNET SWITCH CHANGE	2024-05-14	C.HANER	K.KALUNG	K.KALUNG	ECM127665							
0	ISSUED FOR CONSTRUCTION	2023-12-28	M.KALIRA	S.THANGA	K.KISITU	N/A							
REV	DESCRIPTION	DATE	DWN	CKD	APPD	ECN							

0307/0308



WITHHOLD THE EXPRESS WRITEN CONSENT OF EVOQUA. ALL PATENT RIGHTS ARE RESERVED. THIS DOCUMENT AND DERIVATIVE WORKS THEREOF ARE PROTECTED BY U.S. PATENT AND COPYRIGHT LAWS, AND BY INTERNATIONAL TRADE LAW. THIS DOCUMENT, AND EXTRACTS, AND ALL RELATED NOTES AND ANALYSES MUST BE RETURNED TO EVOQUA IF DESTROYED, AS INSTRUCTED BY EVOQUA. ACCEPTANCE OF THE DELIVERY OF THIS DOCUMENT CONSTITUTES AGREEMENT TO THESE TERMS.		K.KISITU 2023-11-28 MOD BY: SCALE P.RYAN NTS	 evoqua WATER TECHNOLOGIES	EVOQUA WATER TECHNOLOGIES COLORADO SPRINGS CO USA +1 719-570-9600
PART NUMBER W37602507	PROJ/PROD NUMBER 0030401845	CODE EC-DS053	FILE/DRAWING NUMBER V112057483-14	SHEET 14 OF 21
				REV 1

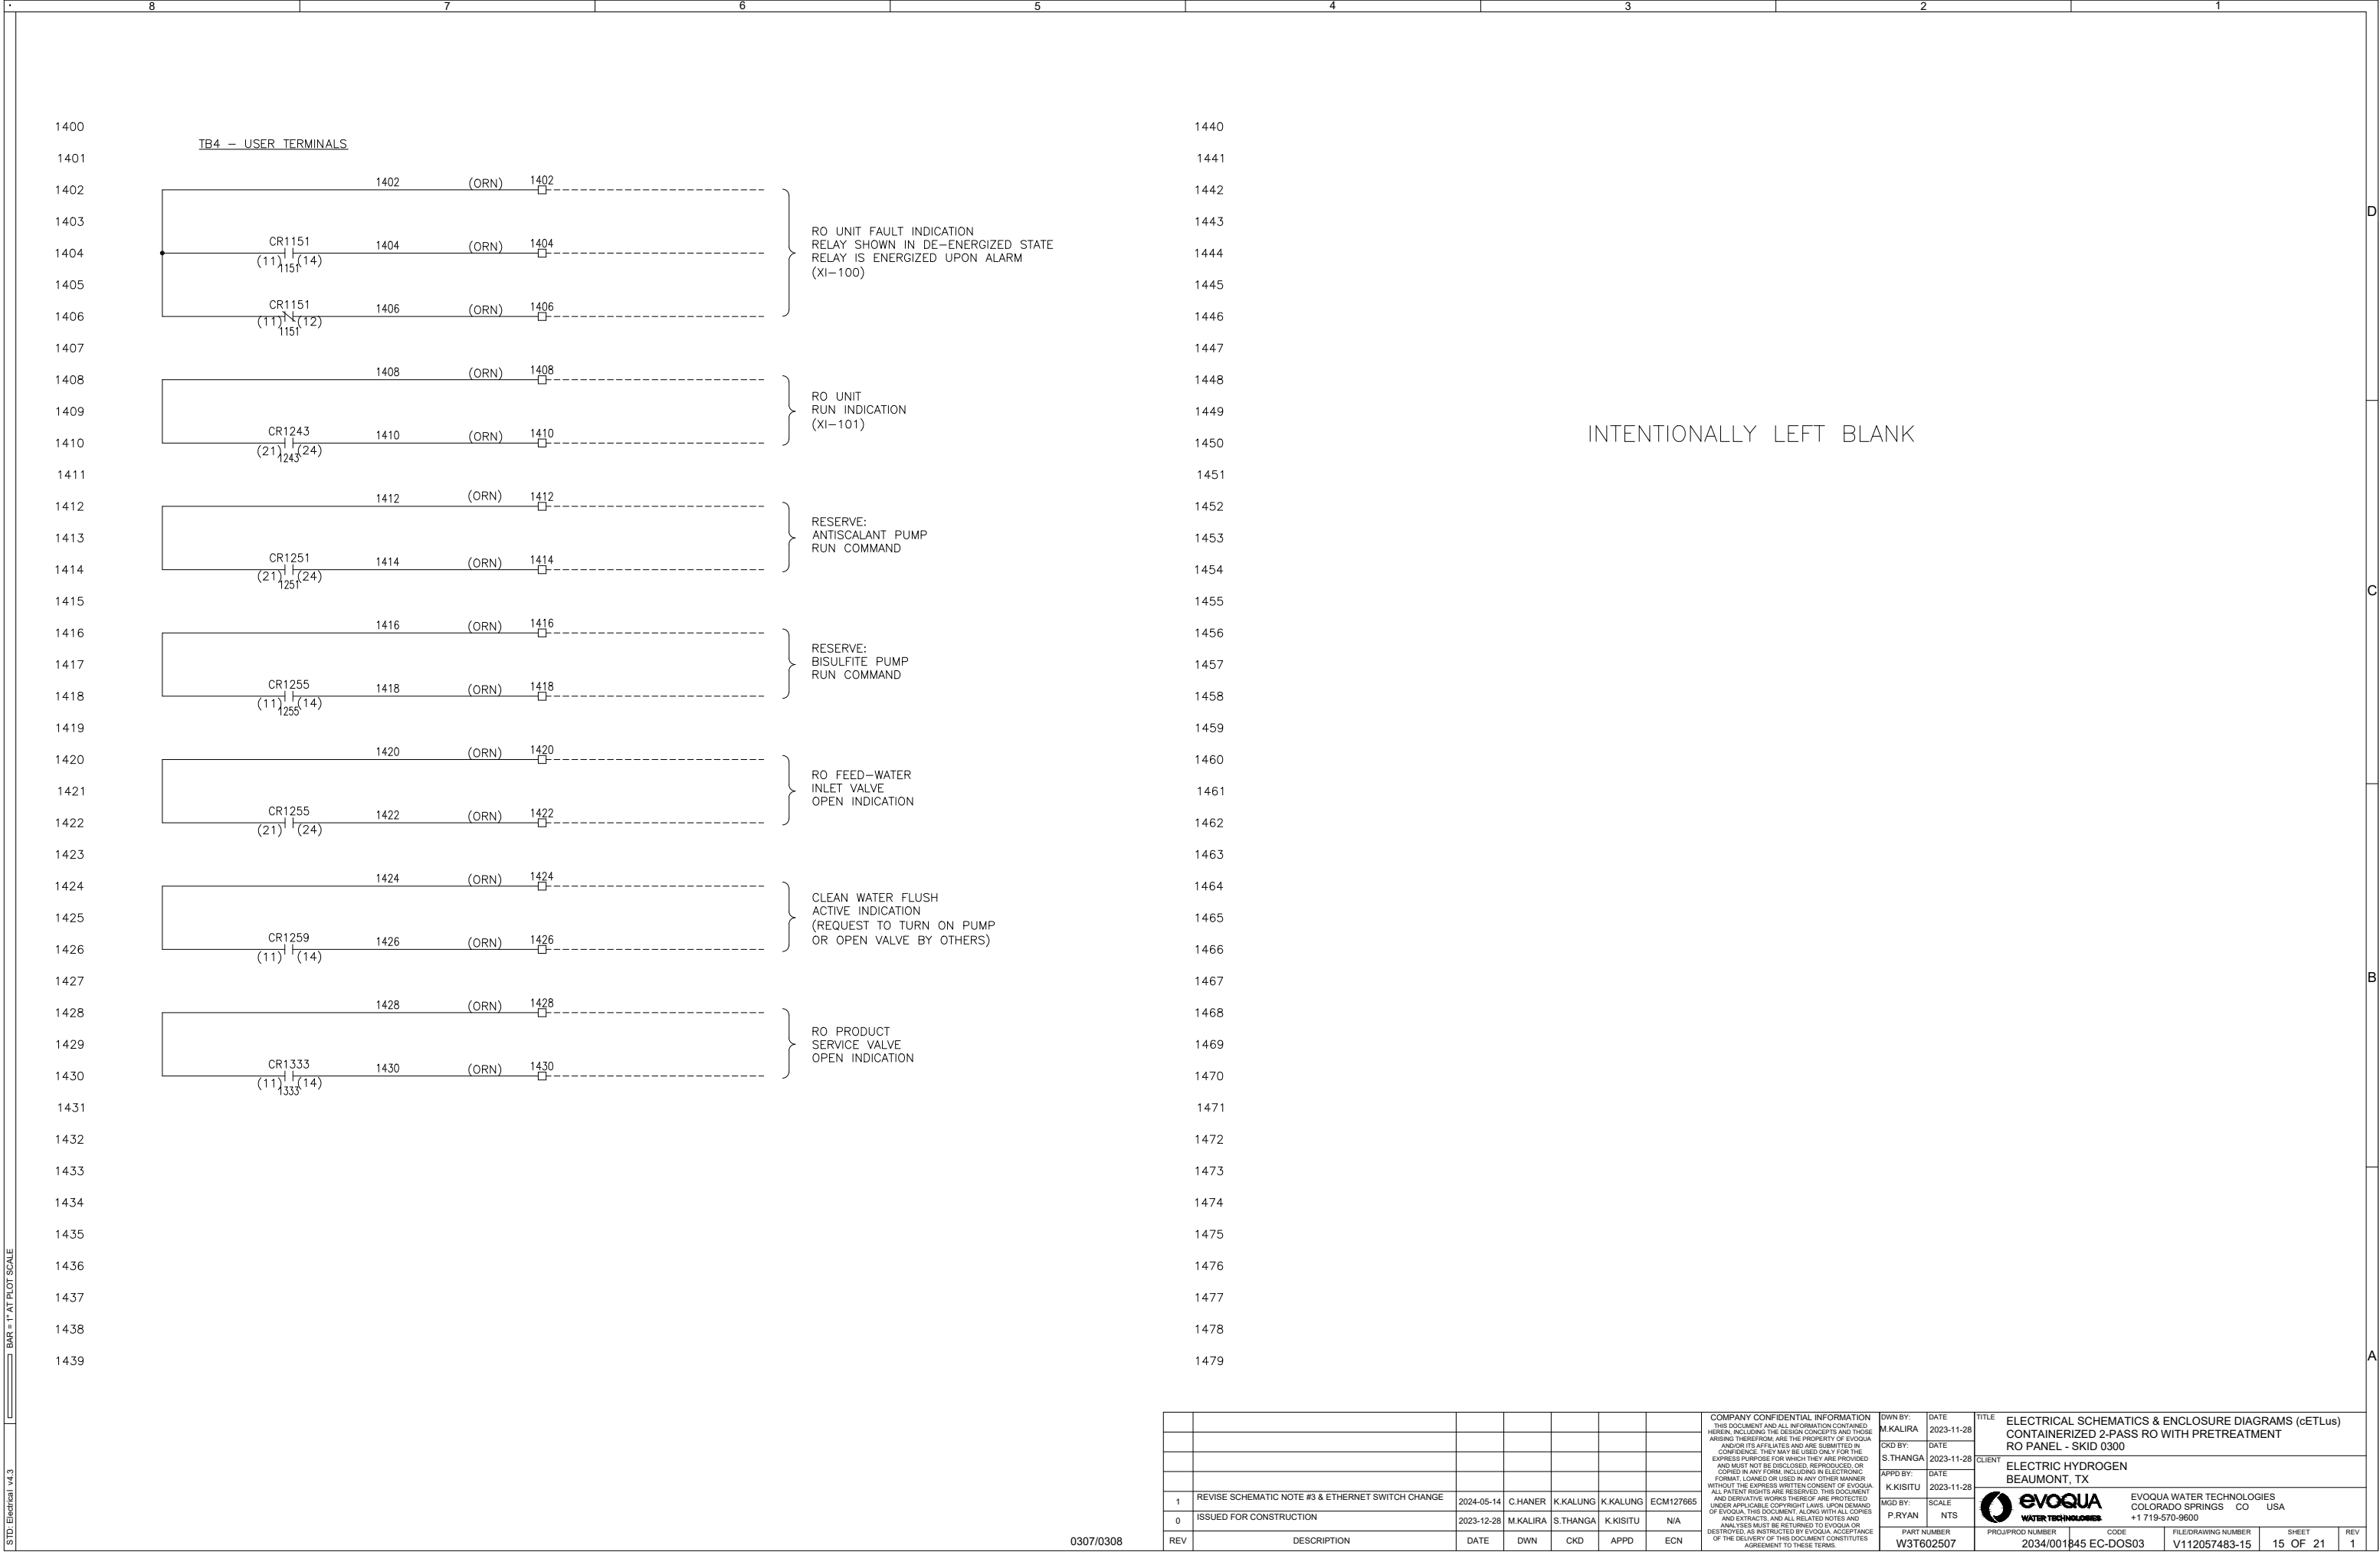

STD Electrical v4.3

BAR = 1" AT PLOT SCALE

							COMPANY CONFIDENTIAL INFORMATION THIS DOCUMENT AND ALL INFORMATION CONTAINED HEREIN, INCLUDING THE DESIGN CONCEPTS AND THOSE ARISING THEREFROM, ARE THE PROPERTY OF EVOQUA AND/OR ITS AFFILIATES AND ARE SUBMITTED IN CONFERENCE. THEY MAY BE USED ONLY FOR THE EXPRESS PURPOSE FOR WHICH THEY ARE PROVIDED AND MUST NOT BE DISCLOSED, REPRODUCED, OR COPIED IN ANY FORM, INCLUDING IN ELECTRONIC FORMAT, LOANED OR USED IN ANY OTHER MANNER WITHOUT THE EXPRESS WRITTEN CONSENT OF EVOQUA. ALL PATENT RIGHTS ARE RESERVED. THIS DOCUMENT AND DERIVATIVE WORKS THEREOF ARE PROTECTED UNDER APPLICABLE COPYRIGHT LAWS. UPON DEMAND OF EVOQUA, THIS DOCUMENT, ALONG WITH ALL COPIES AND EXTRACTS, AND ALL RELATED NOTES AND ANALYSES MUST BE RETURNED TO EVOQUA OR DESTROYED, AS INSTRUCTED BY EVOQUA. ACCEPTANCE OF THE DELIVERY OF THIS DOCUMENT CONSTITUTES AGREEMENT TO THESE TERMS.	DWN BY: M.KALIRA	DATE: 2023-11-28	TITLE: ELECTRICAL SCHEMATICS & ENCLOSURE DIAGRAMS (cETLus) CONTAINERIZED 2-PASS RO WITH PRETREATMENT RO PANEL - SKID 0300
								CKD BY: S.THANGA	DATE: 2023-11-28	CLIENT: ELECTRIC HYDROGEN BEAUMONT, TX
								APPD BY: K.KISITU	DATE: 2023-11-28	
1	REVISE SCHEMATIC NOTE #3 & ETHERNET SWITCH CHANGE	2024-05-14	C.HANER	K.KALUNG	K.KALUNG	ECM127665		MGD BY: P.RYAN	SCALE: NTS	
0	ISSUED FOR CONSTRUCTION	2023-12-28	M.KALIRA	S.THANGA	K.KISITU	N/A				
REV	DESCRIPTION	DATE	DWN	CKD	APPD	ECN		PART NUMBER: W3T602507	PROJ/PROD NUMBER: 2034/001845	CODE: EC-DOS03
									FILE/DRAWING NUMBER: V112057483-15	SHEET: 15 OF 21
										REV: 1

0307/0308

1

2

3

4

5

6


7

8


		8		7		6		5		4		3		2		1							
1500		INTENTIONALLY LEFT BLANK										1540											
1501												1541											
1502												1542											
1503												1543											
1504												1544		INTENTIONALLY LEFT BLANK									
1505												1545											
1506												1546											
1507												1547											
1539												1579											
1		REVISE SCHEMATIC NOTE #3 & ETHERNET SWITCH CHANGE		2024-05-14		C.HANER		K.KALUNG		K.KALUNG		ECM127665											
0		ISSUED FOR CONSTRUCTION		2023-12-28		M.KALIRA		S.THANGA		K.KISITU		N/A											
REV		DESCRIPTION		DATE		DWN		CKD		APPD		ECN											

NOTES: UNLESS OTHERWISE SPECIFIED


- THIS PANEL TO BE MOUNTED ON THE RO SKID 0300.
- THIS ENCLOSURE IS TO BE NEMA 4 CARBON STEEL
- MANUFACTURING TO LAYOUT BACKPANEL AS SHOWN.
- ALL WIREWAYS TO BE 4" HIGH.
- MANUFACTURING TO VERIFY ALL DIMENSIONS AND CUTOUT SIZES BEFORE CUTTING OR DRILLING PANEL.
- DIN RAIL TO BE MOUNTED ON 1" STANDOFFS.
- FUSIBLE DISCONNECT WILL VARY DEPENDING ON MODEL.
- CONDUIT MATERIAL TO BE EMT.
- PNEUMATIC TUBING MATERIAL TO BE PE.

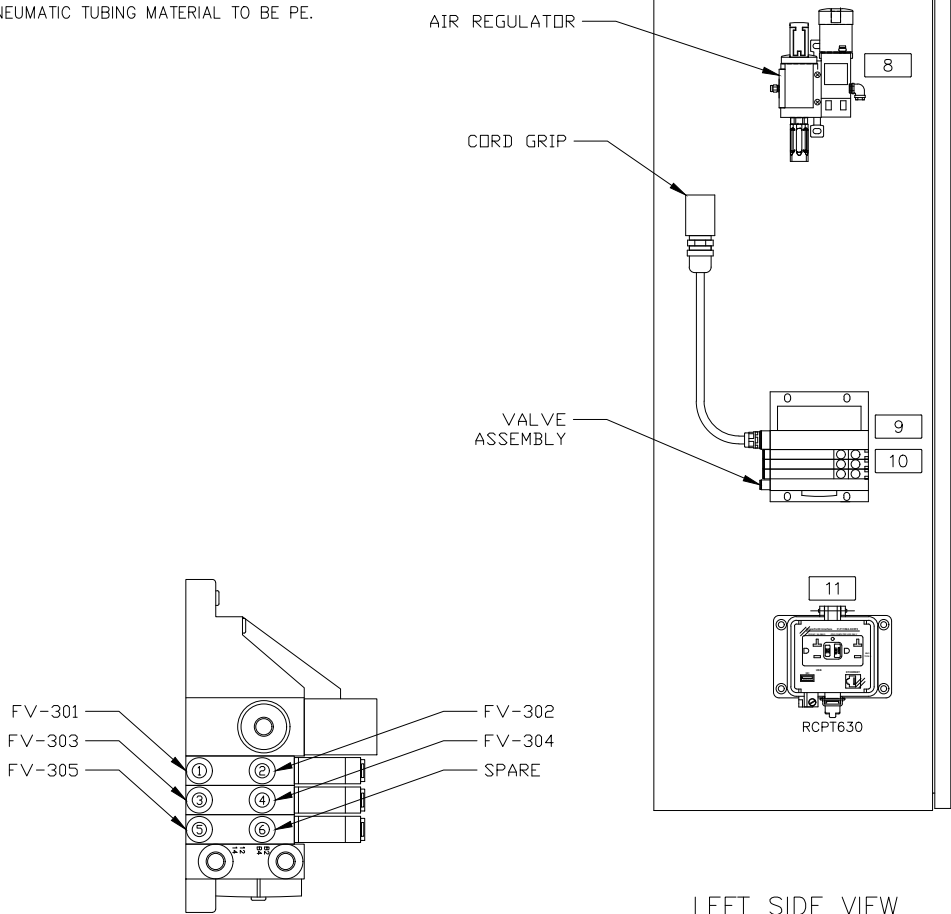

LEFT SIDE VIEW

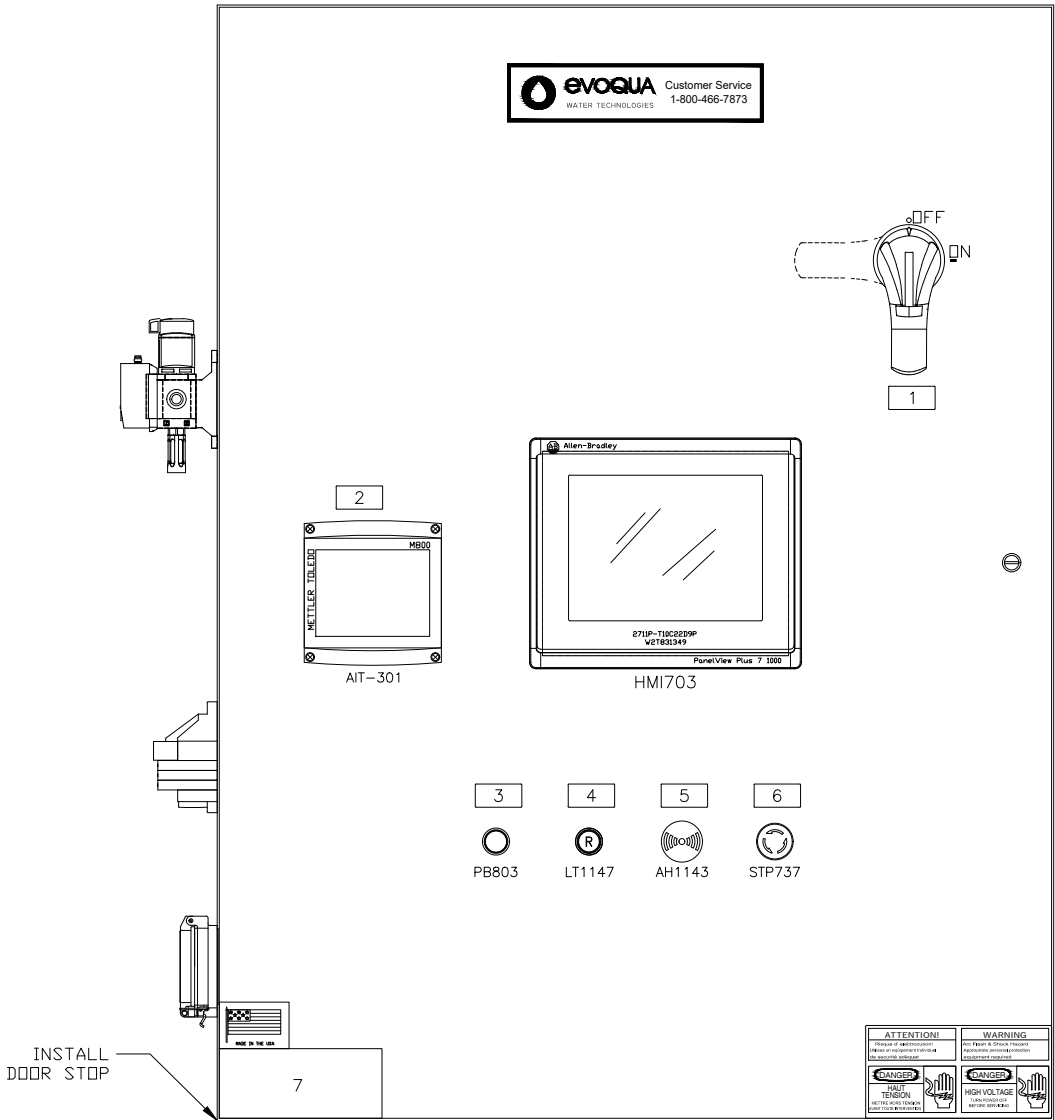

PANEL LAYOUT
48"x36"x12"
[1219 X 914 X 305]

 


RIGHT SIDE VIEW

STD Electrical v4.3 BAR = 1" AT PLOT SCALE

COMPANY CONFIDENTIAL INFORMATION THIS DOCUMENT AND ALL INFORMATION CONTAINED HEREIN, INCLUDING THE DESIGN CONCEPTS AND THOSE ARISING THEREFROM, ARE THE PROPERTY OF EVOQUA AND/OR ITS AFFILIATES AND ARE SUBMITTED IN CONFERENCE. THEY MAY BE USED ONLY FOR THE EXPRESS PURPOSE FOR WHICH THEY ARE PROVIDED AND MUST NOT BE DISCLOSED, REPRODUCED, OR COPIED IN ANY FORM, INCLUDING IN ELECTRONIC FORMAT, LOANED OR USED IN ANY OTHER MANNER WITHOUT THE EXPRESS WRITTEN CONSENT OF EVOQUA. ALL PATENT RIGHTS ARE RESERVED. THIS DOCUMENT AND DERIVATIVE WORKS THEREOF ARE PROTECTED UNDER APPLICABLE COPYRIGHT LAWS. UPON DEMAND OF EVOQUA, THIS DOCUMENT, ALONG WITH ALL COPIES AND EXTRACTS, AND ALL RELATED NOTES AND ANALYSES MUST BE RETURNED TO EVOQUA OR DESTROYED, AS INSTRUCTED BY EVOQUA. ACCEPTANCE OF THE DELIVERY OF THIS DOCUMENT CONSTITUTES AGREEMENT TO THESE TERMS.							DWN BY:	DATE:	TITLE:			
							M.KALIRA	2023-11-28	ELECTRICAL SCHEMATICS & ENCLOSURE DIAGRAMS (cETLus) CONTAINERIZED 2-PASS RO WITH PRETREATMENT RO PANEL - SKID 0300			
							CKD BY:	DATE:	CLIENT:			
							S.THANGA	2023-11-28	ELECTRIC HYDROGEN BEAUMONT, TX			
							APPD BY:	DATE:				
							K.KISITU	2023-11-28				
							MGD BY:	SCALE:				
							P.RYAN	NTS	 EVOQUA WATER TECHNOLOGIES COLORADO SPRINGS CO USA +1 719-570-9600			
1	REVISE SCHEMATIC NOTE #3 & ETHERNET SWITCH CHANGE	2024-05-14	C.HANER	K.KALUNG	K.KALUNG	ECM127665						
0	ISSUED FOR CONSTRUCTION	2023-12-28	M.KALIRA	S.THANGA	K.KISITU	N/A						
REV	DESCRIPTION	DATE	DWN	CKD	APPD	ECN	PART NUMBER	PROJ/PROD NUMBER	CODE	FILE/DRAWING NUMBER	SHEET	REV
							W3T602507	2034/001845	EC-DOS03	V112057483-17	17 OF 21	1

STD: Electrical v4.3		BAR = 1" AT PLOT SCALE
----------------------	---	------------------------

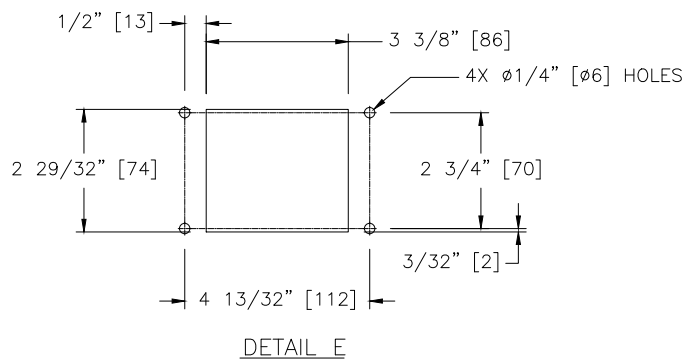

										COMPANY CONFIDENTIAL INFORMATION THIS DOCUMENT AND ALL INFORMATION CONTAINED HEREIN, INCLUDING THE DESIGN CONCEPTS AND THOSE APPROPRIATE INFORMATION, IS THE PROPERTY OF EVOQUA AND/OR ITS AFFILIATES AND ARE SUBMITTED IN CONFIDENCE. THEY MAY BE USED ONLY FOR THE EXPRESS PURPOSE FOR WHICH THEY ARE PROVIDED AND MUST NOT BE DISCLOSED, REPRODUCED, OR COPIED IN ANY FORM, INCLUDING IN ELECTRONIC FORMAT, LOANED OR USED IN ANY OTHER MANNER, WITHOUT THE EXPRESS WRITTEN CONSENT OF EVOQUA. ALL PATENT RIGHTS ARE RESERVED. THIS DOCUMENT AND DERIVATIVE WORKS THEREOF ARE PROTECTED BY U.S. AND INTERNATIONAL COPYRIGHT LAWS. NO PART OF EVOQUA, THIS DOCUMENT, ALONG WITH ALL COPIES AND EXTRACTS, AND ALL RELATED NOTES AND ANALYSES MUST BE RETURNED TO EVOQUA OR DESTROYED AS INSTRUCTED BY EVOQUA. ACCEPTANCE OF THE DELIVERY OF THIS DOCUMENT CONSTITUTES AGREEMENT TO THESE TERMS.										DWN BY: M.KALIRA DATE: 2023-11-28 CKD BY: S.THANGA DATE: 2023-11-28 APPD BY: K.KISITU DATE: 2023-11-28 MGD BY: P.PRYAN SCALE: NTS		TITLE ELECTRICAL SCHEMATICS & ENCLOSURE DIAGRAMS (cETLus) CONTAINERIZED 2-PASS RO WITH PRETREATMENT RO PANEL - SKID 0300 CLIENT ELECTRIC HYDROGEN BEAUMONT, TX		 EVOQUA WATER TECHNOLOGIES EVORA ROAD, SUITE 200 FARMINGTON, CT 06030 USA +1 719-570-9600		EVOQUA WATER TECHNOLOGIES EVORA ROAD, SUITE 200 FARMINGTON, CT 06030 USA +1 719-570-9600									
1	REVISE SCHEMATIC NOTE #3 & ETHERNET SWITCH CHANGE					C.HANER	K.KALLUNG	K.KALLUNG	ECM127665																										
0	ISSUED FOR CONSTRUCTION					2023-12-28	M.KALIRA	S.THANGA	K.KISITU	N/A																									
REV	DESCRIPTION					DATE	DWN	CKD	APPD	ECN	PART NUMBER		PROJECT/PROJ NUMBER		CODE		FILEDRAWING NUMBER		SHEET		REV														
						2023-12-28					W3T602507		2034/001845		EC-DOS03		V1120057483-18		OF 21		1														

STD: Electrical v4.3



							COMPANY CONFIDENTIAL INFORMATION THIS DOCUMENT AND ALL INFORMATION CONTAINED HEREIN, INCLUDING THE DESIGN CONCEPTS AND THOSE ARISING THEREFROM, ARE THE PROPERTY OF EVUQUA AND/OR ITS AFFILIATES AND ARE SUBMITTED IN CONFIDENCE. THEY MAY BE USED ONLY FOR THE EXPRESS PURPOSES FOR WHICH THEY ARE PROVIDED AND MAY NOT BE DISCLOSED, REPRODUCED, COPIED IN ANY FORM, INCLUDING IN ELECTRONIC OR PRINT, LOANED OR OTHERWISE TRANSMITTED WITHOUT THE EXPRESS WRITTEN CONSENT OF EVUQUA. ALL PATENT RIGHTS ARE RESERVED. THIS DOCUMENT AND DERIVATIVE WORKS THEREOF ARE PROTECTED UNDER U.S. PATENT AND COPYRIGHT LAWS AND LAWS OF EVUQUA. THIS DOCUMENT, ALONG WITH ALL COPIES AND EXTRACTS, AND ALL RELATED ITEMS AND ANALYSES MUST BE RETURNED TO EVUQUA OF REQUEST. ANY VIOLATION OF THIS AGREEMENT OR THE DELIVERY OF THIS DOCUMENT CONSTITUTES AN AGREEMENT TO THESE TERMS.		OWN BY: K.MALLIRA DATE: 2023-11-28 CKD BY: S.THANGA DATE: 2023-11-28 APPD BY: K.KISITU DATE: 2023-11-28 MGD BY: P.PRYAN SCALE: NTS		TITLE: ELECTRICAL SCHEMATICS & ENCLOSURE DIAGRAMS (cETLus) CONTAINERIZED 2-PASS RO WITH PRETREATMENT RO PANEL - SKID 0300 CLIENT: ELECTRIC HYDROGEN BEAUMONT, TX					
1	REVISE SCHEMATIC NOTE #3 & ETHERNET SWITCH CHANGE	2024-05-14	C.HANER	K.KALLANG	K.KALLANG	ECM127665										
0	ISSUED FOR CONSTRUCTION	2024-12-28	M.KALLIRA	S.THANGA	K.KISITU	N/A			 EVOQUA WATER TECHNOLOGIES COLORADO SPRINGS CO USA +1 719-570-9600							
REV	DESCRIPTION	DATE	DWN	CKD	APPD	ECN	PART NUMBER		PROJ/PROD NUMBER		CODE	FILE/DRAWING NUMBER	SHEET	OF	REV	
							W3T602507		2034/001845		EC-DOS03	V112057483-19	19	OF 21	1	

[illegible]

