

NOTES: UNLESS OTHERWISE SPECIFIED.
1. ALL DIMENSIONS ARE IN INCHES. ALL TOLERANCES ARE +/- 0.5 INCHES.



Project No.: 22MH194

8027

Tag No.:

- | | |
|---|---|
| 1 | Approved Without Comments |
| 2 | Approved With Comments; Revise and Resubmit |
| 3 | Revise and Resubmit |
| 4 | For Information Only |
| 5 | Certified as Final Data |


Julie Walker

Procurement/Vendor Data Contact

7/24/2024

Date

GENERAL ARRANGEMENT SPECIFICATION	
SKID LENGTH	506.45"
SKID WIDTH	96.00"
SKID HEIGHT	115.48"
SKID WEIGHT DRY	31600 lbs
SKID WEIGHT WET(OPERATING)	46600 lbs

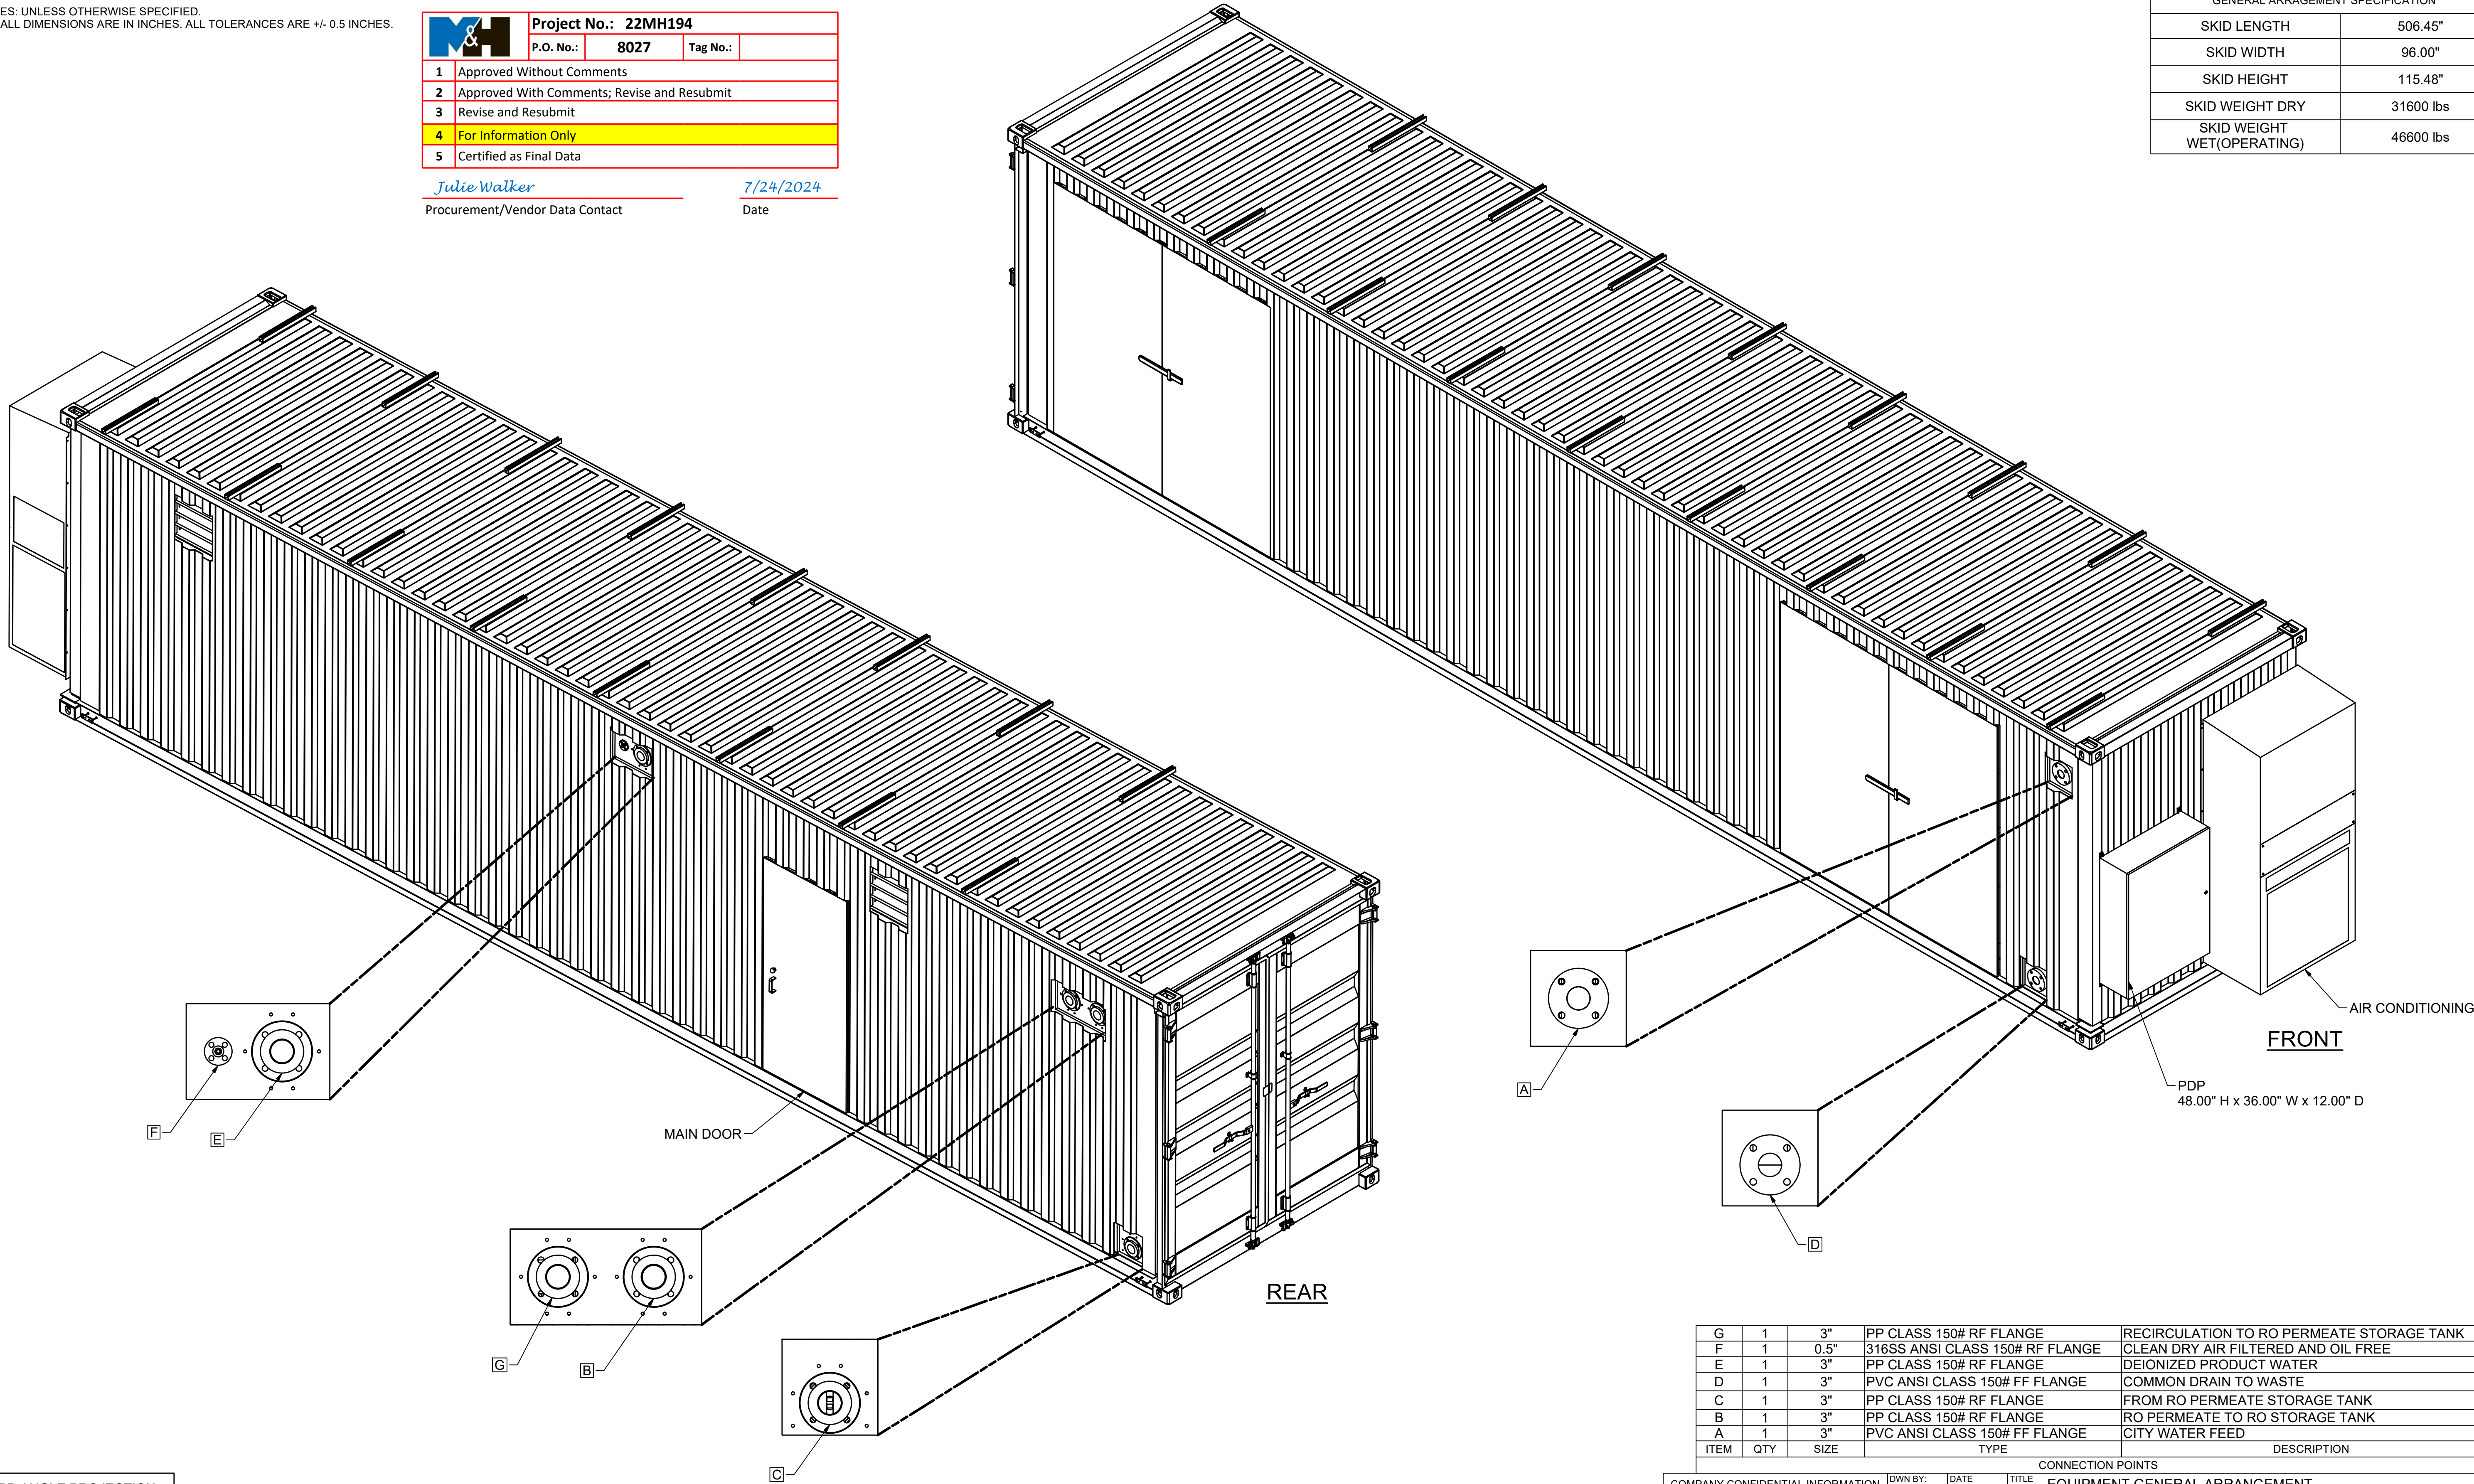


G	1	3"	PP CLASS 150# RF FLANGE	RECIRCULATION TO RO PERMEATE STORAGE TANK
F	1	0.5"	316SS ANSI CLASS 150# RF FLANGE	CLEAN DRY AIR FILTERED AND OIL FREE
E	1	3"	PP CLASS 150# RF FLANGE	DEIONIZED PRODUCT WATER
D	1	3"	PVC ANSI CLASS 150# FF FLANGE	COMMON DRAIN TO WASTE
C	1	3"	PP CLASS 150# RF FLANGE	FROM RO PERMEATE STORAGE TANK
B	1	3"	PP CLASS 150# RF FLANGE	RO PERMEATE TO RO STORAGE TANK
A	1	3"	PVC ANSI CLASS 150# FF FLANGE	CITY WATER FEED
ITEM	QTY	SIZE	TYPE	DESCRIPTION


COMPANY CONFIDENTIAL INFORMATION

THIS DOCUMENT AND ALL INFORMATION CONTAINED HEREIN, INCLUDING THE DESIGN CONCEPTS AND THOSE ARISING THEREFROM ARE THE PROPERTY OF EVEQUO, AND/OR ITS AFFILIATES AND ARE SUBMITTED IN CONFIDENCE. THEY MAY BE USED ONLY FOR THE EXPRESS PURPOSE FOR WHICH THEY ARE PROVIDED AND MUST NOT BE REPRODUCED, COPIED, OR USED IN ANY FORM, INCLUDING IN ELECTRONIC FORM, LOANED OR USED IN ANY OTHER MANNER WITHOUT THE EXPRESS WRITTEN CONSENT OF EVEQUO. ALL PATENT RIGHTS ARE RESERVED BY EVEQUO. ALL RIGHTS NOT EXPRESSLY SET FORTH ARE PROTECTED UNDER APPLICABLE COPYRIGHT LAWS. UPON DEMAND OF EVEQUO, THIS DOCUMENT, ALONG WITH ALL COPIES AND EXTRACTS, AND ALL RELATED NOTES AND ANALYSES MUST BE RETURNED TO EVEQUO. ACCEPTANCE OF THE DELIVERY OF THIS DOCUMENT CONSTITUTES AGREEMENT TO THESE TERMS.


DWN BY:	DATE
S.SUKUMA	2024-01-09
CKD BY:	DATE
D.DHANAP	2024-01-09
APPD BY:	DATE
J.FOURNI	2024-01-09
MGD BY:	SCALE
P.RYAN	NTS
PART NUMBER W3T602504	

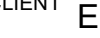TITLE EQUIPMENT GENERAL ARRANGEMENT CONTAINERIZED 2-PASS RO WITH PRETREATMENT SKID,MOBILE 2034/001845-0100 RO/DI/UV				
CLIENT ELECTRIC HYDROGEN BEAUMONT, TX				
 evoQUA WATER TECHNOLOGIES EVOQUA WATER TECHNOLOGIES COLORADO SPRINGS CO USA +1 719-570-9600				
PROJ/PROD NUMBER 2034/001845	CODE M-GA01	FILE/DRAWING NUMBER V113616762	SHEET 1 OF 4	REV 2

THIRD ANGLE PROJECTION

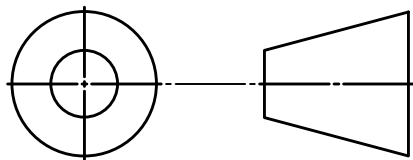


2	RECIRCULATION LINE CHANGE	2024-02-16	R.SURESH	D.DHANAP	N.VLACIC	127120
1	MOVED TIE POINT F AND E TOWARDS LEFT OVER 0.5" & GROUNDING LUG ADDED	2024-01-29	D.SUJI	D.DHANAP	J.FOURNI	127000
0	ISSUED FOR CONSTRUCTION	2024-01-09	S.SUKUMA	D.DHANAP	J.FOURNI	
REV	DESCRIPTION	DATE	DWN	CKD	APPD	ECN

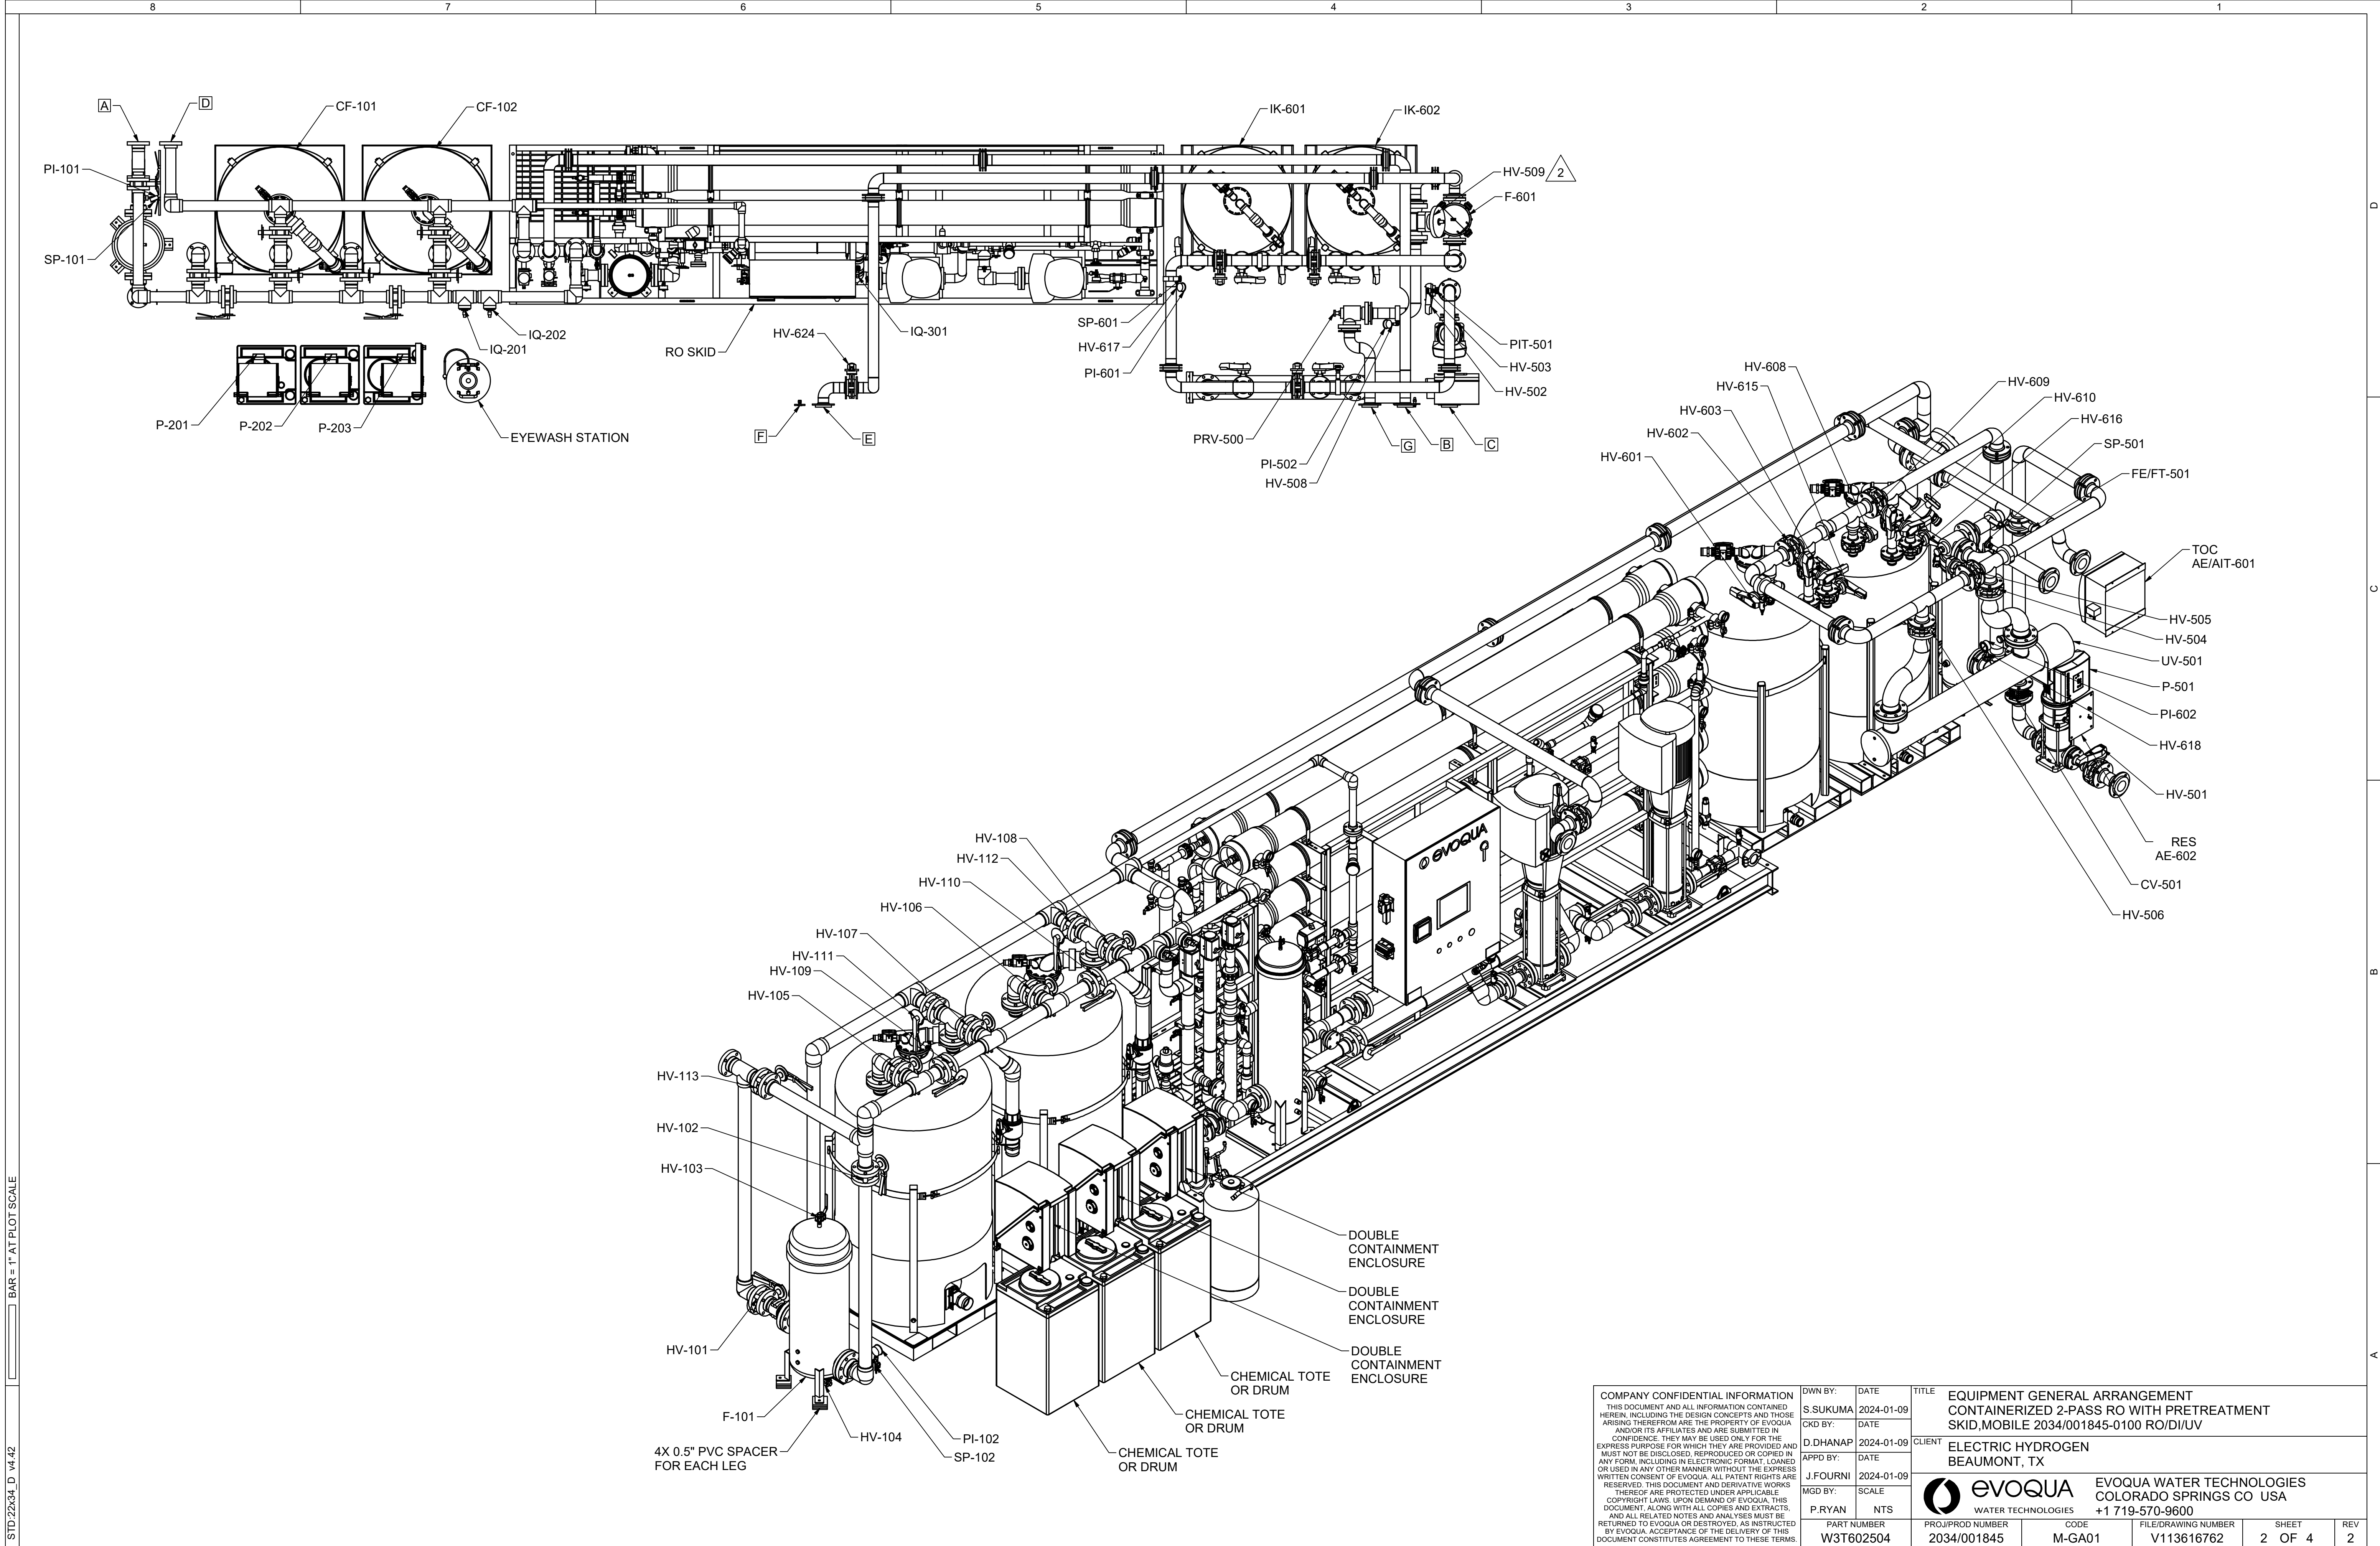

STD:22x34_D v4.42 BAR = 1" AT PLOT SCALE

COMPANY CONFIDENTIAL INFORMATION		DWN BY:	DATE	TITLE			
THIS DOCUMENT AND ALL INFORMATION CONTAINED HEREIN, INCLUDING THE DESIGN CONCEPTS AND THOSE ARISING THEREFROM ARE THE PROPERTY OF EVOQUA AND/OR ITS AFFILIATES AND ARE SUBMITTED IN CONFIDENCE. THEY MAY BE USED ONLY FOR THE EXPRESS PURPOSE FOR WHICH THEY ARE PROVIDED AND MUST NOT BE DISCLOSED, REPRODUCED OR COPIED IN ANY FORM, INCLUDING IN ELECTRONIC FORMAT, LOANED OR USED IN ANY OTHER MANNER WITHOUT THE EXPRESS WRITTEN CONSENT OF EVOQUA. ALL PATENT RIGHTS ARE RESERVED. THIS DOCUMENT AND DERIVATIVE WORKS THEREOF ARE PROTECTED UNDER APPLICABLE COPYRIGHT LAWS. UPON DEMAND OF EVOQUA, THIS DOCUMENT, ALONG WITH ALL COPIES AND EXTRACTS, AND ALL RELATED NOTES AND ANALYSES MUST BE RETURNED TO EVOQUA OR DESTROYED, AS INSTRUCTED BY EVOQUA. ACCEPTANCE OF THE DELIVERY OF THIS DOCUMENT CONSTITUTES AGREEMENT TO THESE TERMS.		S.SUKUMA	2024-01-09	EQUIPMENT GENERAL ARRANGEMENT CONTAINERIZED 2-PASS RO WITH PRETREATMENT SKID,MOBILE 2034/001845-0100 RO/DI/UV			
		CKD BY:	DATE	CLIENT			
		D.DHANAP	2024-01-09	ELECTRIC HYDROGEN BEAUMONT, TX			
		APPD BY:	DATE				
		J.FOURNI	2024-01-09				
		MGD BY:	SCALE	 EVOQUA WATER TECHNOLOGIES COLORADO SPRINGS CO USA +1 719-570-9600			
		P.RYAN	NTS	WATER TECHNOLOGIES			
PART NUMBER		PROJ/PROD NUMBER		CODE	FILE/DRAWING NUMBER	SHEET	REV
W3T602504		2034/001845		M-GA01	V113616762	2 OF 4	2

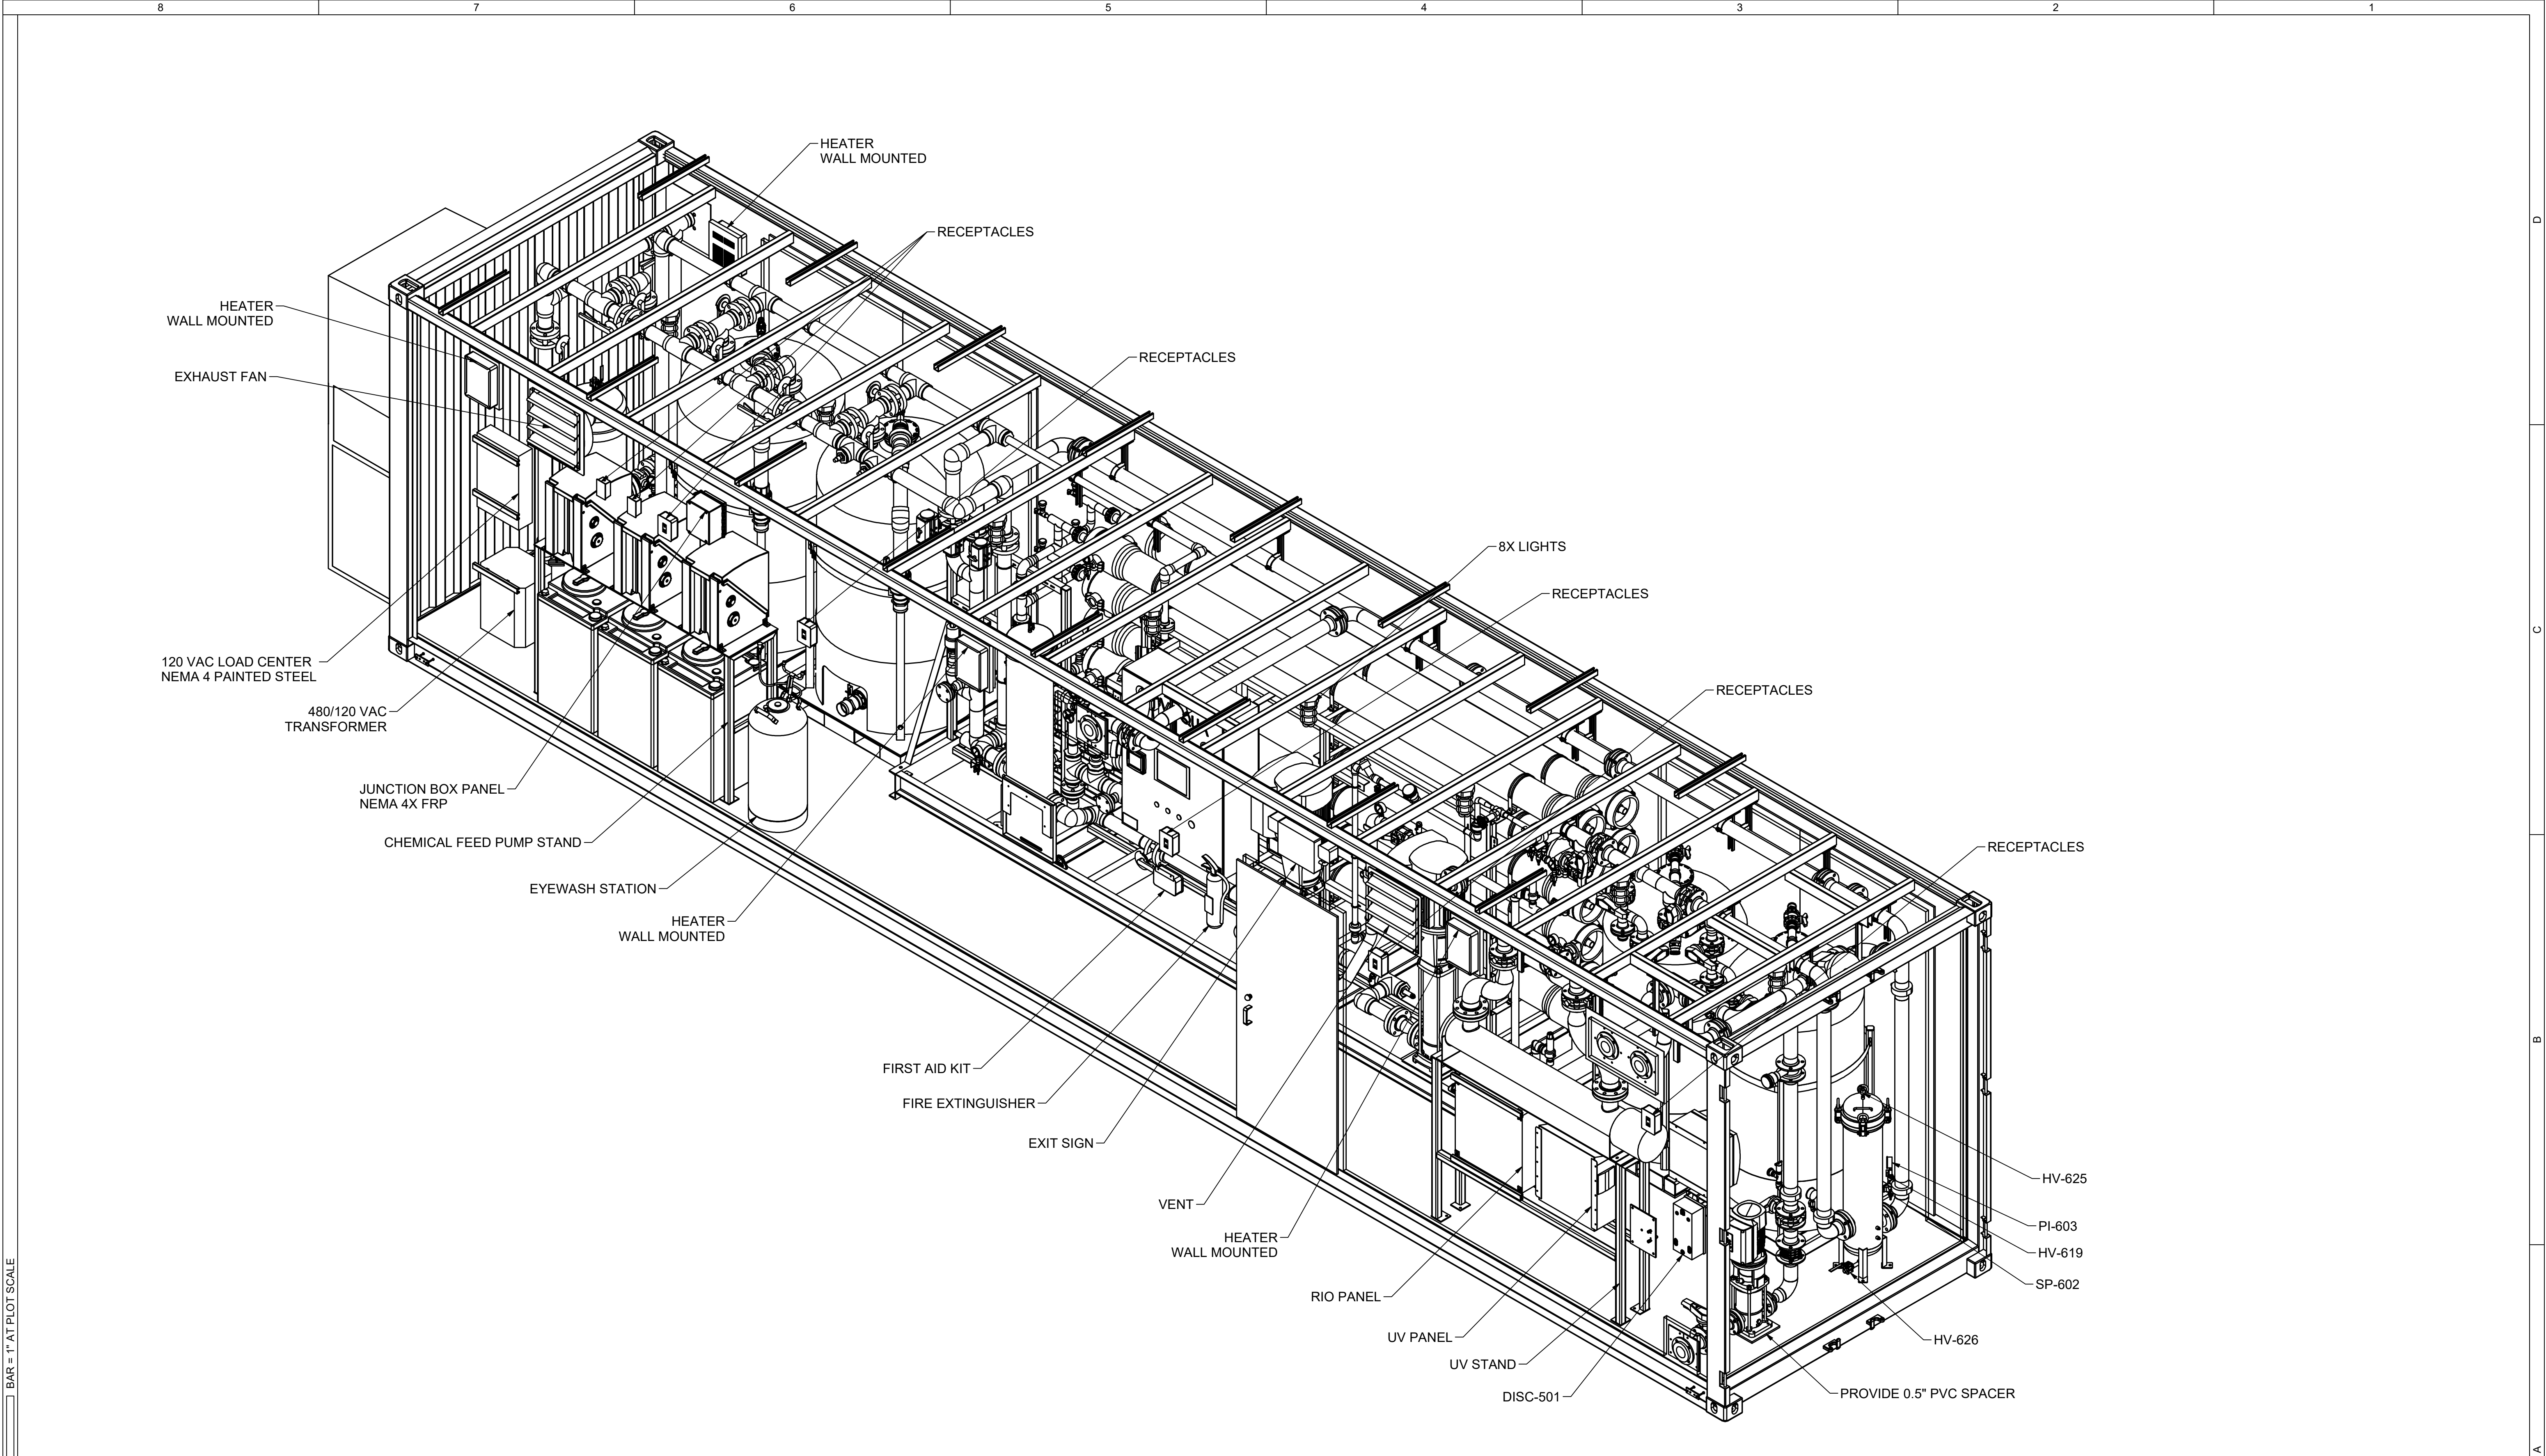

STD:22x34_D v4.42 BAR = 1" AT PLOT SCALE

COMPANY CONFIDENTIAL INFORMATION THIS DOCUMENT AND ALL INFORMATION CONTAINED HEREIN, INCLUDING THE DESIGN CONCEPTS AND THOSE ARISING THEREFROM ARE THE PROPERTY OF EVOQUA AND/OR ITS AFFILIATES AND ARE SUBMITTED IN CONFIDENCE. THEY MAY BE USED ONLY FOR THE EXPRESS PURPOSE FOR WHICH THEY ARE PROVIDED AND MUST NOT BE DISCLOSED, REPRODUCED OR COPIED IN ANY FORM, INCLUDING IN ELECTRONIC FORMAT, LOANED OR USED IN ANY OTHER MANNER WITHOUT THE EXPRESS WRITTEN CONSENT OF EVOQUA. ALL PATENT RIGHTS ARE RESERVED. THIS DOCUMENT AND DERIVATIVE WORKS THEREOF ARE PROTECTED UNDER APPLICABLE COPYRIGHT LAWS. UPON DEMAND OF EVOQUA, THIS DOCUMENT, ALONG WITH ALL COPIES AND EXTRACTS, AND ALL RELATED NOTES AND ANALYSES MUST BE RETURNED TO EVOQUA OR DESTROYED, AS INSTRUCTED BY EVOQUA. ACCEPTANCE OF THE DELIVERY OF THIS DOCUMENT CONSTITUTES AGREEMENT TO THESE TERMS.				DWN BY: S.SUKUMA CKD BY: D.DHANAP APPD BY: J.FOURNI MGD BY: P.RYAN	DATE: 2024-01-09 DATE: 2024-01-09 DATE: 2024-01-09 SCALE: NTS	TITLE: EQUIPMENT GENERAL ARRANGEMENT CONTAINERIZED 2-PASS RO WITH PRETREATMENT SKID,MOBILE 2034/001845-0100 RO/DI/UV CLIENT: ELECTRIC HYDROGEN BEAUMONT, TX	EVOQUA WATER TECHNOLOGIES COLORADO SPRINGS CO USA +1 719-570-9600				PART NUMBER: W3T602504	PROJ/PROD NUMBER: 2034/001845	CODE: M-GA01	FILE/DRAWING NUMBER: V113616762	SHEET: 3 OF 4	REV: 2
---	--	--	--	---	--	---	---	--	--	--	------------------------	-------------------------------	--------------	---------------------------------	---------------	--------

