
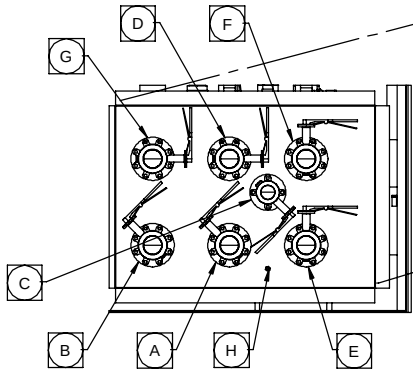


NOTES:

1. ALL DIMENSIONS ARE IN INCHES. (FOR REFERENCE ONLY)
2. ALL WEIGHTS ASSOCIATED WITH GENERAL ARRANGEMENT DRAWINGS ARE NOMINAL.
3. TAGS TO BE LAMICOID. HANG WITH TIE-WRAPs.
4. BOLT HOLE PATTERN OF FLANGES TO STRADDLE PRINCIPLE CENTERLINE OF PIPE.
5. ALL TUBING TO BE PE.
6. ALL FLANGE GASKETS TO BE EPDM UNLESS OTHERWISE NOTED.
7. ALL MOUNTING HARDWARE TO BE STAINLESS STEEL.
8. CONDUIT TO BE EMT. FLEXIBLE CONDUIT TO BE USED BETWEEN PUMP AND PANEL S.O. CABLE FOR ALL.
9. PRESSURE TEST ALL PNEUMATIC TUBING TO 90psi.
10. HYDROSTATICALLY LEAK TESTED TO 100psi.

General Table	
GENERAL ARRANGEMENT SPECIFICATIONS	
CONTAINER LENGTH	53'
CONTAINER WIDTH	8'-6"
CONTAINER HEIGHT	9'-6"
CONTAINER HEIGHT (INSIDE)	103 7/8"
WEIGHT DRY	28K LB
WEIGHT WET	34K LB

The proposed container shall be a standard 40 feet long and equipment to be customize per process on P&ID provided.
The RO in this trailer is a 100 GPM product staged unit and the proposed 80 GPM RO will be the same width.

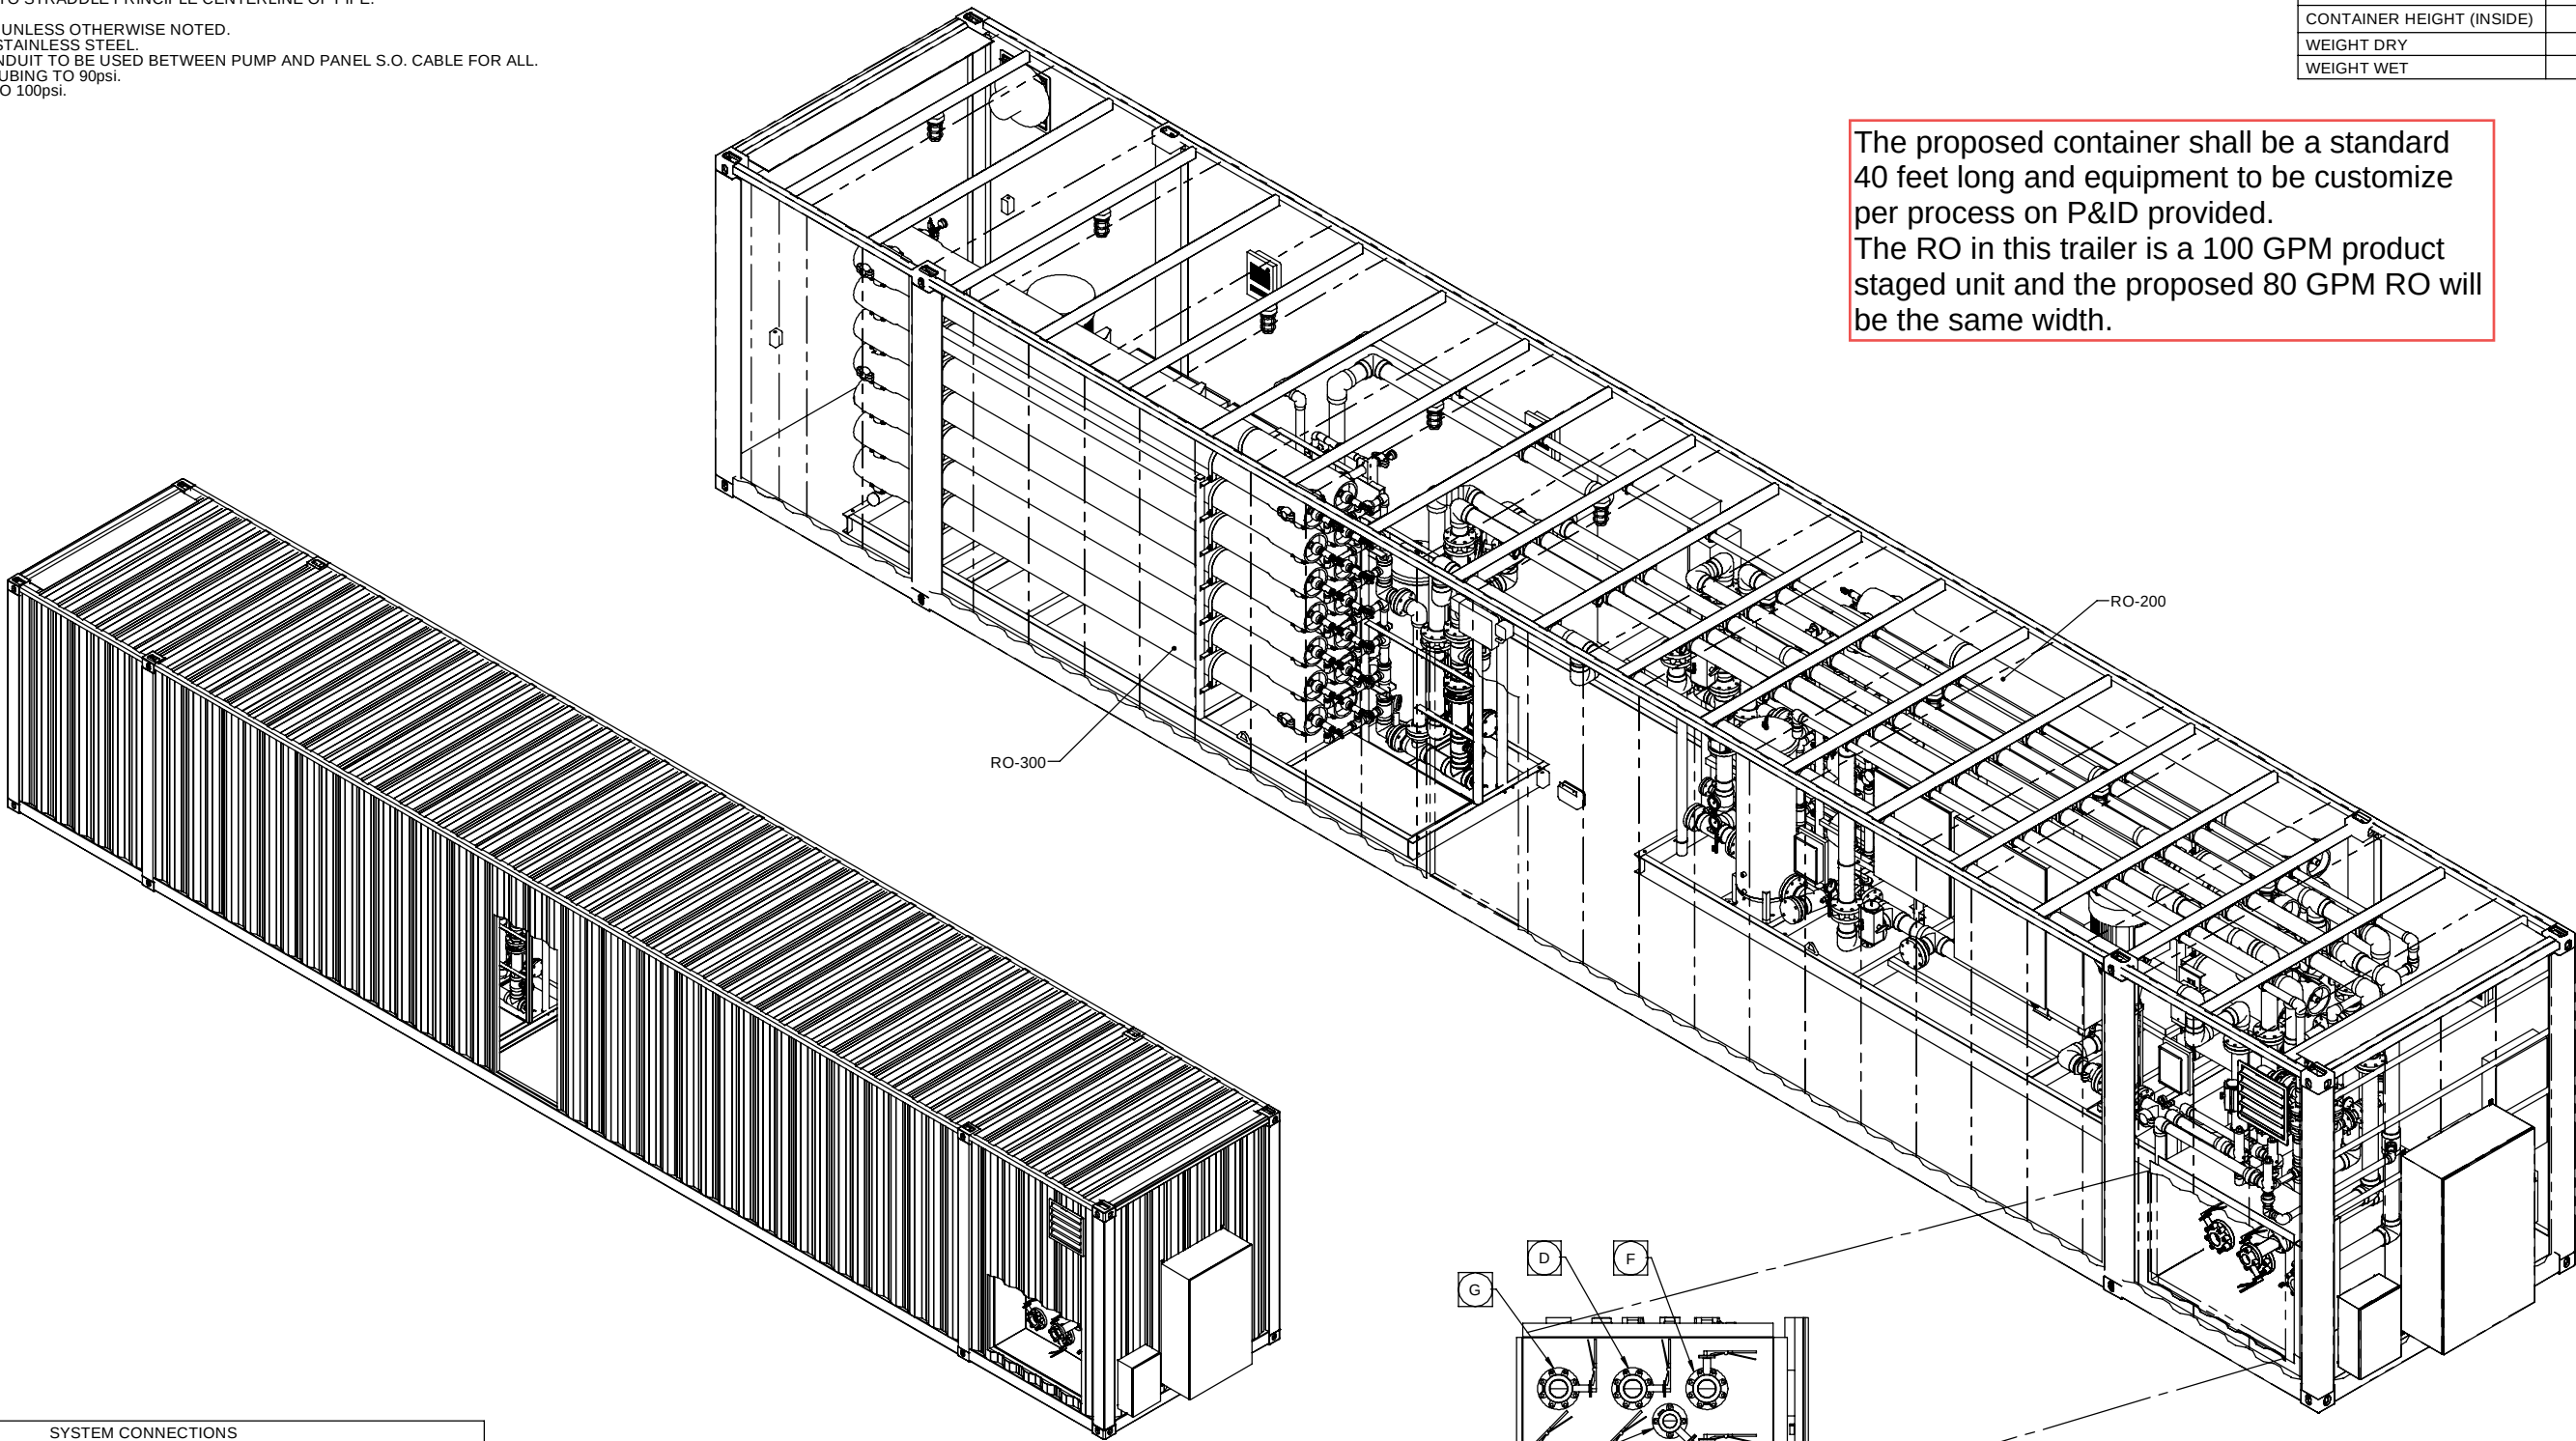

SYSTEM CONNECTIONS	
A	4" PVC SCH80 FLANGED, FEED WATER (RO 200)
B	4" PVC SCH80 FLANGED, FEED WATER (RO300)
C	3" PVC SCH80 FLANGED, CONCENTRATE
D	4" PVC SCH80 FLANGED, RO 300 S.P.P / DOUBLE P.P
E	4" PVC SCH80 FLANGED, SINGLE PASS PRODUCT (RO 200)
F	4" PVC SCH80 FLANGED, FLUSH WATER IN
G	4" PVC SCH80 FLANGED, PRODUCT DIVERT AND FLUSH TO DRAIN
H	1/2" NPT, CLEAN OIL FREE AIR

REV	DESCRIPTION	DATE	DWN	CHKD	APVD	ECN
0	ISSUED FOR MANUFACTURING	5/31/19	CGB	DRA	DRA	

TOLERANCES UNLESS OTHERWISE SPECIFIED	
FABRICATION UNDER 24" ±.06 24"-144" ±.125 OVER 144" ±.188	MACHINE .XX±.03 .XXX±.005
ANGULAR UNDER 72° ±.2°	
THIRD ANGLE PROJECTION	

COMPANY CONFIDENTIAL	
DOCUMENT AND ALL INFORMATION CONTAINED HEREIN ARE THE PROPERTY OF EVOQUA AND/OR ITS AFFILIATES. THE DESIGN CONCEPTS AND INFORMATION CONTAINED HEREIN ARE PROPRIETARY TO EVOQUA AND ARE SUBMITTED IN CONFIDENCE. THEY ARE NOT TRANSFERABLE AND MUST BE USED ONLY FOR THE PURPOSE FOR WHICH THE DOCUMENT IS EXPRESSLY LOANED. THEY MUST NOT BE DISCLOSED, REPRODUCED, LOANED OR USED IN ANY OTHER MANNER WITHOUT THE EXPRESS WRITTEN CONSENT OF EVOQUA. IN NO EVENT SHALL THEY BE USED IN ANY MANNER DETRIMENTAL TO THE INTEREST OF EVOQUA. ALL PATENT RIGHTS ARE RESERVED. UPON THE DEMAND OF EVOQUA, THIS DOCUMENT, ALONG WITH ALL COPIES AND EXTRACTS, AND ALL RELATED NOTES AND ANALYSES, MUST BE RETURNED TO EVOQUA OR DESTROYED, AS INSTRUCTED BY EVOQUA. ACCEPTANCE OF THE DELIVERY OF THIS DOCUMENT CONSTITUTES AGREEMENT TO THESE TERMS.	

DESIGNER	DATE
CGB	5/21/19
CHECKER	DATE
DRA	5/21/19
ENGINEER	DATE
DRA	5/21/19
MANAGER	DATE
PBR	5/21/19
SCALE:	1:26



PROJECT

MST+02

SAP NUMBER

W3T452240

DRAWING

0100

SHEET

1

OF

7


REV

0

WATER TECHNOLOGIES

COLORADO SPRINGS, CO

719-570-9600

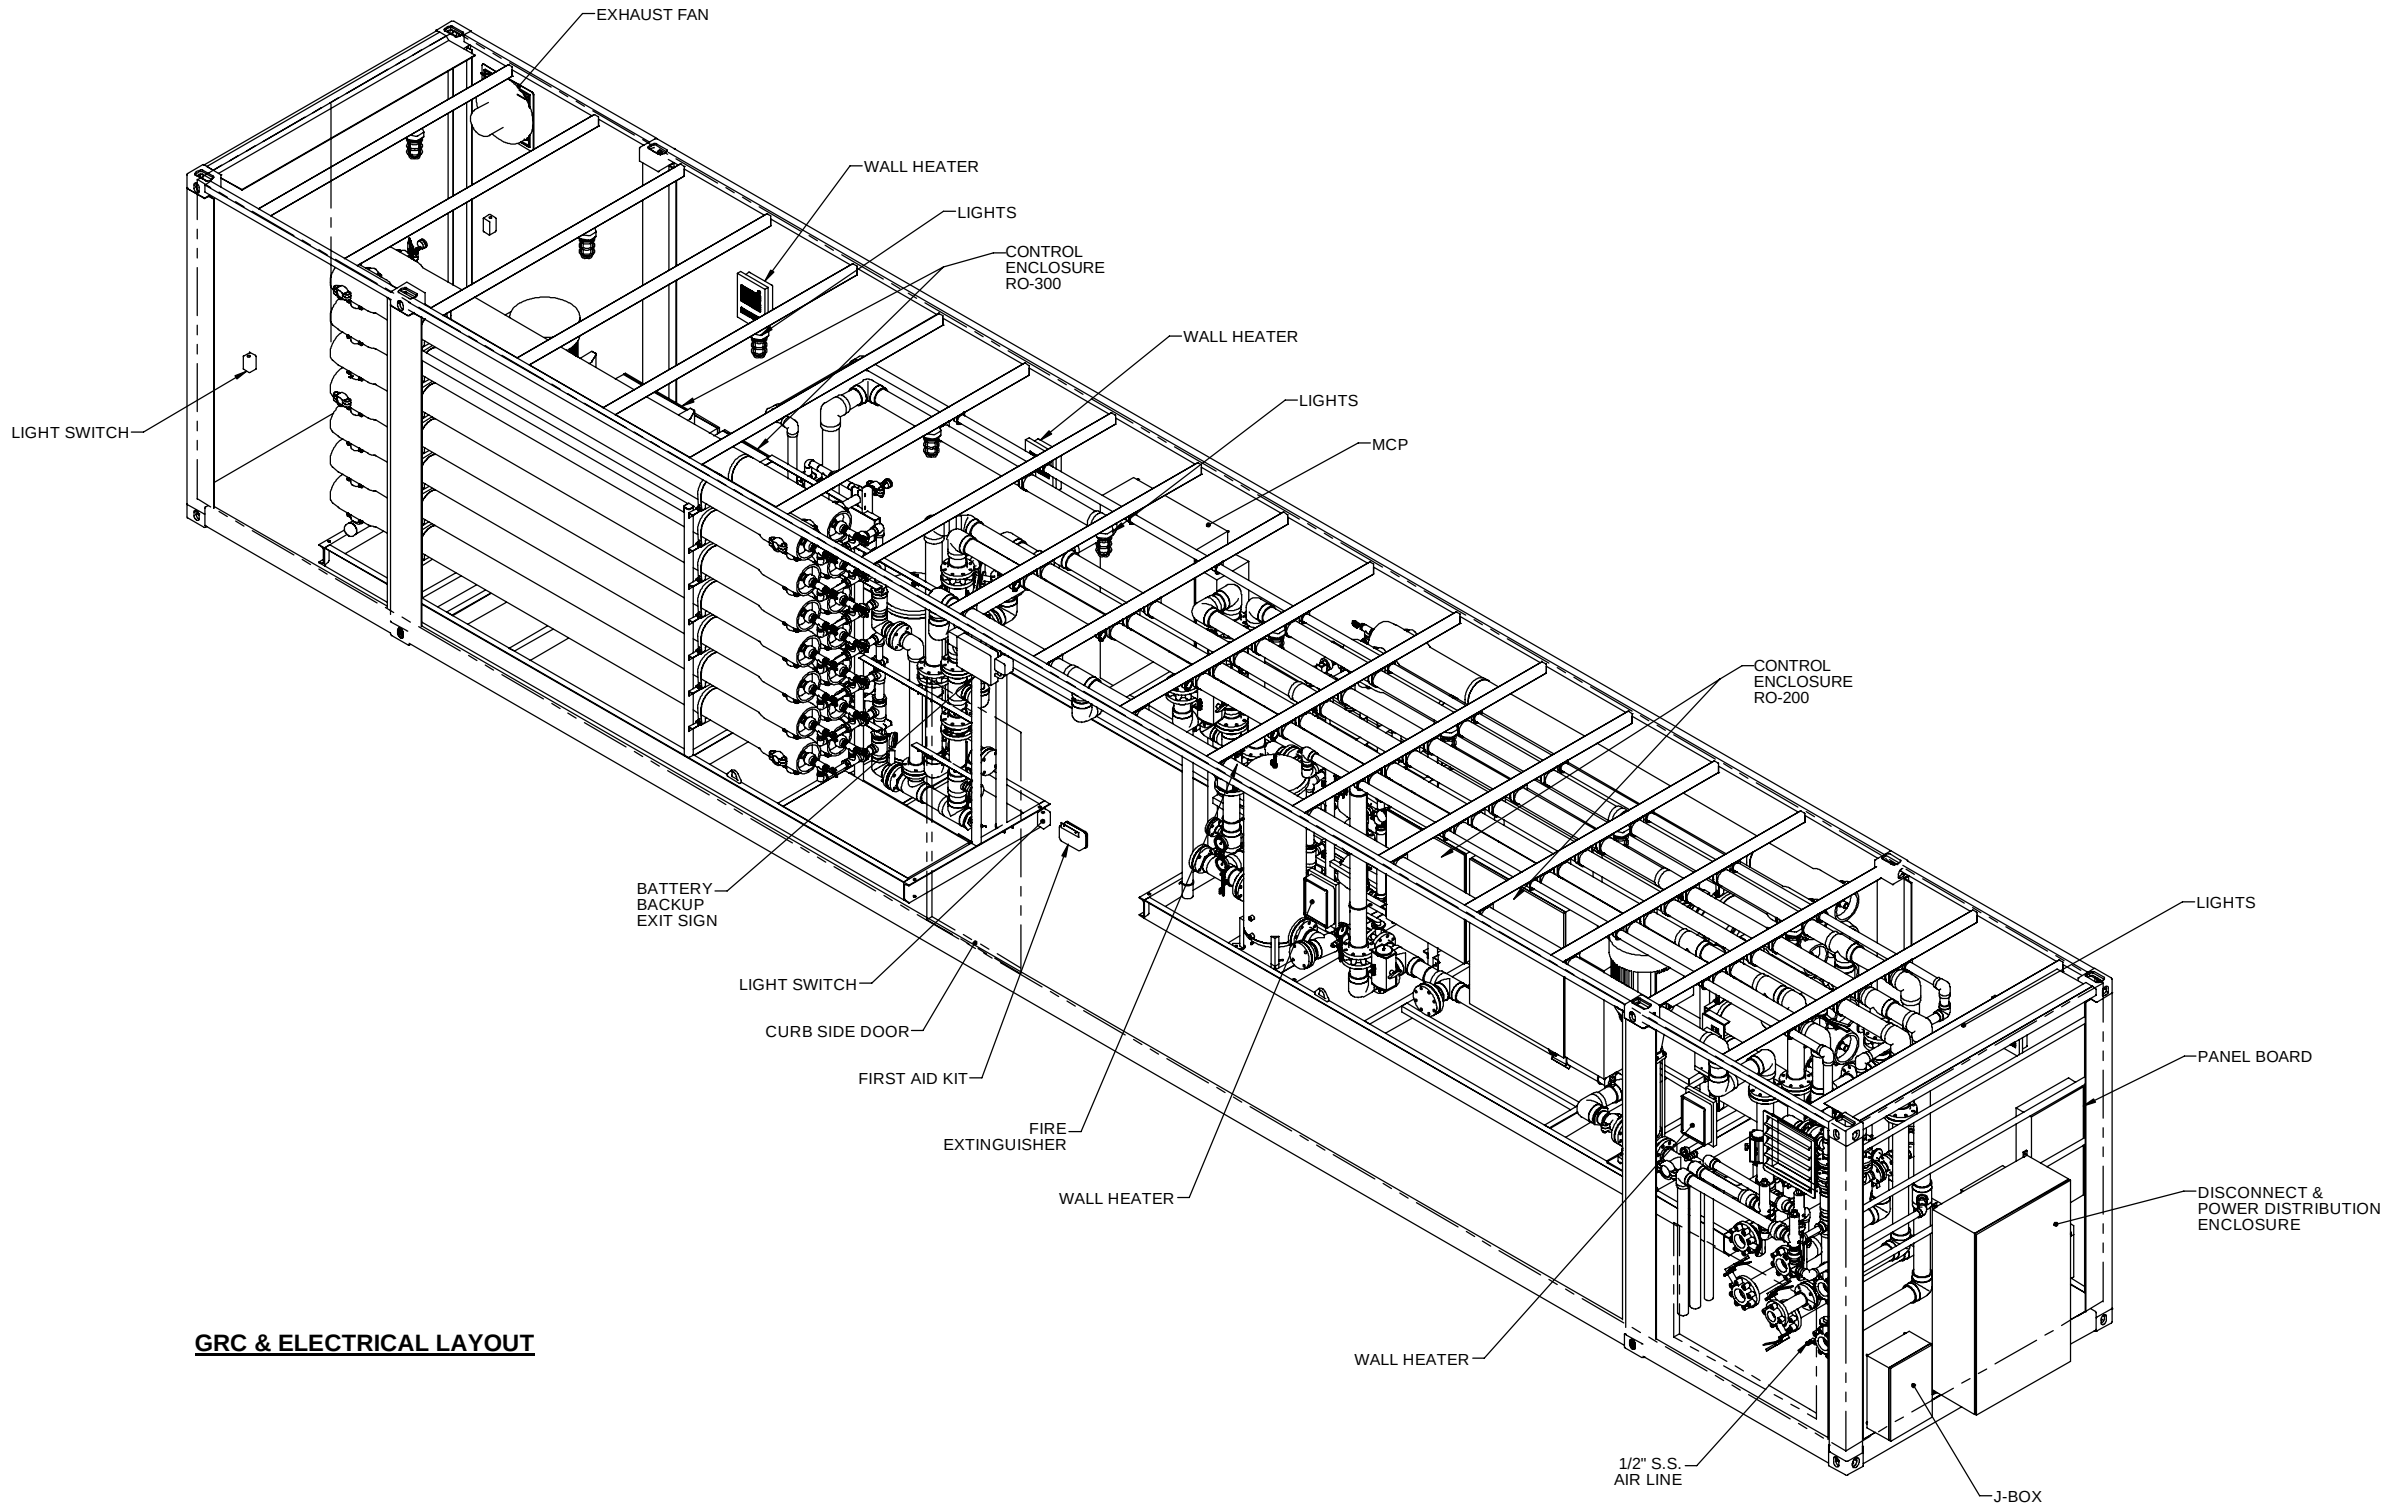

GRC & ELECTRICAL LAYOUT

TOLERANCES UNLESS OTHERWISE SPECIFIED		COMPANY CONFIDENTIAL		DESIGNER	DATE	TITLE			
FABRICATION		DOCUMENT AND ALL INFORMATION CONTAINED HEREIN ARE THE PROPERTY OF EVOQUA AND/OR ITS AFFILIATES. THE DESIGN CONCEPTS AND INFORMATION CONTAINED HEREIN ARE PROPRIETARY TO EVOQUA AND ARE SUBMITTED IN CONFIDENCE. THEY ARE NOT TRANSFERABLE AND MUST BE USED ONLY FOR THE PURPOSE FOR WHICH THE DOCUMENT IS EXPRESSLY LOANED. THEY MUST NOT BE DISCLOSED, REPRODUCED, LOANED OR USED IN ANY OTHER MANNER WITHOUT THE EXPRESS WRITTEN CONSENT OF EVOQUA. IN NO EVENT SHALL THE INTEREST OF EVOQUA, ALL PATENT RIGHTS ARE RESERVED. UPON THE DEMAND OF EVOQUA, THIS DOCUMENT, ALONG WITH ALL COPIES AND EXTRACTS, AND ALL RELATED NOTES AND ANALYSES, MUST BE RETURNED TO EVOQUA OR DESTROYED, AS INSTRUCTED BY EVOQUA. ACCEPTANCE OF THE DELIVERY OF THIS DOCUMENT CONSTITUTES AGREEMENT TO THESE TERMS.		CGB	5/21/19				
MACHINE		CHECKER	DATE						
UNDER 24" ±.06		DRA	5/21/19						
24" - 144" ±.125		ENGINEER	DATE						
OVER 144" ±.188		DRA	5/21/19						
ANGULAR		MANAGER	DATE	PROJECT		SAP NUMBER	DRAWING	SHEET	REV
UNDER 72" ±.2"		PBR	5/21/19	MST+02		W3T452240	0100	2 OF 7	0
THIRD ANGLE PROJECTION		SCALE: 1:26		PROJECT					
				SAP NUMBER					

WATER TECHNOLOGIES
COLORADO SPRINGS, CO
719-570-9600